


UC = UNIDADE COMPACTA
AC = SISTEMA DE AR COMPRIMIDO
AM = ADENSAMENTO MECÂNICO
AS = AERADOR SUPERFICIAL
BO = BOMBAS
CA = CAÇAMBA
CL = CENTRÍFUGA
CL = SISTEMA DE CLORAÇÃO
CM = COM
CO = COMPORTAS
CS = CALHA SÓLIDOS
DI = DIFUSOR
DU = DISJUNTOR
DO = SISTEMA DE DOSAGEM
DS = DECANTADOR SUPERFICIAL
EL = ELETRODUTO
EN = ENTRADA DE ENERGIA
EX = EXAUSTOR
SS = SOFT STARTER

VT = VERTEDOR
RA = RASPADOR AREIA
RT = ROSCA TRANSPORTADORA
GG = QUINDASTE GRATÓRIO
GR = GRADE
MI = MISTURADOR
MN = MONOVIA
MO = MOTOR
OD = SISTEMA DE CONTROLE DE ODORES
PC = PARAFUSO CLASSIFICADOR
PE = PENEIRA ROTATIVA
PR = PONTE ROLANTE

PG = PAINEL DE TRANSFERÊNCIA DO GRUPO GERADOR
OB = QUADRO GERAL DE BAIXA TENSÃO
OC = QUADRO DE COMANDO
QF = QUADRO DE FORÇA
QI = QUADRO DE ILUMINAÇÃO
QM = CUBÍCULO MÊDIA TENSÃO
TR = TRANSFORMADOR
SC = INVERSOR DE FREQUÊNCIA
SO = SOPRADOR
XO = MAIS DE UM EQUIPAMENTO
TU = TUBULAÇÃO
VR = VALVULA DE RETENÇÃO
VG = VALVULA GAVETA
VB = VALVULA BORBOLETA
VE = VALVULA ESFERA
VS = VALVULA SOLENÓIDE
GE = GRUPO GERADOR

800 QUÍMICOS (RETORES NEREDA)

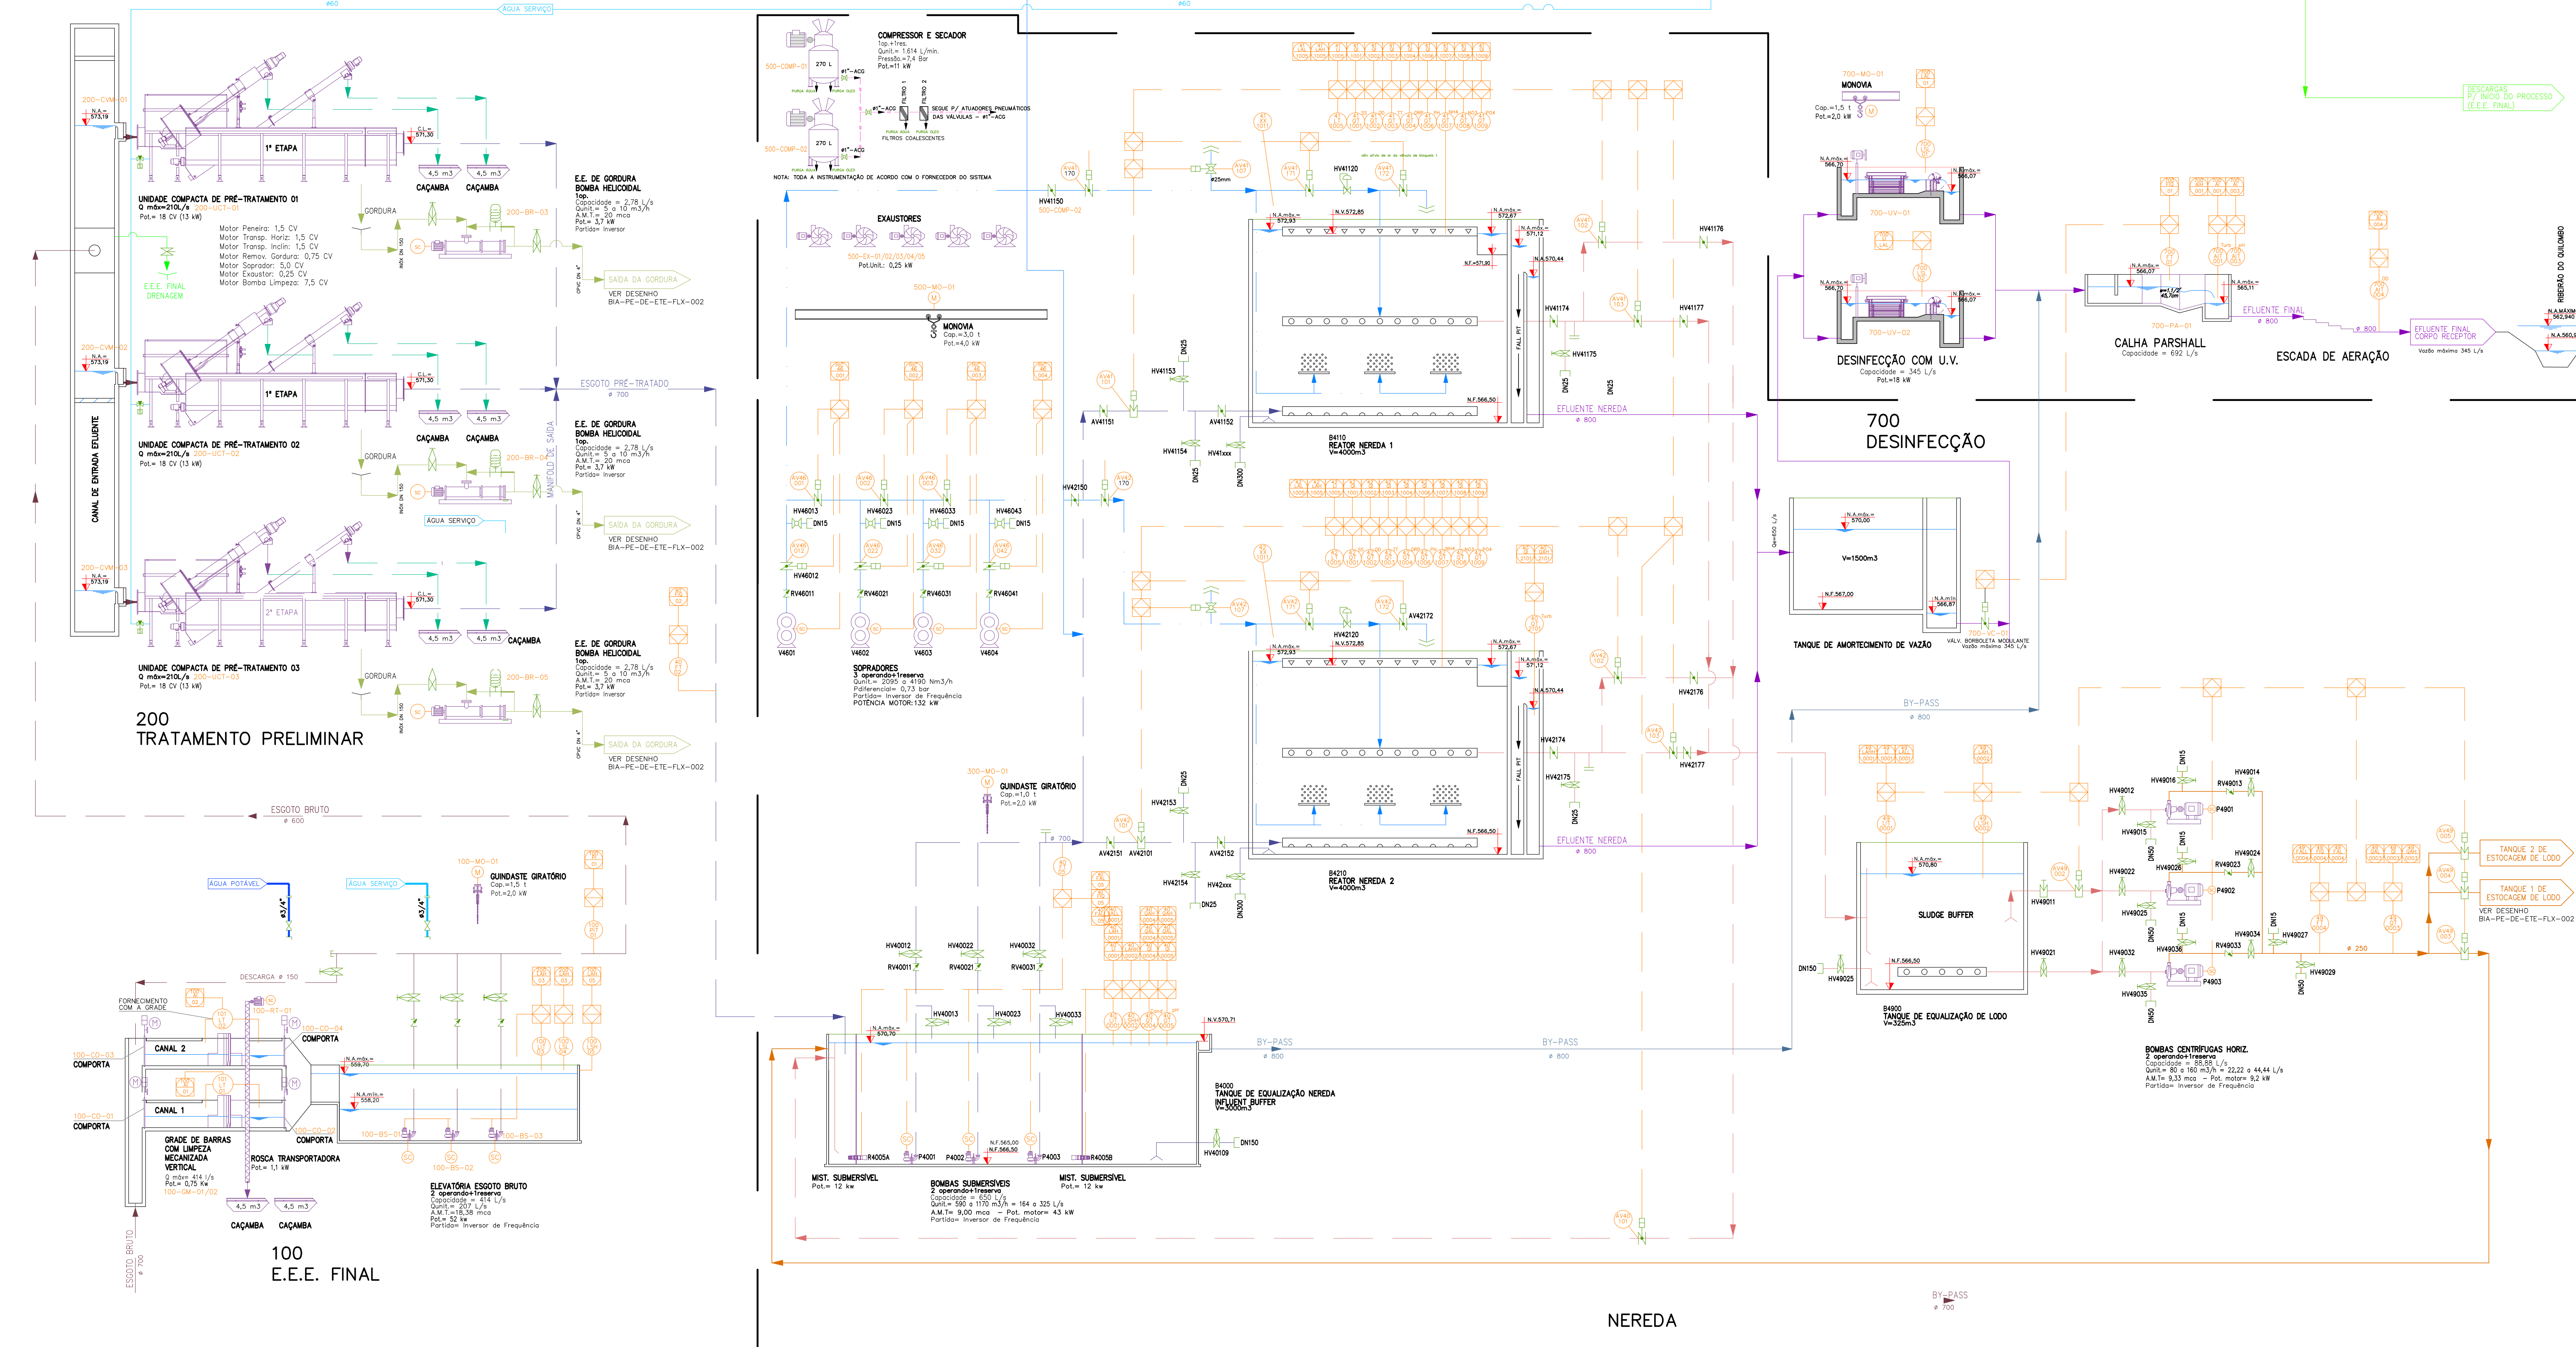

LEGENDA	
	TUBULAÇÃO DE ESGOTO BRUTO
	TUBULAÇÃO DE DRENAGEM
	TUBULAÇÃO DE ESPUMA
	TUBULAÇÃO DE ÁGUA DE SERVIÇO
	TUBULAÇÃO DE POLIETILENO
	TUBULAÇÃO DE BY-PASS
	TUBULAÇÃO RECALQUE DE LODO
	TUBULAÇÃO ÁGUA POTÁVEL
	TUBULAÇÃO DE AR SOPRADO
	TUBULAÇÃO DE HIPOCLORITO
	TUBULAÇÃO DE PRÉ-TRATADO
	TUBULAÇÃO DE EFLENTE REATORES
	TUBULAÇÃO DE CLORETO FÉRRICO
	DESCARTE DE AREIA
	VALVULA DE ALÍVIO
	MEDIDOR DE VAZÃO TIPO PARSHALL
	VALVULA SOLENÓIDE
	VALVULA BORBOLETA MANUAL
	VALVULA BORBOLETA MOTORIZADA
	VALVULA BORBOLETA AUTOMATIZADA
	VALVULA DE RETENÇÃO
	VALVULA GUILHOTINA MANUAL
	VALVULA GUILHOTINA PNEUMÁTICA
	VALVULA GLOBO MANUAL
	VALVULA GLOBO MOTORIZADA
	VALVULA GLOBO PNEUMÁTICA
	VALVULA ESFERA MANUAL
	VALVULA ESFERA MOTORIZADA
	VALVULA ESFERA PNEUMÁTICA
	VALVULA GAVETA MANUAL
	VALVULA GAVETA MOTORIZADA
	VALVULA GAVETA PNEUMÁTICA
	VALVULA DE CONTRAPRESSÃO
	FILTRO "Y"
	JUNTA DE DESMONTAGEM
	REDUÇÃO
	MANEIRA
	ENGATE RÁPIDO PARA ÁGUA DE SERVIÇO

	BOMBA SUBMERSA
	MISTURADOR SUBMERSÍVEL
	BOMBA CENTRÍFUGA
	BOMBA HELICOIDAL
	BOMBA ELETROMAGNÉTICA DIAFRAGMA
	MOTOR ELÉTRICO
	MOTOR ELÉTRICO COM ACIONAMENTO POR VARIADOR DE FREQUÊNCIA
	MOTOR ELÉTRICO PARA VALVULAS
	BOMBA CENTRÍFUGA SUBMERSÍVEL
	EXAUSTOR
	VENTILADOR
	SOPRADOR
	MISTURADOR VERTICAL
	COMPORTA MANUAL
	COMPORTA ACIONAMENTO MECÂNICO
	UNIDADES NEREDA

NOTAS

R1	REVISÃO 1	02/10/25	RSD	JG	RSD
00	EMISSÃO INICIAL	29/03/19	BIA	FC	BRK
REV.	DESCRIÇÃO	DATA	EXEC.	VERIF.	APROV.
AS INFORMAÇÕES DESTE DOCUMENTO SÃO DE PROPRIEDADE DA CONTRATANTE, SENDO PROIBIDA A UTILIZAÇÃO SEM PRÉVIA AUTORIZAÇÃO					
CONTRATANTE: BRK AMBIENTAL		CONTRATO Nº: --			
UNIDADE DA BRK: SUMARE S.A.		MUNICÍPIO/ESTADO: SUMARE /SP			
RESP. TÉCNICO: JEAN CARLOS ESSER		BARRIO/ÁREA: SEDE			
CREA: 076760-0/SC		LOCAL: --			
ASSINATURA:		DATA: --			
ART: --		ART: --			

TÍTULO: ESTAÇÃO DE TRATAMENTO DE ESGOTO TIJUCO PRETO					
CONTEÚDO: PROJETO EXECUTIVO ELÉTRICO ESTAÇÃO DE TRATAMENTO DE ESGOTO FLUXOGRAMA FASE LÍQUIDA					
PROJETO: RSD	APPROVAÇÃO: BRK AMBIENTAL	FORMATO: A1	ESCALA:	TOLHA:	REVISÃO: 04
DESENHO: RSD	APPROVAÇÃO: CLIENTE:	CODIGO:	HID-PE-DE-ETE-FLX-003		
VERIFICAÇÃO: JG					
APPROVAÇÃO: RSD					
HID-PE-DE-ETE-FLX-001 R05 - FASE LÍQUIDA_20260420.DWG					