



RUA HERMANN ALTHOFF Nº 255
BAIRRO ITROUPAVAZINHA
BLUMENAU/SC
FONE: 47 99253-7155
E-mail: vendas@hidryco.com.br

PCE NEREDA

CLIENTE: BRK AMBIENTAL
LOCAL: SUMARÉ-SP

☒ Aprovação

☐ Fabricação/Execução


☐ Conforme Fabricado




LEGENDA:					TÍTULO: PCE NEREDA		
					SUB-TÍTULO: Capa		
REVISÃO:	EI				UNID. BRK:	SUMARÉ	MUNIC./EST.: SUMARÉ-SP
DATA:	03/06/2025				BAIRRO/ÁREA:		
EXECUÇÃO:	Luiz Corrêa				RESP. TÉC.:	JEAN CARLOS ESSER	APROVAÇÃO BRK AMBIENTAL:
VERIFICAÇÃO:	Luiz Corrêa				CREA:	076760-0/SC	APROVAÇÃO CLIENTE: BRK
APROVAÇÃO:	Rafael Decker				CÓDIGO DO PROJETO:	HID-PA-DE-ETE-ELQ-005	
CONTRATANTE: BRK AMBIENTAL					ESCALA:	1:1	REVISÃO: EI
CONTRATO Nº: 230317					FORMATO: HID-PA-DE-ETE-ELQ-005.DWG		

	0	1	2	3	4	5	6	7				
A	Índice								A			
B		Página	Descrição da página			Campo suplementar de páginas		Data	Editor			
		1	Capa					14/12/2025	Luiz Corrêa			
		2	Índice					14/12/2025	Luiz Corrêa			
		2.a	Índice					14/12/2025	Luiz Corrêa			
C		3	legenda					14/12/2025	Luiz Corrêa			
		4	legenda					14/12/2025	Luiz Corrêa			
		5	ENTRADA ENERGIA					14/12/2025	Luiz Corrêa			
		6	ALIMENTAÇÃO INSTRUMENTOS 24Vcc					14/12/2025	Luiz Corrêa			
D		7	ALIMENTAÇÃO INSTRUMENTOS 220Vca					14/12/2025	Luiz Corrêa			
		8	ALIMENTAÇÃO INSTRUMENTOS 220Vca					14/12/2025	Luiz Corrêa			
		9	FONTE 24Vcc					14/12/2025	Luiz Corrêa			
		10	DIAGRAMA CLP					14/12/2025	Luiz Corrêa			
E		11	DIAGRAMA CLP					14/12/2025	Luiz Corrêa			
		12	Entradas Digitais					14/12/2025	Luiz Corrêa			
		13	Entradas Digitais					14/12/2025	Luiz Corrêa			
		14	Entradas Digitais					14/12/2025	Luiz Corrêa			
F		15	Entradas Digitais					14/12/2025	Luiz Corrêa			
		16	Entradas Digitais					14/12/2025	Luiz Corrêa			
		17	Entradas Digitais					14/12/2025	Luiz Corrêa			
		18	Entradas Digitais					14/12/2025	Luiz Corrêa			
G		19	Entradas Digitais					14/12/2025	Luiz Corrêa			
		20	Entradas Digitais					14/12/2025	Luiz Corrêa			
		21	Entradas Digitais					14/12/2025	Luiz Corrêa			
		22	Entradas Digitais					14/12/2025	Luiz Corrêa			
H		23	Entradas Digitais					14/12/2025	Luiz Corrêa			
		24	Entradas Digitais					14/12/2025	Luiz Corrêa			
		25	Entradas Digitais					14/12/2025	Luiz Corrêa			
		26	Entradas Digitais					14/12/2025	Luiz Corrêa			
		27	Entradas Digitais					14/12/2025	Luiz Corrêa			
		28	Saídas Digitais					14/12/2025	Luiz Corrêa			
	0	1	2	3	4	5	6	7				
FOLHA: 2 / 58			LEGENDA:				TÍTULO:					
							PCE NEREDA					
							SUB-TÍTULO:					
			Índice									
			REVISÃO:	EI						UNID. BRK:	MUNIC./EST.:	BAIRRO/ÁREA:
			DATA:	03/06/2025						SUMARÉ	SUMARÉ-SP	
EXECUÇÃO:	Luiz Corrêa				RESP. TÉC.: JEAN CARLOS ESSER	APROVAÇÃO BRK AMBIENTAL:	APROVAÇÃO CLIENTE:					
VERIFICAÇÃO:	Luiz Corrêa				CREA: 076760-0/SC		BRK					
APROVAÇÃO:	Rafael Decker				CONTRATANTE: BRK AMBIENTAL	CONTRATO Nº: 230317	CÓDIGO DO PROJETO: HID-PA-DE-ETE-ELQ-005	ESCALA: 1:1	REVISÃO: EI			
FORMATO: HID-PA-DE-ETE-ELQ-005.DWG												

	0	1	2	3	4	5	6	7		
A		BORNE DE PASSAGEM		TOMADA FÊMEA 5 PONTOS DE CONEXÃO		CHAVE SECCIONADORA PARA FUSÍVEL		COMUTADOR 2 POSIÇÕES COM CHAVE CONTATO "NA" / "NF"		PROTETOR DE SURTO DPS
B		BORNE FUSÍVEL SECCIONÁVEL		BOBINA 24VCC OU 220VCA		DISJUNTOR TÉRMICO/MAGNÉTICO PARA MOTOR		CONTATO "NA" / NF MONTAGEM MODULAR		BUZINA / CORNETA SINALIZAÇÃO SONORA
C		BORNE FUSÍVEL SECCIONÁVEL C/ INDICAÇÃO POR LED		BOBINA BIVOLT 110VCA/220VCA		RELÉ DE PROTEÇÃO TÉRMICA		CONTATO RETROATIVO PRESSOSTATO		SIRENE / BUZER SINALIZAÇÃO SONORA
D		CONECTOR FÊMEA		CONTATO TRANSISTOR NPN		INTERRUPTOR DIFERENCIAL RESIDUAL "DR"		TRANSFORMADOR DE CORRENTE		MOTOR MONOFÁSICO COM PE
E		CONECTOR MACHO		CONTATO TRANSISTOR PNP		DISJUNTOR MONOFÁSICO		COMUTADOR 3 POSIÇÕES COM TRAVA		COMUTADOR 2 POSIÇÕES CONTATO "NA" / "NF"
F		TOMADA FÊMEA 3 PONTOS DE CONEXÃO		CONTATO "NA" COMANDO		DISJUNTOR BIFÁSICO		FIM DE CURSO MECÂNICO CONTATO "NA" / "NF"		MOTOR TRIFÁSICO COM PE
G		TOMADA FÊMEA 4 PONTOS DE CONEXÃO		CONTATO "NA" POTÊNCIA		DISJUNTOR TRIFÁSICO		TERMOPAR		SIRENE / BUZER SINALIZAÇÃO SONORA
H		CONTATO "NA" LINHA DE ATUAÇÃO		SENSOR NTC / PTC		DISJUNTOR POLIFÁSICO		SENSOR NTC / PTC		VÁLVULA SOLENÓIDE
I		CONTATO "NF" COMANDO		BATERIA		CONTATO "NA" / "NF" PRESSOSTATO		BATERIA		SINALEIRO
J		CONTATO "NF" POTENCIA		TRANSFORMADOR		CONTATO "NA" / "NF" RETROATIVO BÓIA		TRANSFORMADOR		CONTATO "NA" / "NF" TEMPERATURA
K		CONTATO "NF" LINHA DE ATUAÇÃO		BOTÃO DE EMERGÊNCIA "NA" / "NF" SOCO/ GIRA		FONTE AUXILIAR AC / DC		FONTE AUXILIAR AC / DC		BOTÃO DE PULSO "NA" / "NF"

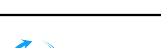0		1		2		3		4		5		6		7			
FOLHA: 3 / 58				LEGENDA:						TÍTULO: PCE NEREDA							
										SUB-TÍTULO: legenda							
				REVISÃO:		EI						UNID. BRK: SUMARÉ		MUNIC./EST.: SUMARÉ-SP		BAIRRO/ÁREA:	
				DATA:		03/06/2025						RESP. TÉC.: JEAN CARLOS ESSER 076760-0/SC		APROVAÇÃO BRK AMBIENTAL:		APROVAÇÃO CLIENTE: BRK	
				EXECUÇÃO:		Luiz Corrêa						CREA:					
		VERIFICAÇÃO:		Luiz Corrêa				CONTRATANTE: BRK AMBIENTAL		CONTRATO Nº: 230317		CÓDIGO DO PROJETO: HID-PA-DE-ETE-ELQ-005		ESCALA: 1:1		REVISÃO: EI	
		APROVAÇÃO:		Rafael Decker													

	0	1	2	3	4	5	6	7
A	1- CARACTERISTICAS ELÉTRICAS			4- FIAÇÃO DE COMANDO			7- PINTURA	
	1.1- TENSÃO NOM. DE OPERAÇÃO(Ue): 1.2- TENSÃO NOM. DE CONTROLE: 1.3- TENSÃO NOM. DE SERVIÇOS AUXILIARES: 1.4- TENSÃO NOM. DE ISOLAMENTO (Ui) 1.5- FREQUENCIA:			4.1- CLASSE ISOLAÇÃO: 4.2- CLASSE TEMPERATURA: 4.3- ISOLAÇÃO: 4.4- CORES / SEÇÃO MÍNIMA:			7.1- CLASSE ISOLAÇÃO:	
	2- BARRAMENTOS			4.5- ANILHAMENTO:			7.2- ACABAMENTO EXTERNO:	
B	OBS: CORRENTE CURTO-CIRCUITO: 10kA FORMA DE SEPARAÇÃO: 1			5- AMBIENTE			7.3- ACABAMENTO INTERNO:	
C	2.1- TEMPERATURA MÁXIMA DO AR AO REDOR DO BARRAMENTO: 2.2- TEMPERATURA MÁXIMA DA SUPERFÍCIE DO BARAMENTO: 2.3- MATERIAL: 2.4- TRATAMENTO: 2.5- CONEXÕES: 2.6- CORES:			6- CARACTERISTICAS MECÂNICAS			7.4- ACABAMENTO DA CHAPA DE MONTAGEM	
D	2.6.1- CIRCUITO CA - FASE (R): 2.6.2- CIRCUITO CA - FASE (S): 2.6.3- CIRCUITO CA - FASE (T): 2.6.4- TERRA (PE): 2.6.5- NEUTRO (N): 2.6.6- PROTEÇÃO + NEUTRO (PEN): 2.6.7- BITOLA DO BARRAMENTO GERAL			7- REQUISITOS DE OPERAÇÃO (ATIVIDADE CRÍTICA) :			7.5- ACABAMENTO DA SOLEIRA:	
E	OBS: EM CASO DA NÃO INDENTIFICAÇÃO DAS CORES ATRAVÉS DE PINTURA, OS BARRAMENTOS SERÃO INDENTIFICADOS COM FITA DA COR CORRESPONDENTE			8- REQUISITOS DE OPERAÇÃO (ATIVIDADE CRÍTICA) :			7.6- ESPESSURA DA FINAL DA CAMADA	
F	3- FIAÇÃO DE FORÇA			9- ARMAZENAMENTO, EMBALAGEM PRESERVAÇÃO E GARANTIA:			8.1- PARA INSTALAÇÃO E OPERAÇÃO LEVAR EM CONSIDERAÇÃO ESTA FOLHA DE NOTAS	
G	3.1- CLASSE DE ISOLAÇÃO: 3.2- CLASSE TEMPERATURA: 3.3- ISOLAÇÃO: 3.4- CORES / SEÇÃO MÍNIMA:			6.1- SEPARAÇÃO INTERNA DO CONJUNTO CONFORME APROVAÇÃO DO CLIENTE			8.2- QUANDO O PAINEL FOR IÇADO, UTILIZAR OS DISPOZITIVOS DE IÇAMNETO DE FORMA QUE O PESO DO PRODUTO FIQUE DISTRIBUIDO DE FORMA HOMOGÊNEA	
H	3.5- ANILHAMENTO:			6.2- INSTALAÇÃO:			8.3- NÃO MANOBRAR AS CHAVES SECCIONADORAS COM GARGA	
	FIO IDENTIFICADO EM SUAS EXTREMIDADES COM O NÚMERO DO CABO, RESPEITANDO OS DOIS PRIMEIROS DÍGITOS O NÚMERO DE PÁGINA + CONTADOR			6.3- GRAU DE PROTEÇÃO:			9.1- O PAINEL DEVERÁ SER TRANSPORTADO, ACONDICIONADO E ARMAZENADO CONFORME A MARCAÇÃO DA EMBALAGEM (SÍMBOLOS DE MANUSEIO) FIXADA NO PRODUTO OU NA EMBALAGEM:	
	FIO IDENTIFICADO EM SUAS EXTREMIDADES COM O NÚMERO DO CABO, RESPEITANDO OS DOIS PRIMEIROS DÍGITOS O NÚMERO DE PÁGINA + CONTADOR			6.4- OPERAÇÃO DO PAINEL:			FACE SUPERIOR NESTA DIREÇÃO	
	FIO IDENTIFICADO EM SUAS EXTREMIDADES COM O NÚMERO DO CABO, RESPEITANDO OS DOIS PRIMEIROS DÍGITOS O NÚMERO DE PÁGINA + CONTADOR			6.5- MANUTENÇÃO DO PAINEL:			FRÁGIL	
	FIO IDENTIFICADO EM SUAS EXTREMIDADES COM O NÚMERO DO CABO, RESPEITANDO OS DOIS PRIMEIROS DÍGITOS O NÚMERO DE PÁGINA + CONTADOR			6.6- ENTRADA DOS CABOS:			PROTEGER CONTRA A UMIDADE	
	FIO IDENTIFICADO EM SUAS EXTREMIDADES COM O NÚMERO DO CABO, RESPEITANDO OS DOIS PRIMEIROS DÍGITOS O NÚMERO DE PÁGINA + CONTADOR			6.7- SAÍDA DOS CABOS:			9.2- TODO PRODUTO É ENTREGUE COM CERTIFICADO DE GARANTIA	
	FIO IDENTIFICADO EM SUAS EXTREMIDADES COM O NÚMERO DO CABO, RESPEITANDO OS DOIS PRIMEIROS DÍGITOS O NÚMERO DE PÁGINA + CONTADOR			6.8- SUPORTAÇÃO:			9.3- PESO APROXIMADO DO PAINEL (CONJUNTO):	
	FIO IDENTIFICADO EM SUAS EXTREMIDADES COM O NÚMERO DO CABO, RESPEITANDO OS DOIS PRIMEIROS DÍGITOS O NÚMERO DE PÁGINA + CONTADOR			6.9- ESTRUTURA DO PAINEL EM:				
	FIO IDENTIFICADO EM SUAS EXTREMIDADES COM O NÚMERO DO CABO, RESPEITANDO OS DOIS PRIMEIROS DÍGITOS O NÚMERO DE PÁGINA + CONTADOR			6.10- BILOTA DAS CHAPAS EM (mm):				
	FIO IDENTIFICADO EM SUAS EXTREMIDADES COM O NÚMERO DO CABO, RESPEITANDO OS DOIS PRIMEIROS DÍGITOS O NÚMERO DE PÁGINA + CONTADOR			6.10.1- ESTRUTURA				
	FIO IDENTIFICADO EM SUAS EXTREMIDADES COM O NÚMERO DO CABO, RESPEITANDO OS DOIS PRIMEIROS DÍGITOS O NÚMERO DE PÁGINA + CONTADOR			6.10.2- BASE SOLEIRA				
	FIO IDENTIFICADO EM SUAS EXTREMIDADES COM O NÚMERO DO CABO, RESPEITANDO OS DOIS PRIMEIROS DÍGITOS O NÚMERO DE PÁGINA + CONTADOR			6.10.3- PLACA MONTAGEM				
	FIO IDENTIFICADO EM SUAS EXTREMIDADES COM O NÚMERO DO CABO, RESPEITANDO OS DOIS PRIMEIROS DÍGITOS O NÚMERO DE PÁGINA + CONTADOR			6.10.4- PORTAS				
	FIO IDENTIFICADO EM SUAS EXTREMIDADES COM O NÚMERO DO CABO, RESPEITANDO OS DOIS PRIMEIROS DÍGITOS O NÚMERO DE PÁGINA + CONTADOR			6.10.5- TAMPAS				
	FIO IDENTIFICADO EM SUAS EXTREMIDADES COM O NÚMERO DO CABO, RESPEITANDO OS DOIS PRIMEIROS DÍGITOS O NÚMERO DE PÁGINA + CONTADOR			6.10.6- FLANGES				
	FIO IDENTIFICADO EM SUAS EXTREMIDADES COM O NÚMERO DO CABO, RESPEITANDO OS DOIS PRIMEIROS DÍGITOS O NÚMERO DE PÁGINA + CONTADOR			6.10.7- TELHADO				
	FIO IDENTIFICADO EM SUAS EXTREMIDADES COM O NÚMERO DO CABO, RESPEITANDO OS DOIS PRIMEIROS DÍGITOS O NÚMERO DE PÁGINA + CONTADOR			OBS: 1,25mm = 18USG; 1,90mm = 14USG; 2,65mm= 12USG				
	FIO IDENTIFICADO EM SUAS EXTREMIDADES COM O NÚMERO DO CABO, RESPEITANDO OS DOIS PRIMEIROS DÍGITOS O NÚMERO DE PÁGINA + CONTADOR			FIO IDENTIFICADO EM SUAS EXTREMIDADES COM O NÚMERO DO CABO, RESPEITANDO OS DOIS PRIMEIROS DÍGITOS O NÚMERO DE PÁGINA + CONTADOR				
	FIO IDENTIFICADO EM SUAS EXTREMIDADES COM O NÚMERO DO CABO, RESPEITANDO OS DOIS PRIMEIROS DÍGITOS O NÚMERO DE PÁGINA +							

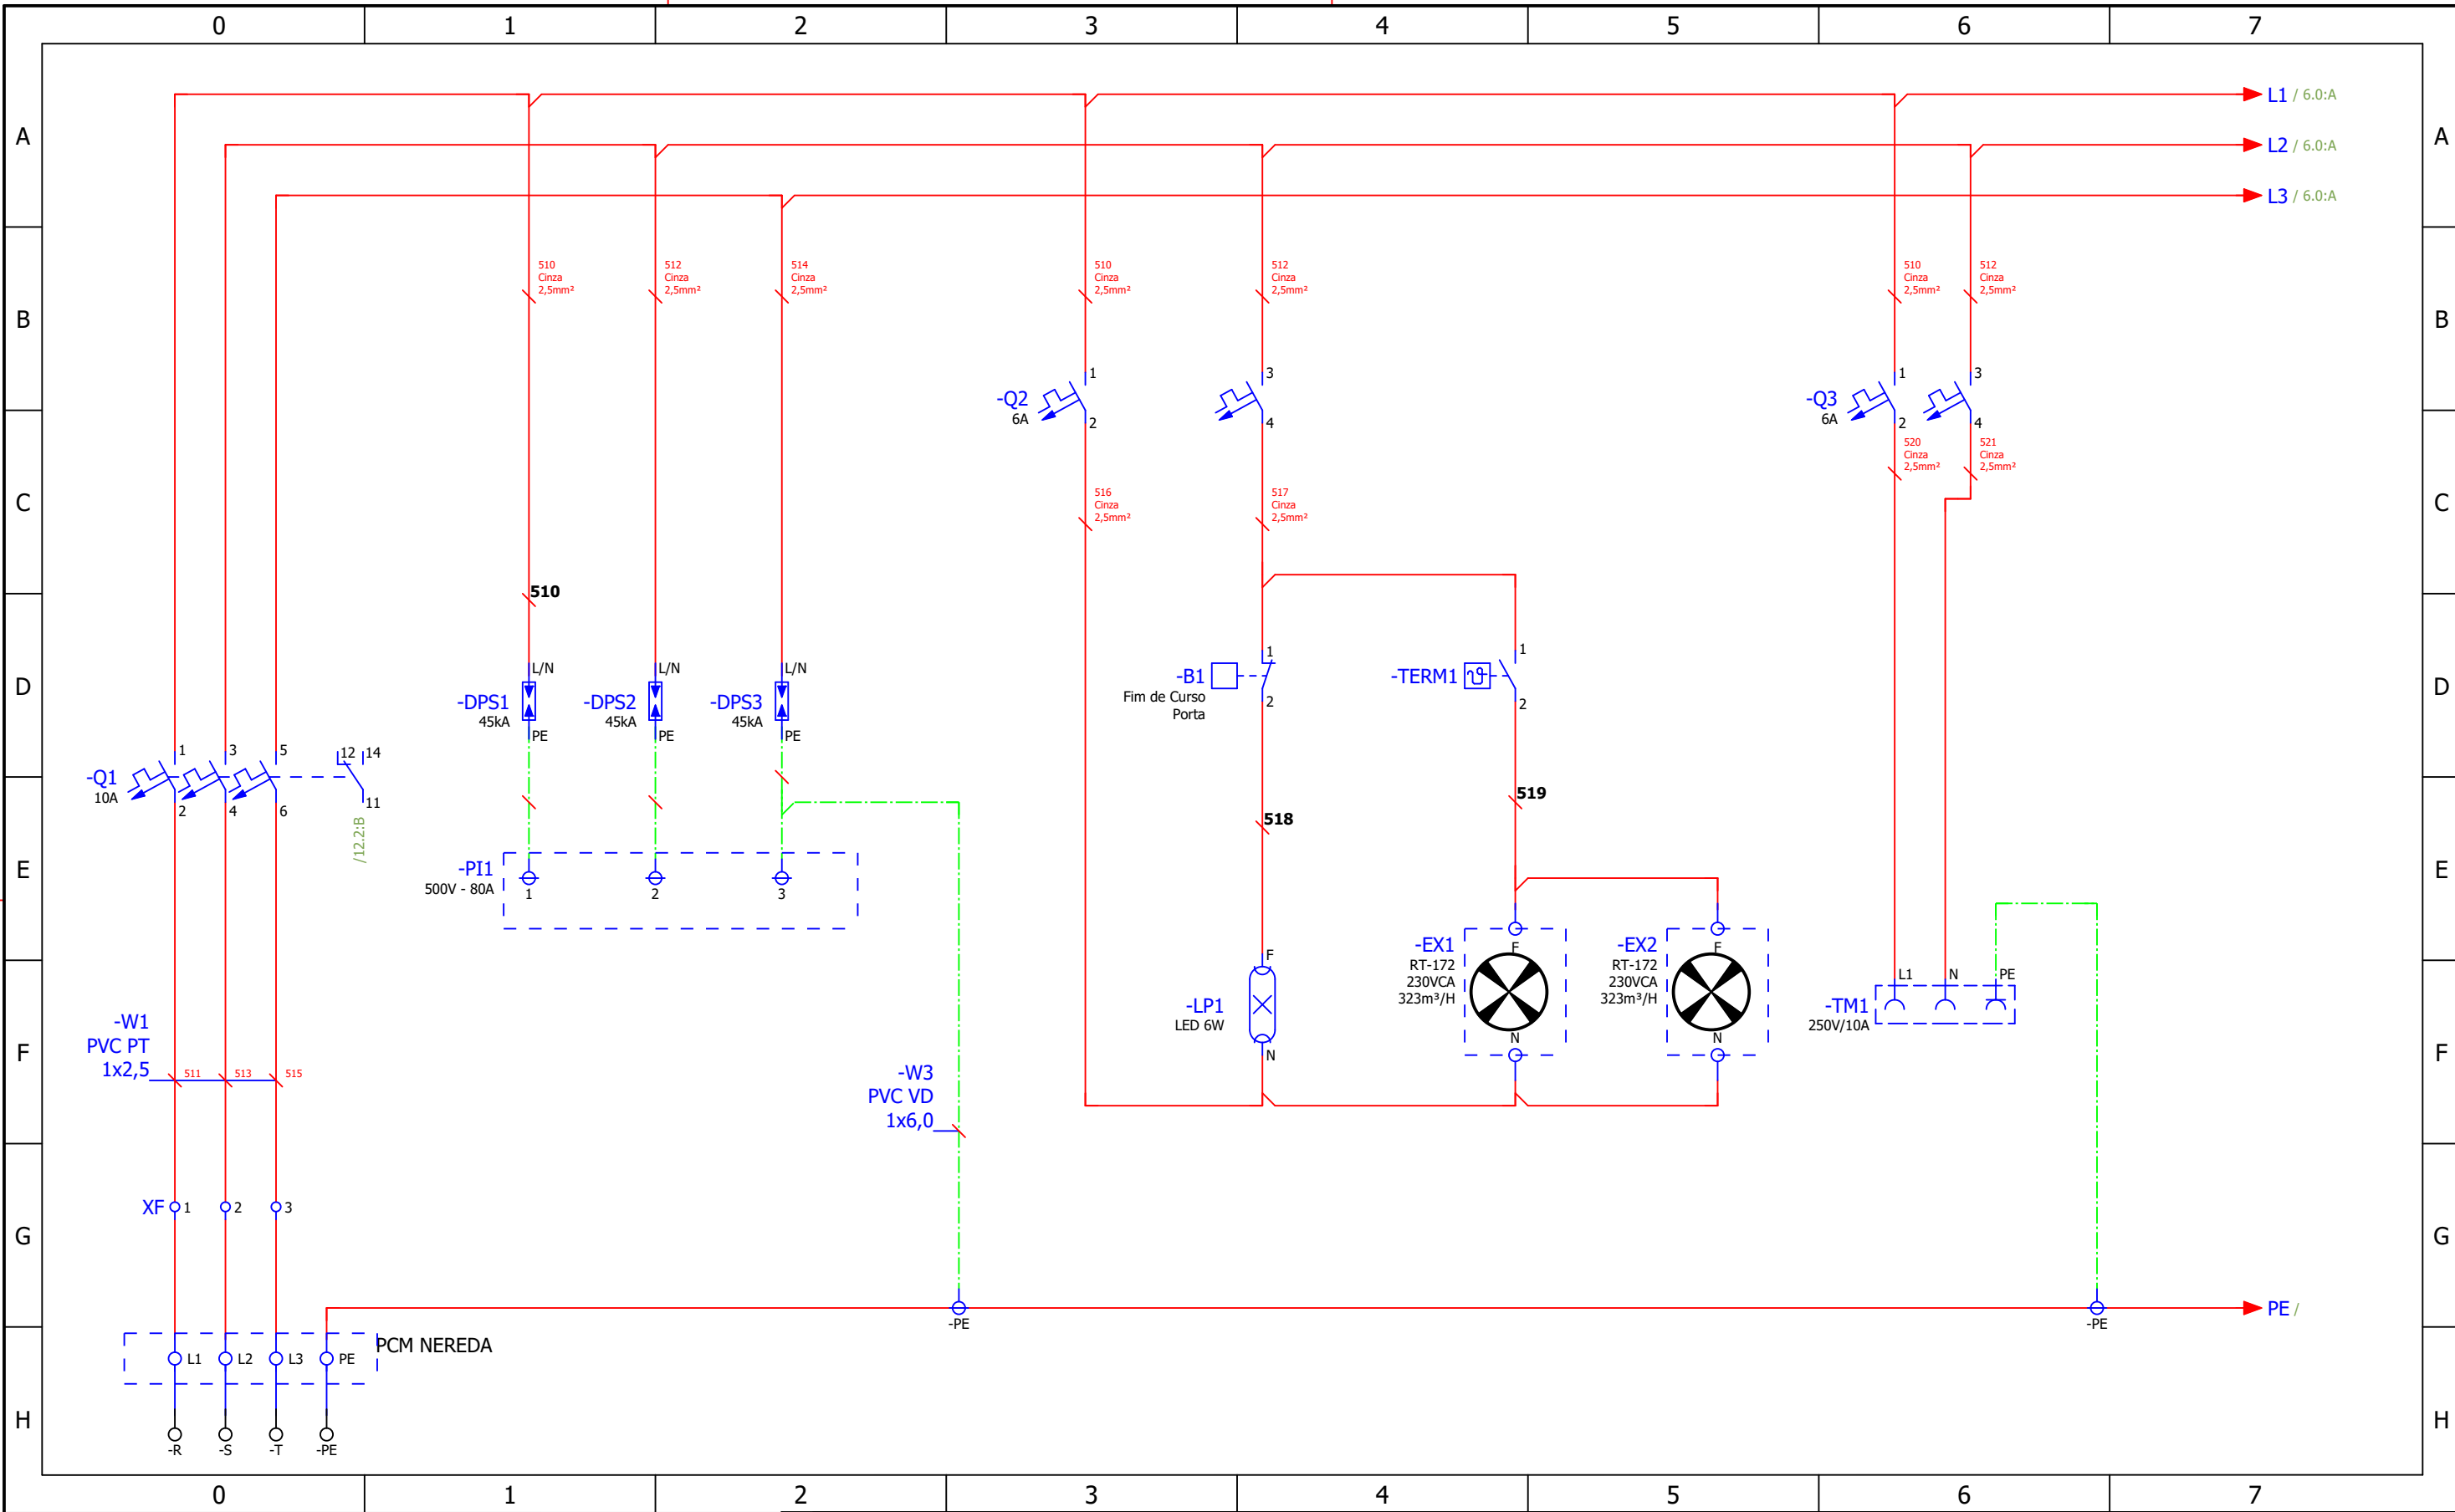

LEGENDA:				
REVISÃO:	EI			
DATA:	03/06/2025			
EXECUÇÃO:	Luiz Corrêa			
VERIFICAÇÃO:	Luiz Corrêa			
APROVAÇÃO:	Rafael Decker			

BRK




CONTRATANTE: BRK AMBIENTAL
CONTRATO Nº: 230317


TÍTULO:		
PCE NEREDA		
SUB-TÍTULO:		
ENTRADA ENERGIA		
UNID. BRK:	MUNIC./EST.:	BAIRRO/ÁREA:
SUMARÉ	SUMARÉ-SP	
RESP. TÊC.: JEAN CARLOS ESSER	APROVAÇÃO BRK AMBIENTAL:	APROVAÇÃO CLIENTE:
076760-0/SC		BRK
CÓDIGO DO PROJETO:	ESCALA:	REVISÃO:
HID-PA-DE-ETE-ELQ-005	1:1	EI


FORMATO:


HID-PA-DE-ETE-ELQ-005.DWG

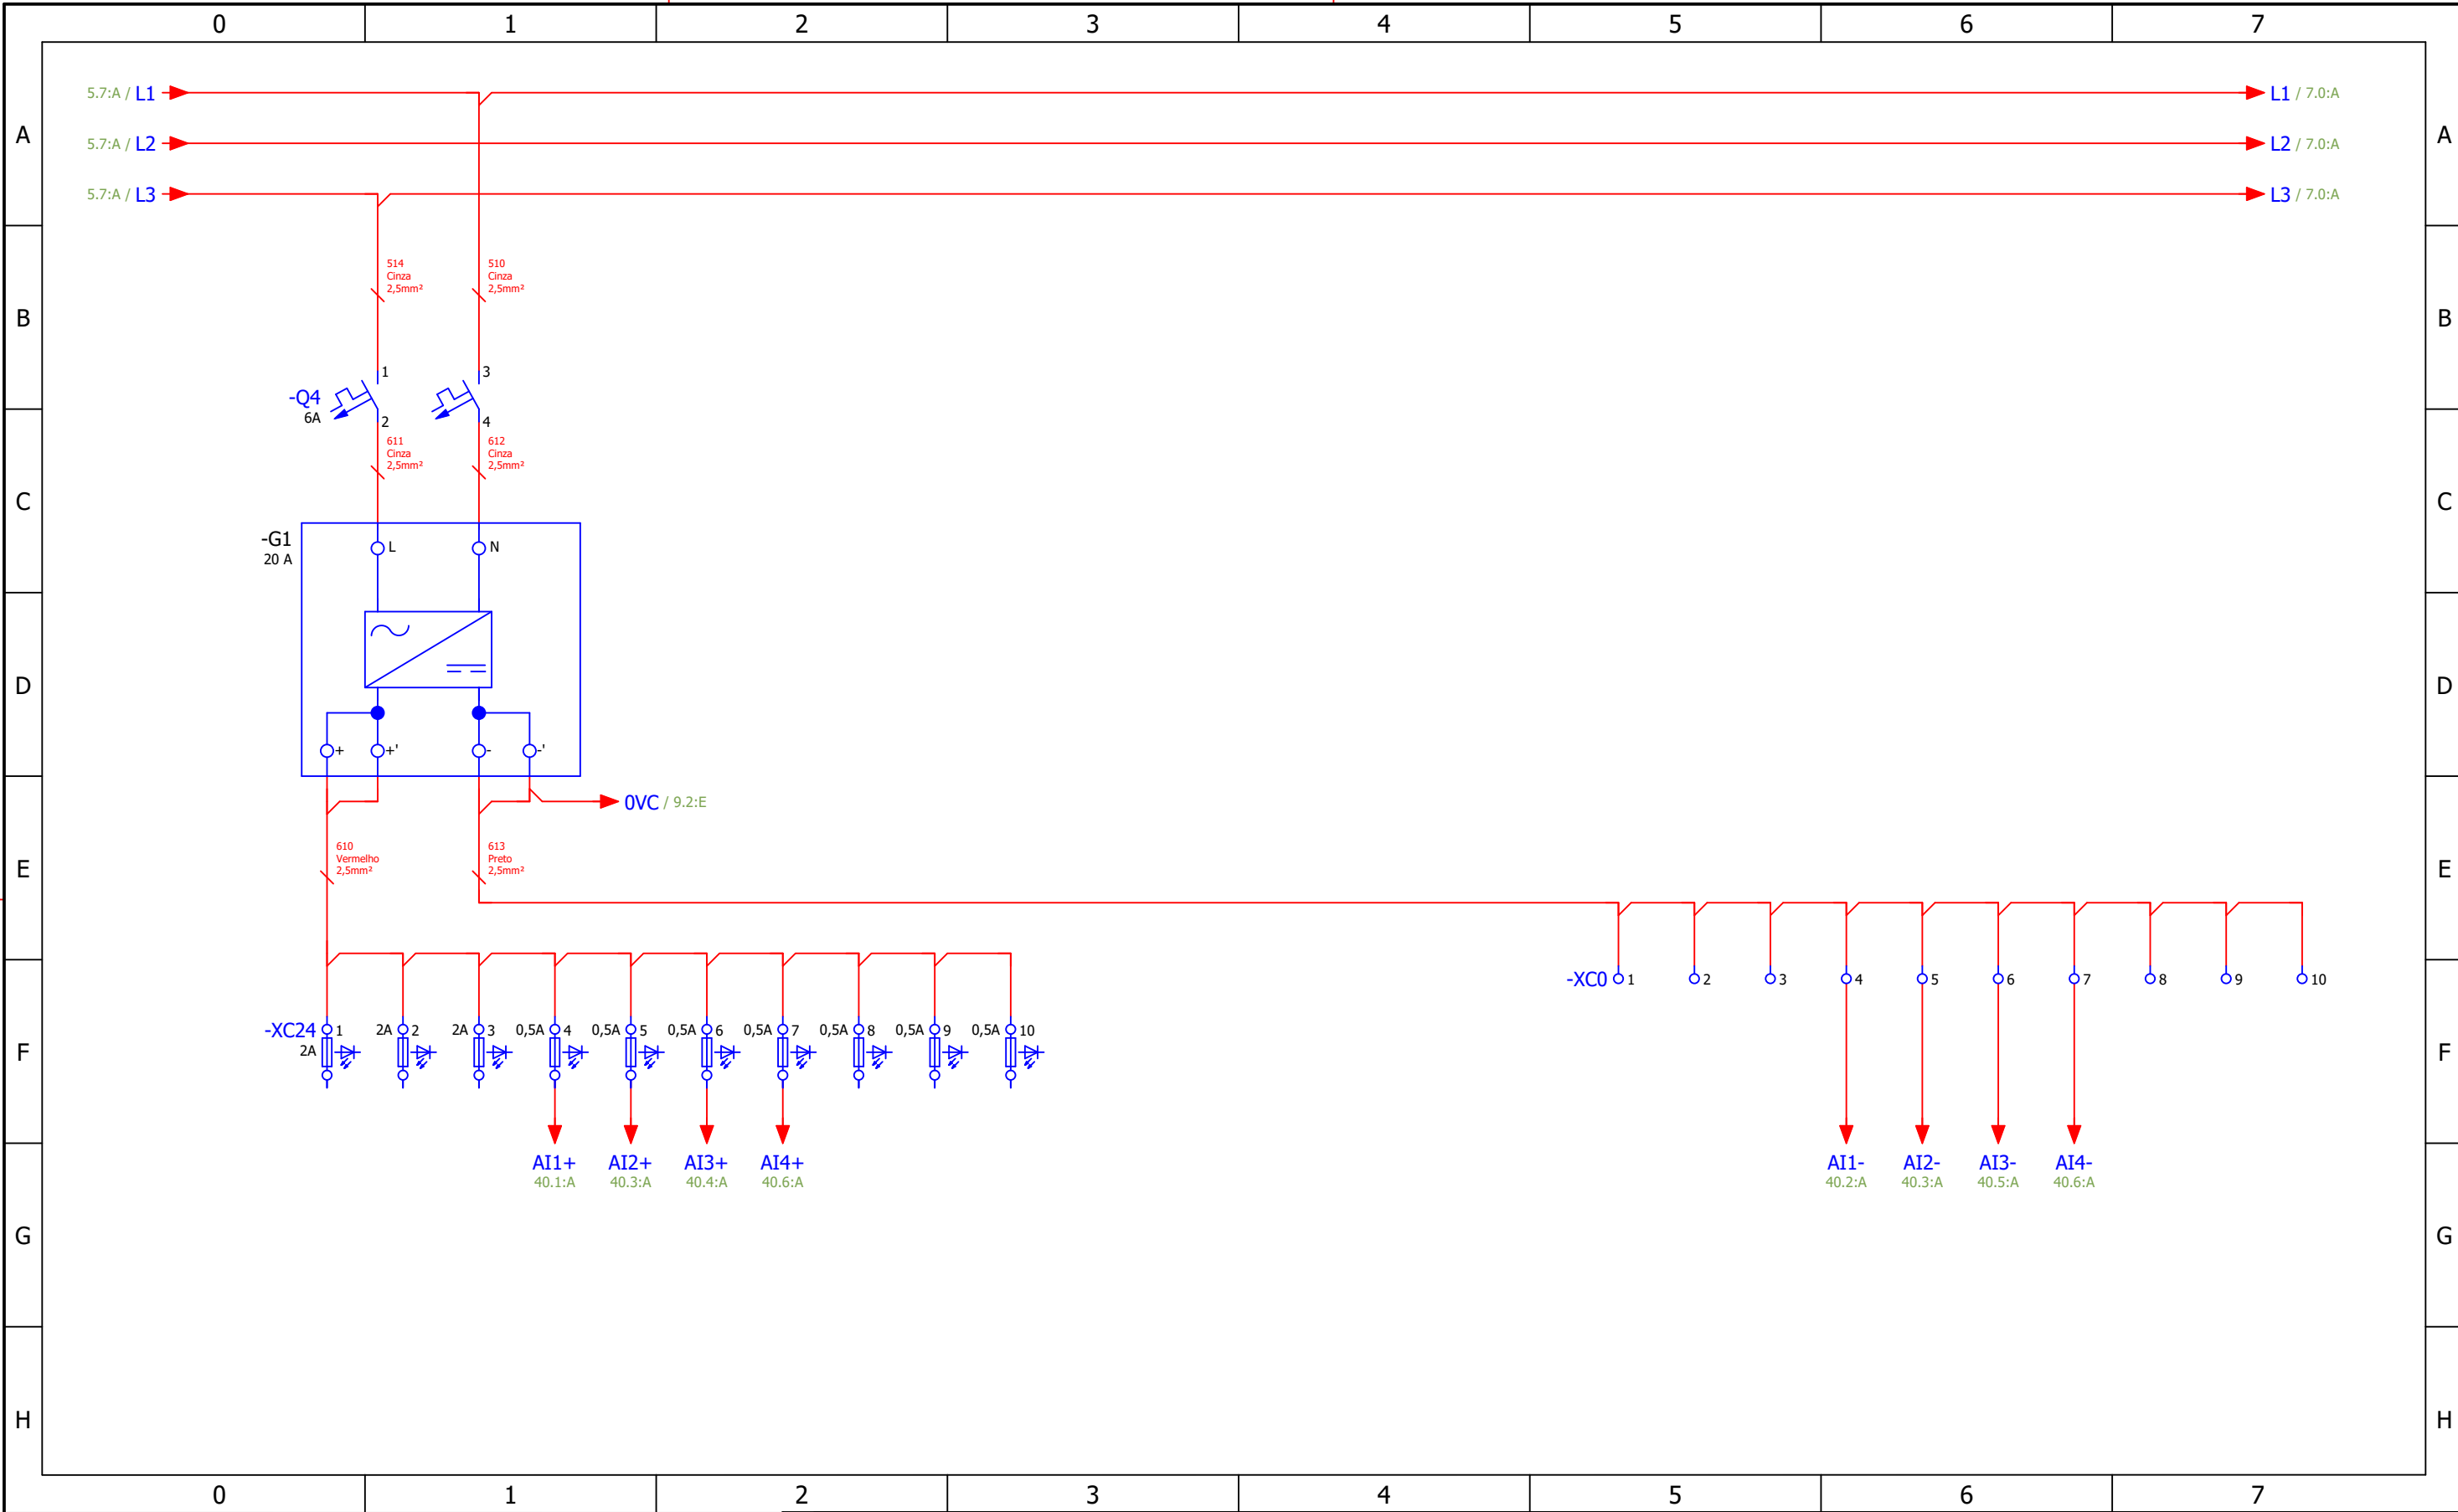



	FOLHA: 6 / 58	LEGENDA:						TÍTULO: PCE NEREDA				
								SUB-TÍTULO: ALIMENTAÇÃO INSTRUMENTOS 24Vcc				
		REVISÃO:	EI					UNID. BRK:	SUMARÉ	MUNIC./EST.:	SUMARÉ-SP	BAIRRO/ÁREA:
		DATA:	03/06/2025					RESP. TÊC.:	JEAN CARLOS ESSER	APROVAÇÃO BRK AMBIENTAL:		APROVAÇÃO CLIENTE:
		EXECUÇÃO:	Luiz Corrêa					CREA:	076760-0/SC			BRK
		VERIFICAÇÃO:	Luiz Corrêa					CÓDIGO DO PROJETO:			ESCALA:	REVISÃO:
		APROVAÇÃO:	Rafael Decker				CONTRATANTE:	CONTRATO Nº:	HID-PA-DE-ETE-ELQ-005			1:1
					BRK AMBIENTAL	230317						

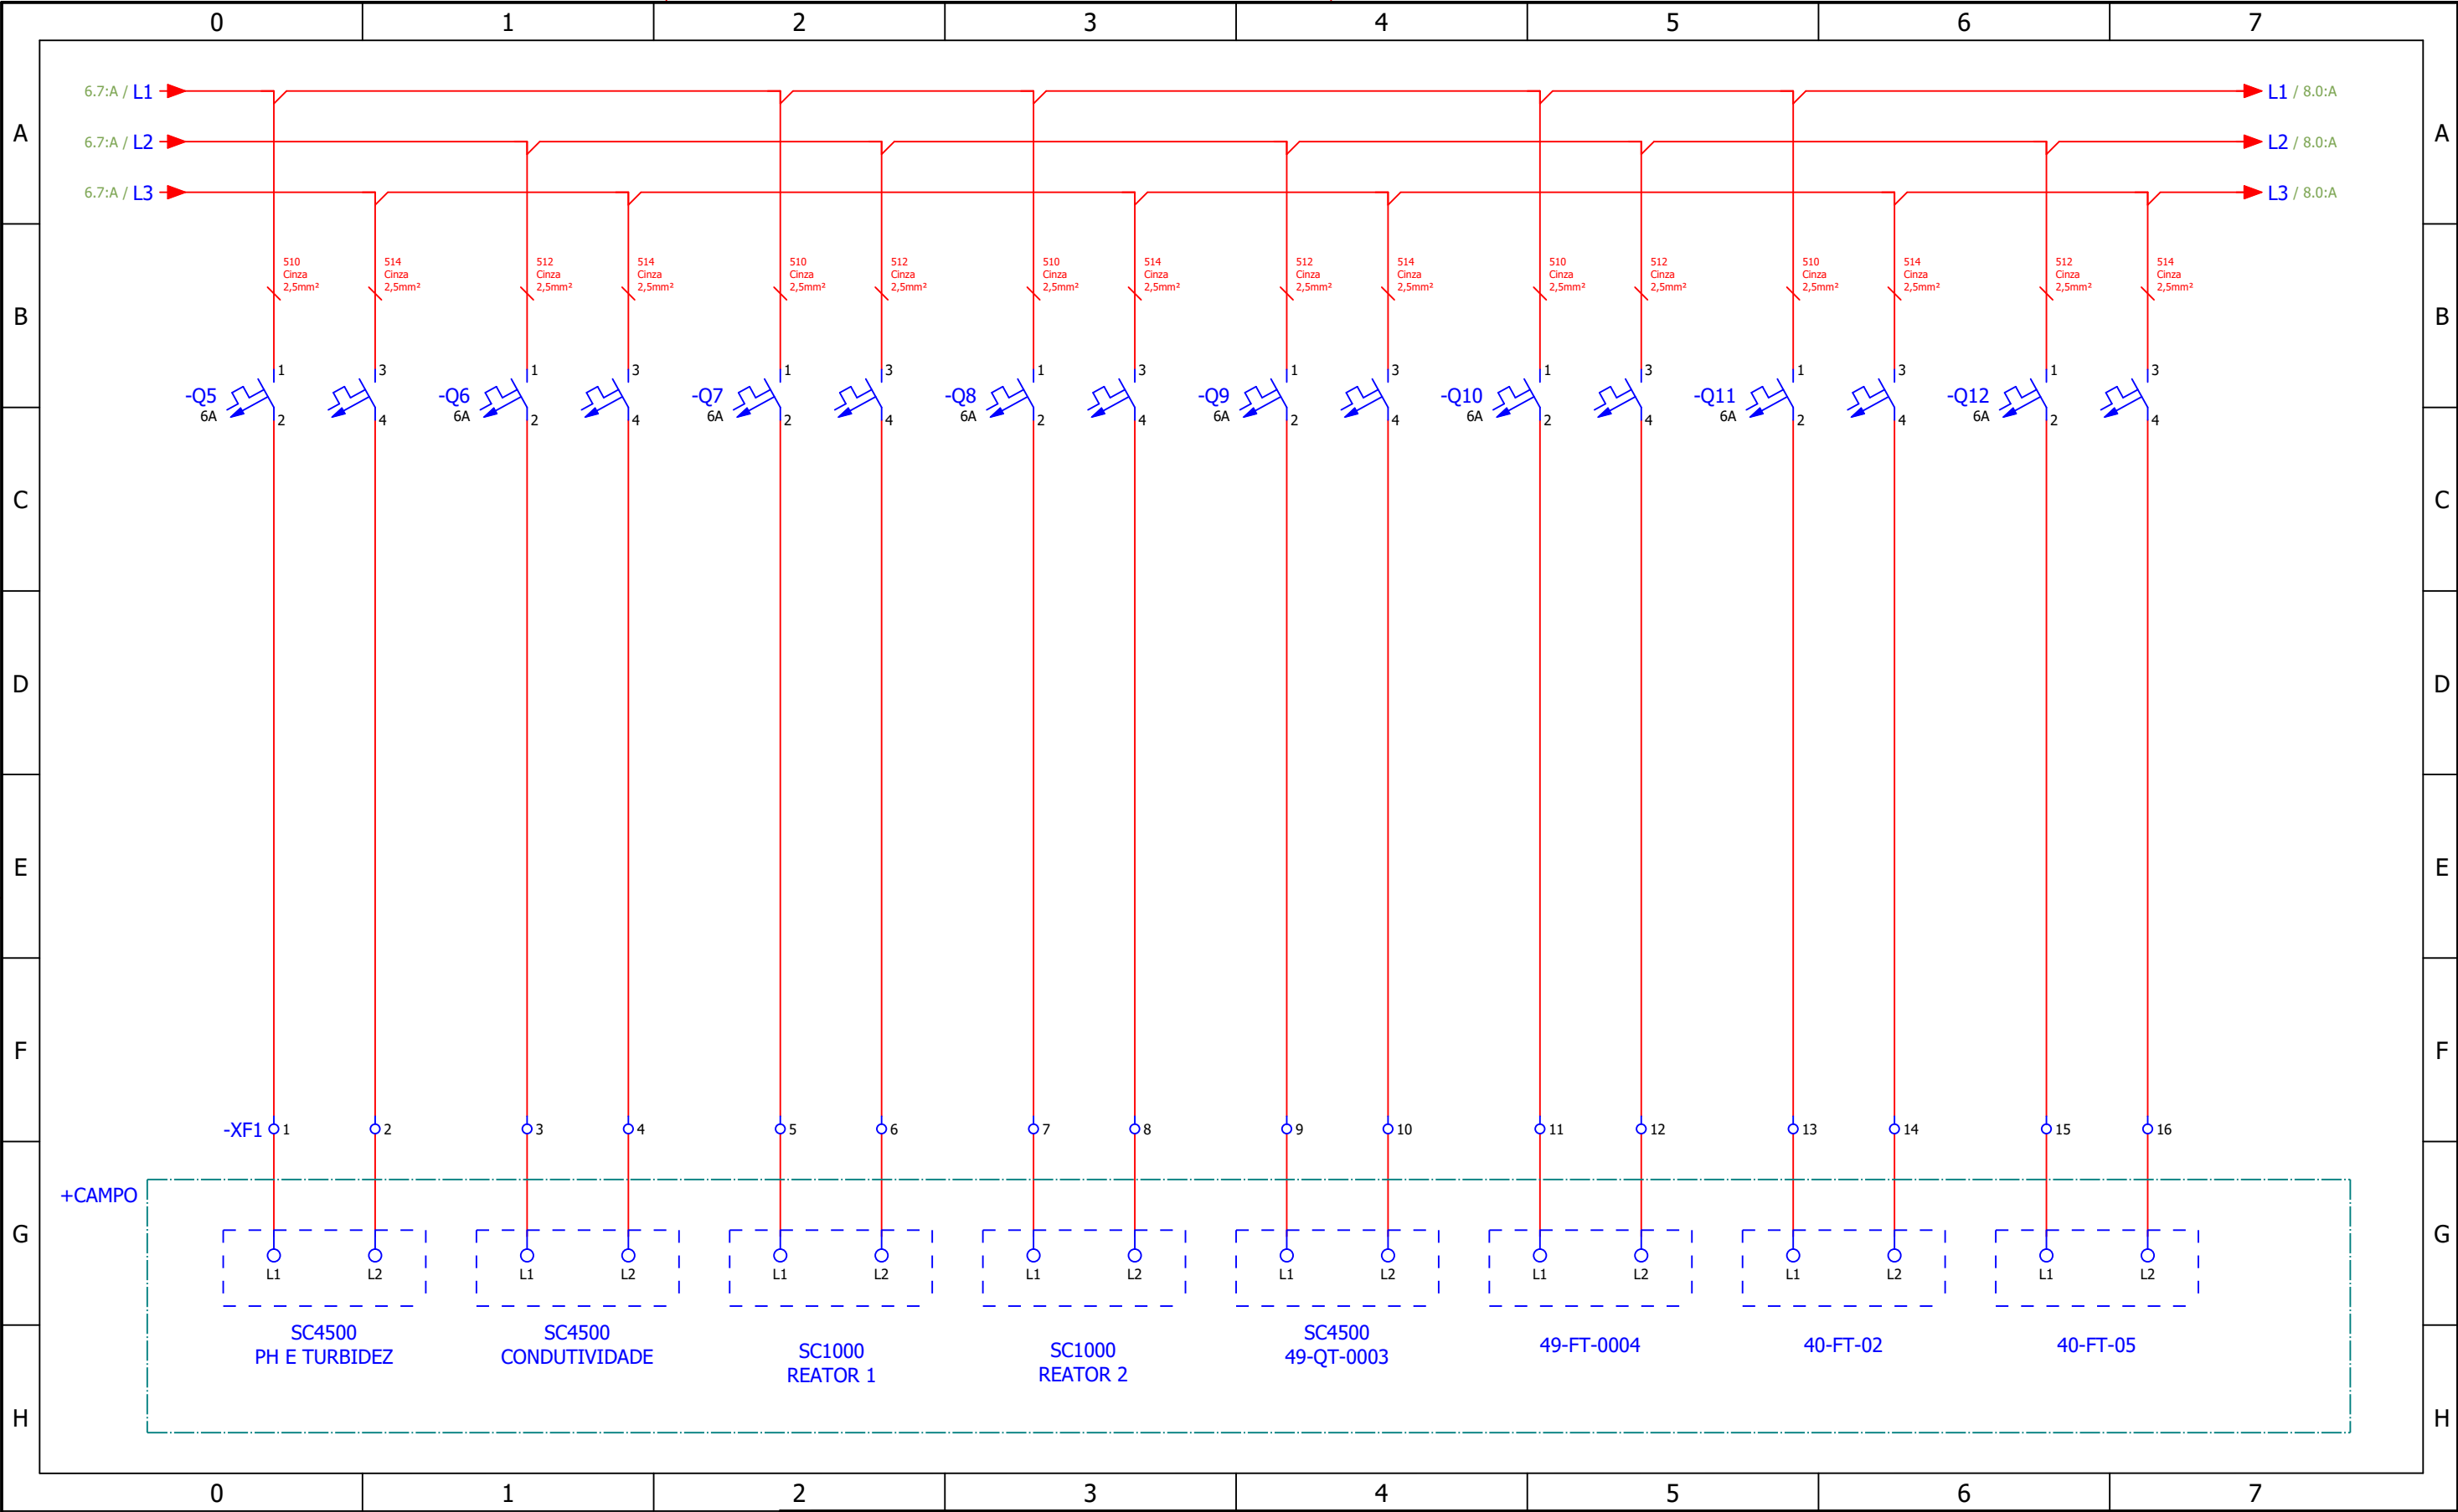

 FOLHA: 7 / 58	LEGENDA:						TÍTULO: PCE NEREDA			
							SUB-TÍTULO: ALIMENTAÇÃO INSTRUMENTOS 220Vca			
	REVISÃO:	EI						UNID. BRK: SUMARÉ	MUNIC./EST.: SUMARÉ-SP	BAIRRO/ÁREA:
	DATA:	03/06/2025						RESP. TÉC.: JEAN CARLOS ESSER 076760-0/SC	APROVAÇÃO BRK AMBIENTAL:	APROVAÇÃO CLIENTE: BRK
	EXECUÇÃO:	Luiz Corrêa				CÓDIGO DO PROJETO: HID-PA-DE-ETE-ELQ-005			ESCALA: 1:1	REVISÃO: EI
	VERIFICAÇÃO:	Luiz Corrêa				CONTRATANTE: BRK AMBIENTAL	CONTRATO Nº: 230317			
APROVAÇÃO:		Rafael Decker								

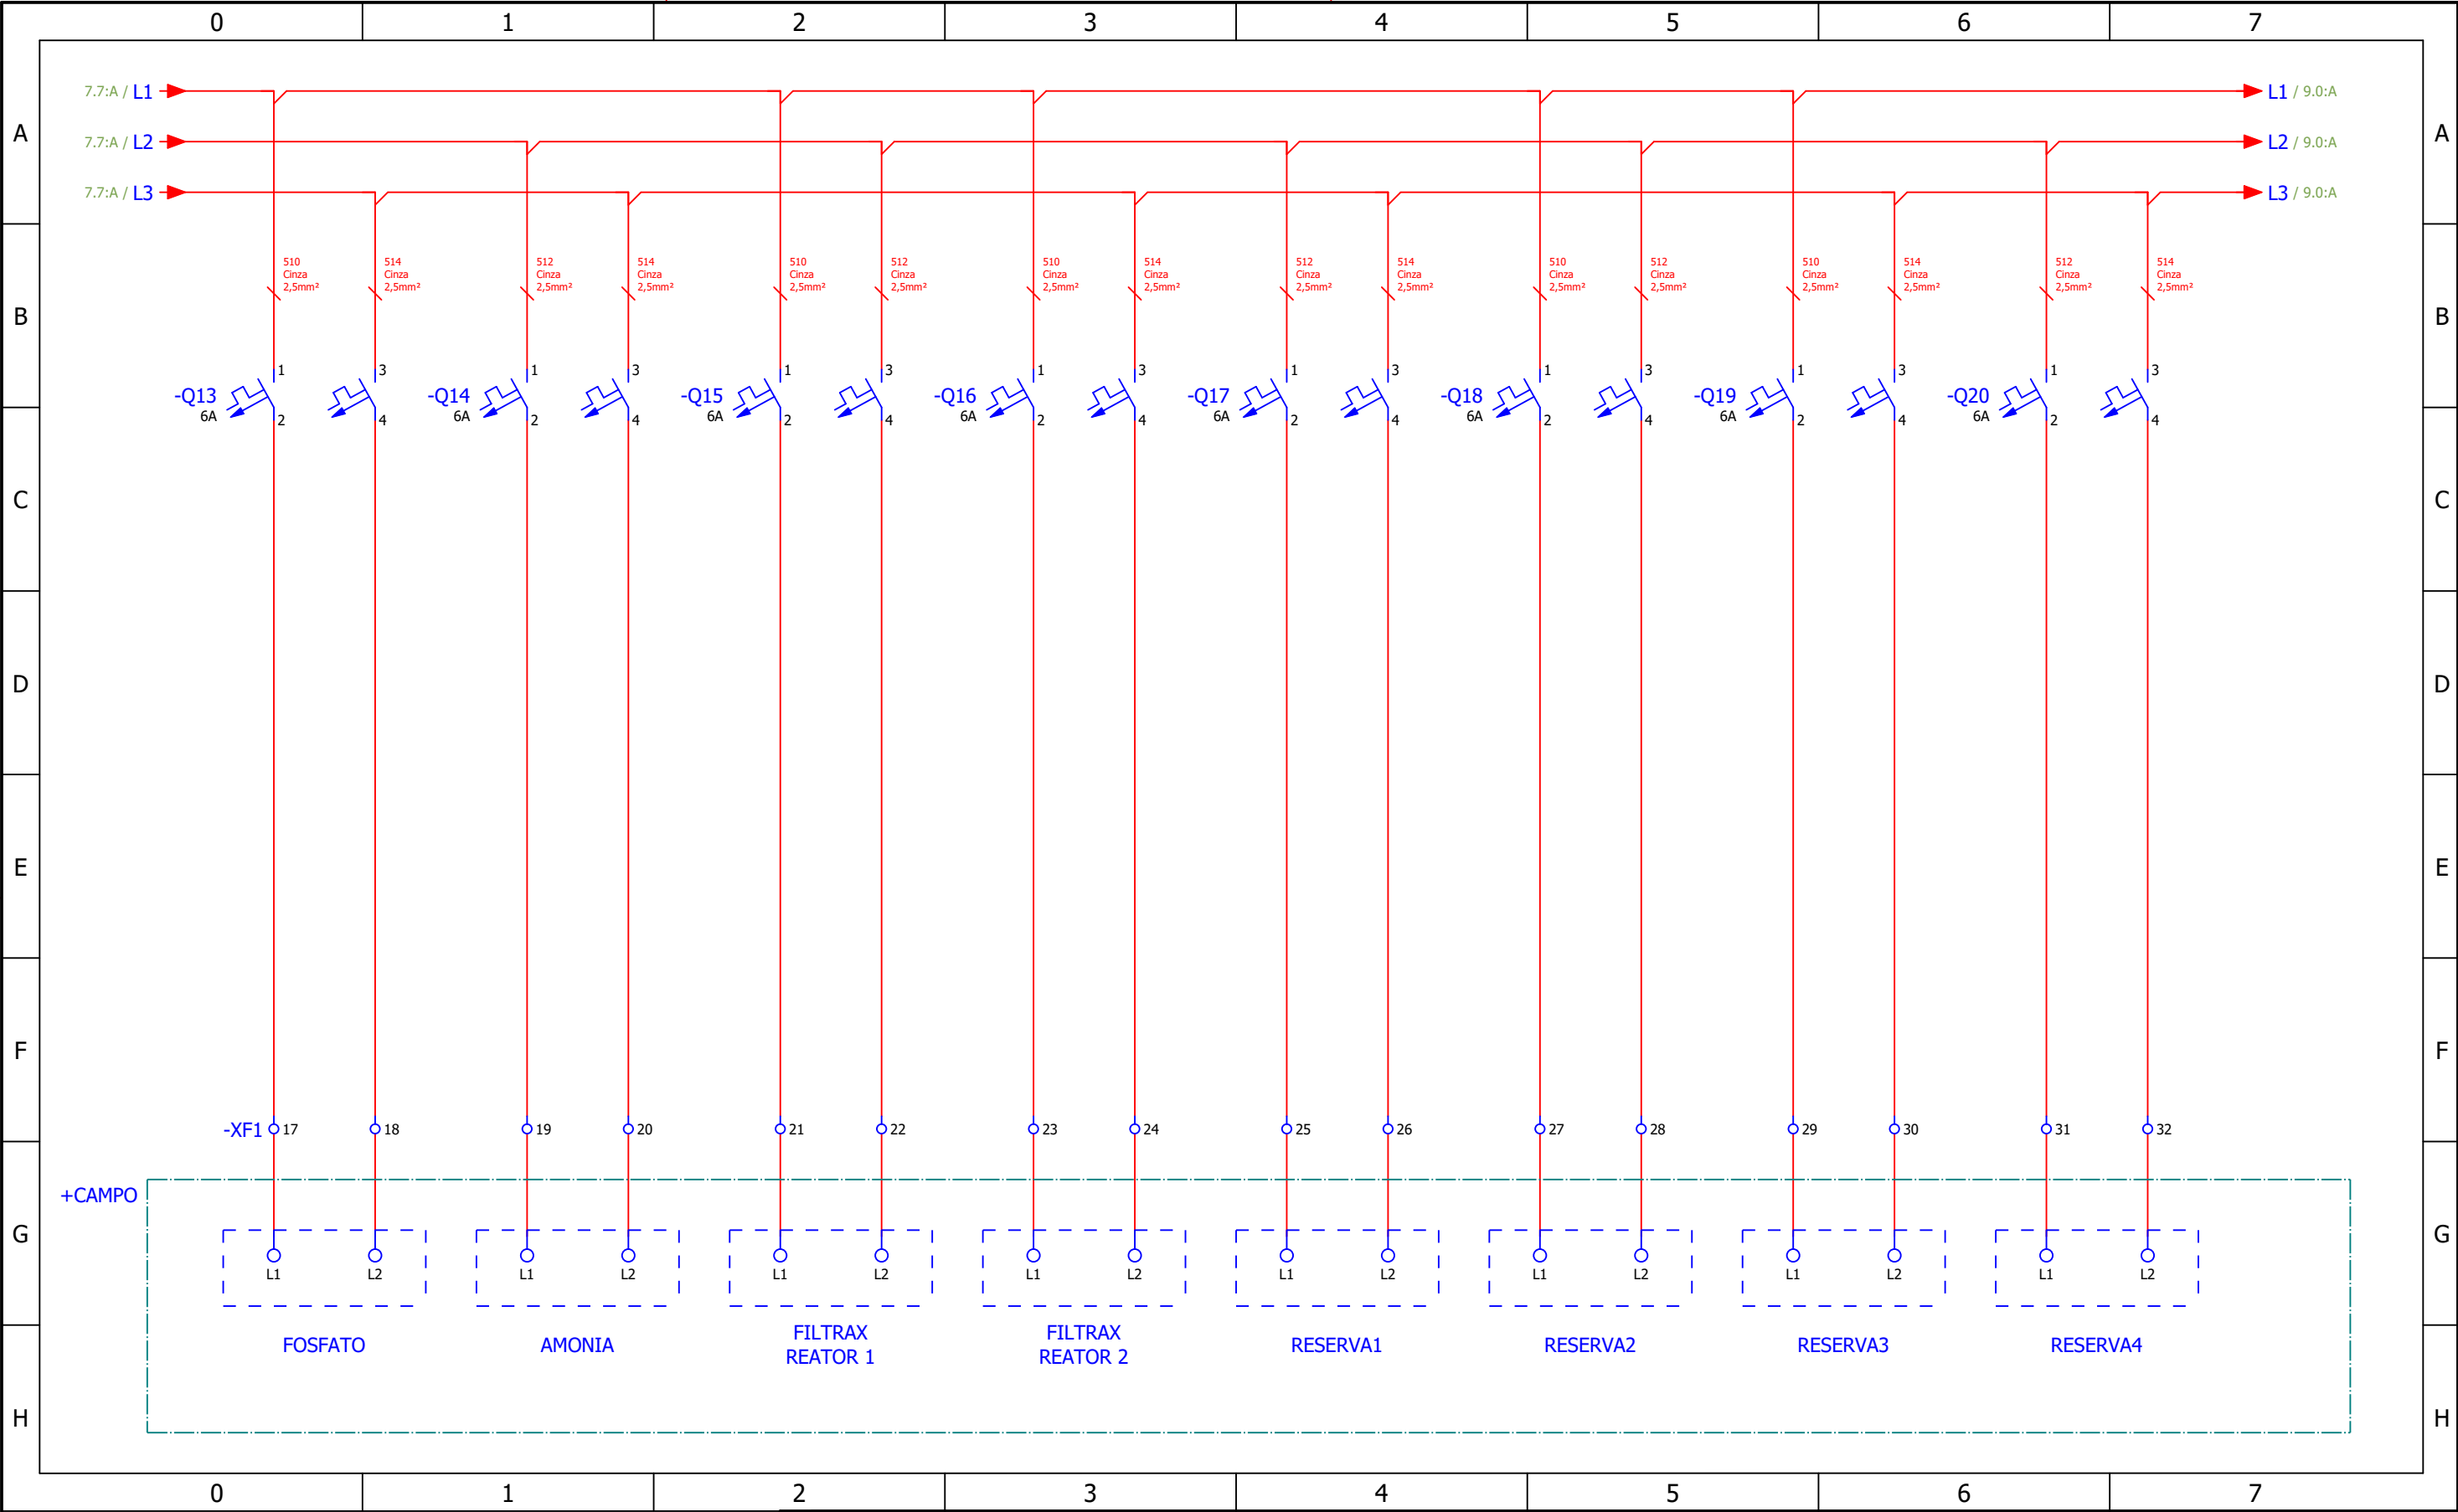

 FOLHA: 8 / 58	LEGENDA:						TÍTULO: PCE NEREDA		
							SUB-TÍTULO: ALIMENTAÇÃO INSTRUMENTOS 220Vca		
	REVISÃO:	EI					UNID. BRK: SUMARÉ	MUNIC./EST.: SUMARÉ-SP	BAIRRO/ÁREA:
	DATA:	03/06/2025					RESP. TÉC.: JEAN CARLOS ESSER 076760-0/SC	APROVAÇÃO BRK AMBIENTAL:	APROVAÇÃO CLIENTE: BRK
	EXECUÇÃO:	Luiz Corrêa					CÓDIGO DO PROJETO: HID-PA-DE-ETE-ELQ-005		
	VERIFICAÇÃO:	Luiz Corrêa					ESCALA: 1:1	REVISÃO: EI	
	APROVAÇÃO:	Rafael Decker				CONTRATANTE: BRK AMBIENTAL	CONTRATO Nº: 230317		

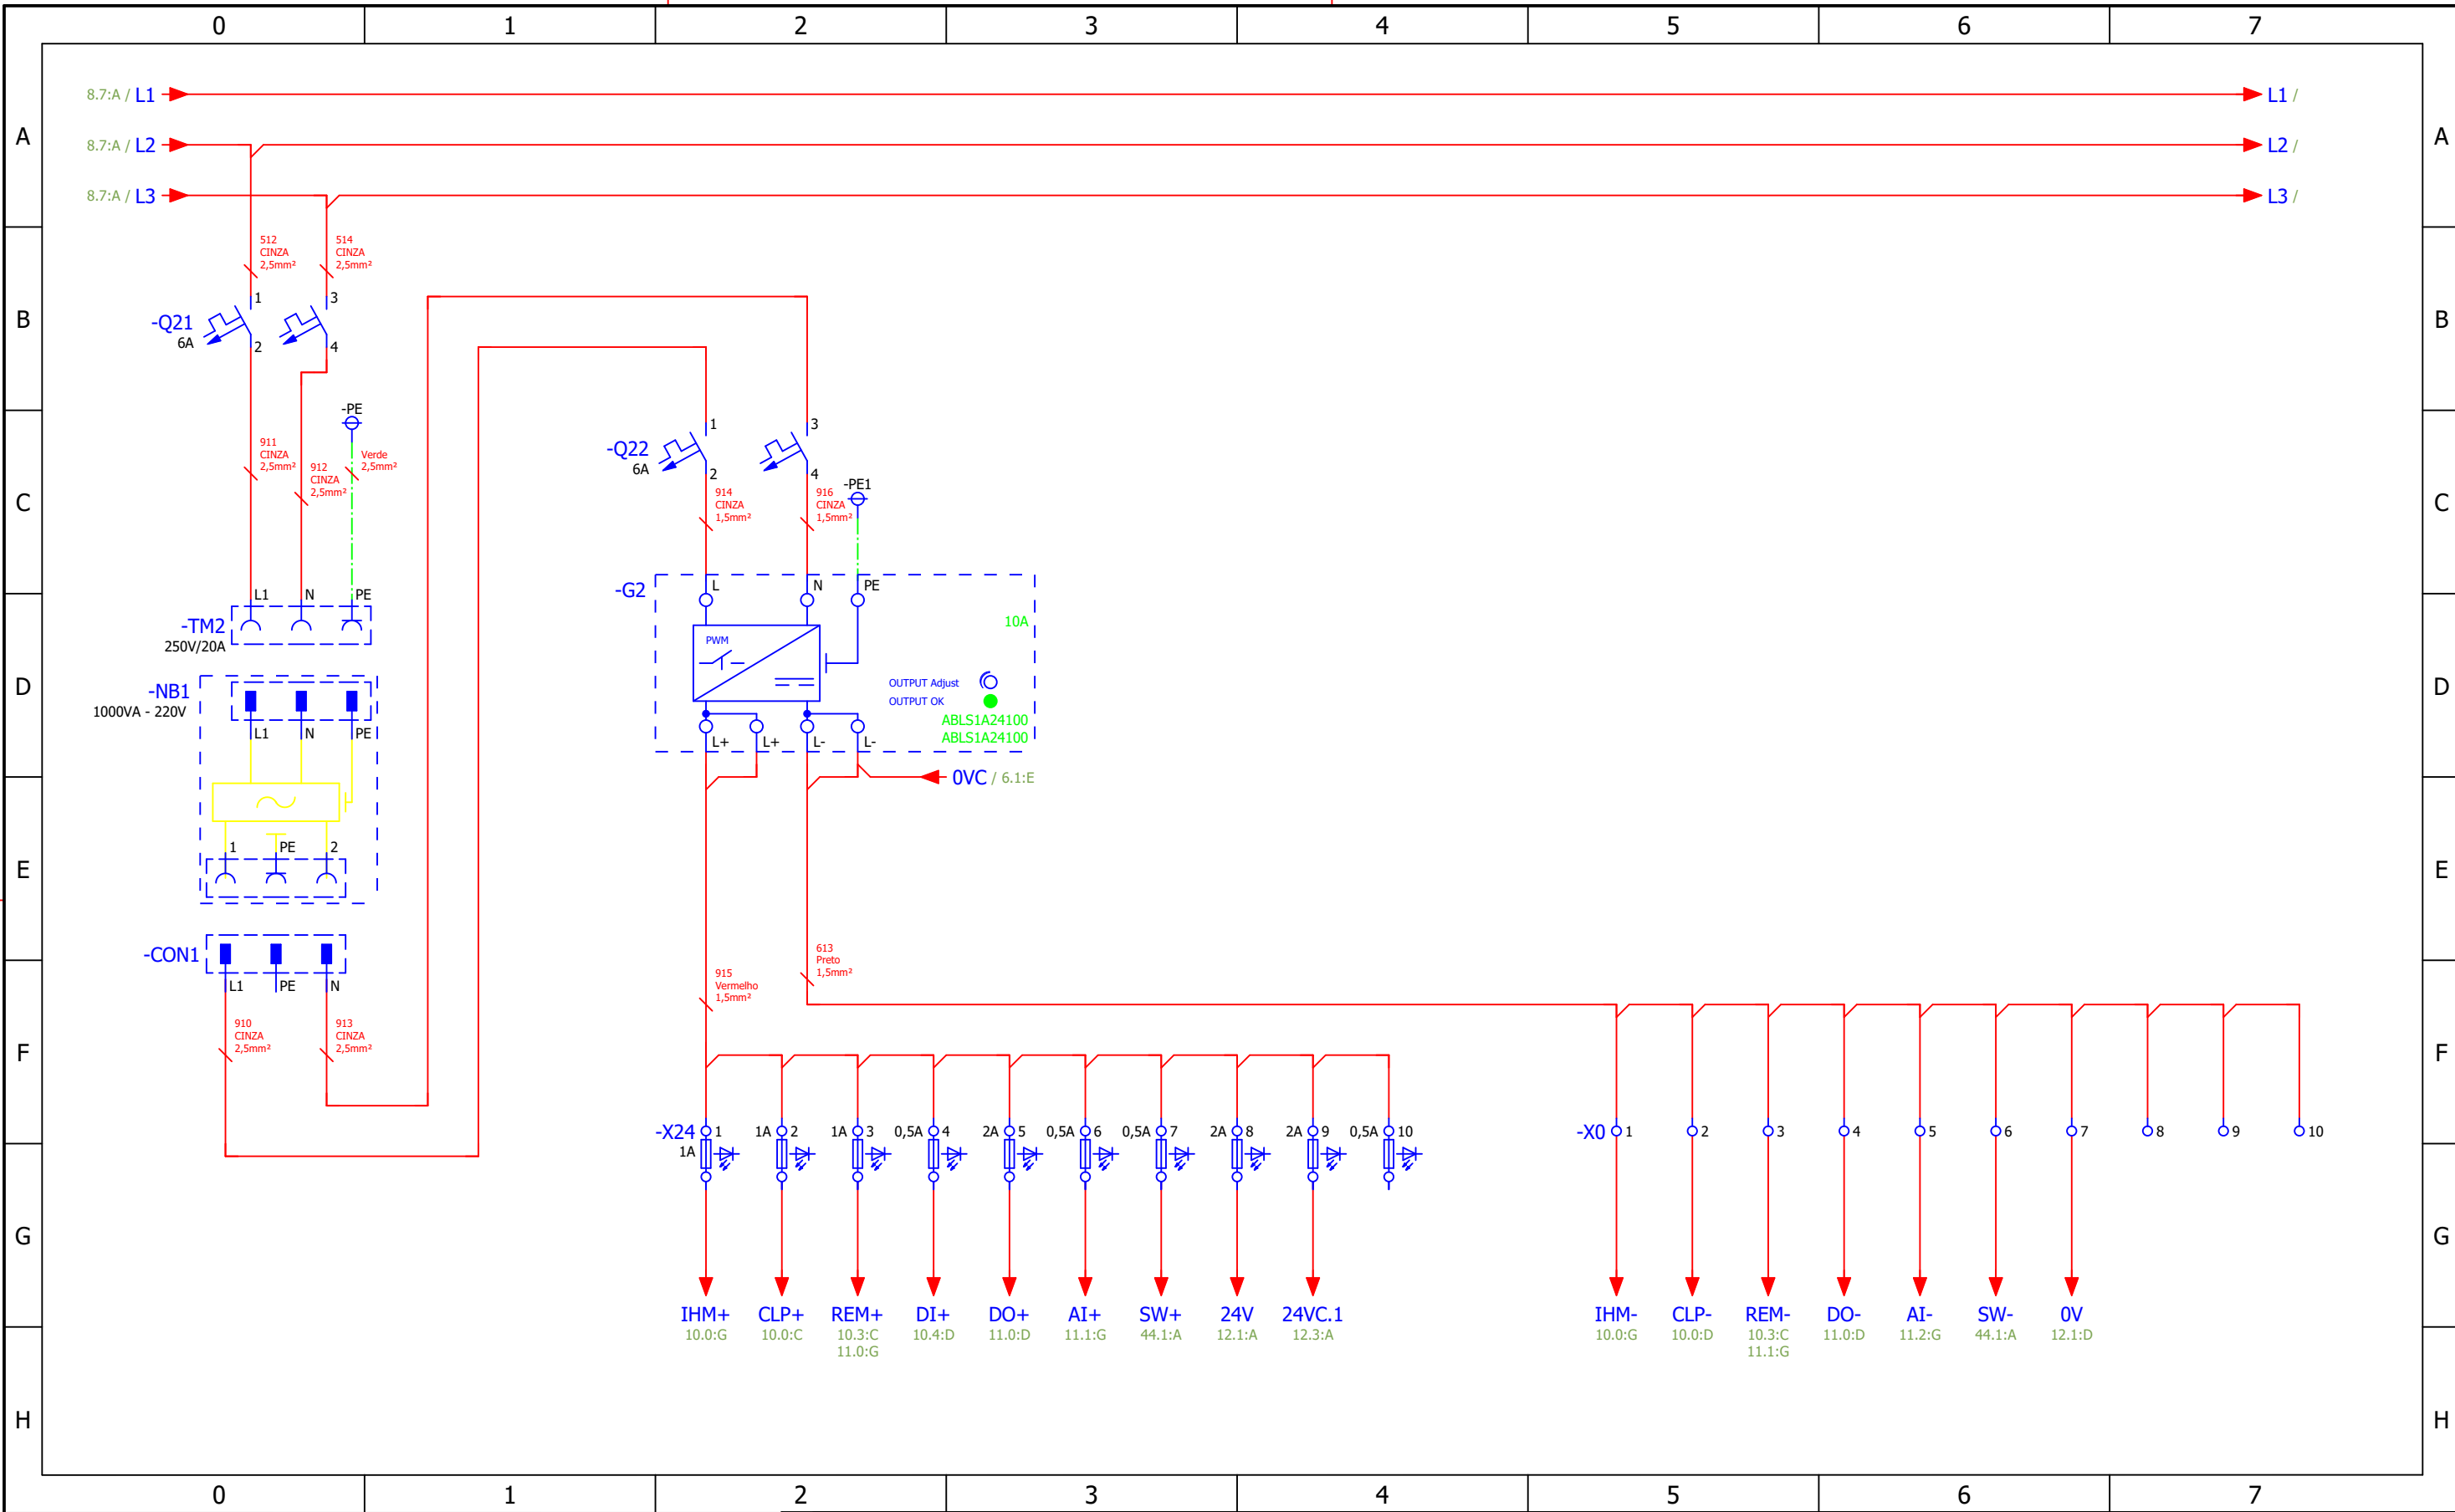

LEGENDA:

REVISÃO:	EI			
DATA:	03/06/2025			
EXECUÇÃO:	Luiz Corrêa			
VERIFICAÇÃO:	Luiz Corrêa			
APROVAÇÃO:	Rafael Decker			

BRK



CONTRATANTE:
BRK AMBIENTAL

CONTRATO Nº:
230317

TÍTULO:

PCE NEREDA

SUB-TÍTULO:

FONTE 24Vcc

UNID. BRK:

SUMARÉ

MUNIC./EST.:

SUMARÉ-SP

BAIRRO/ÁREA:

RESP. TÊC.: **JEAN CARLOS ESSER**
CREA: **076760-0/SC**

APROVAÇÃO BRK AMBIENTAL:

APROVAÇÃO CLIENTE:
BRK

CÓDIGO DO PROJETO:

HID-PA-DE-ETE-ELQ-005

ESCALA:

1:1

REVISÃO:


EI

FORMATO:


HID-PA-DE-ETE-ELQ-005.DWG


FOLHA:
9


58

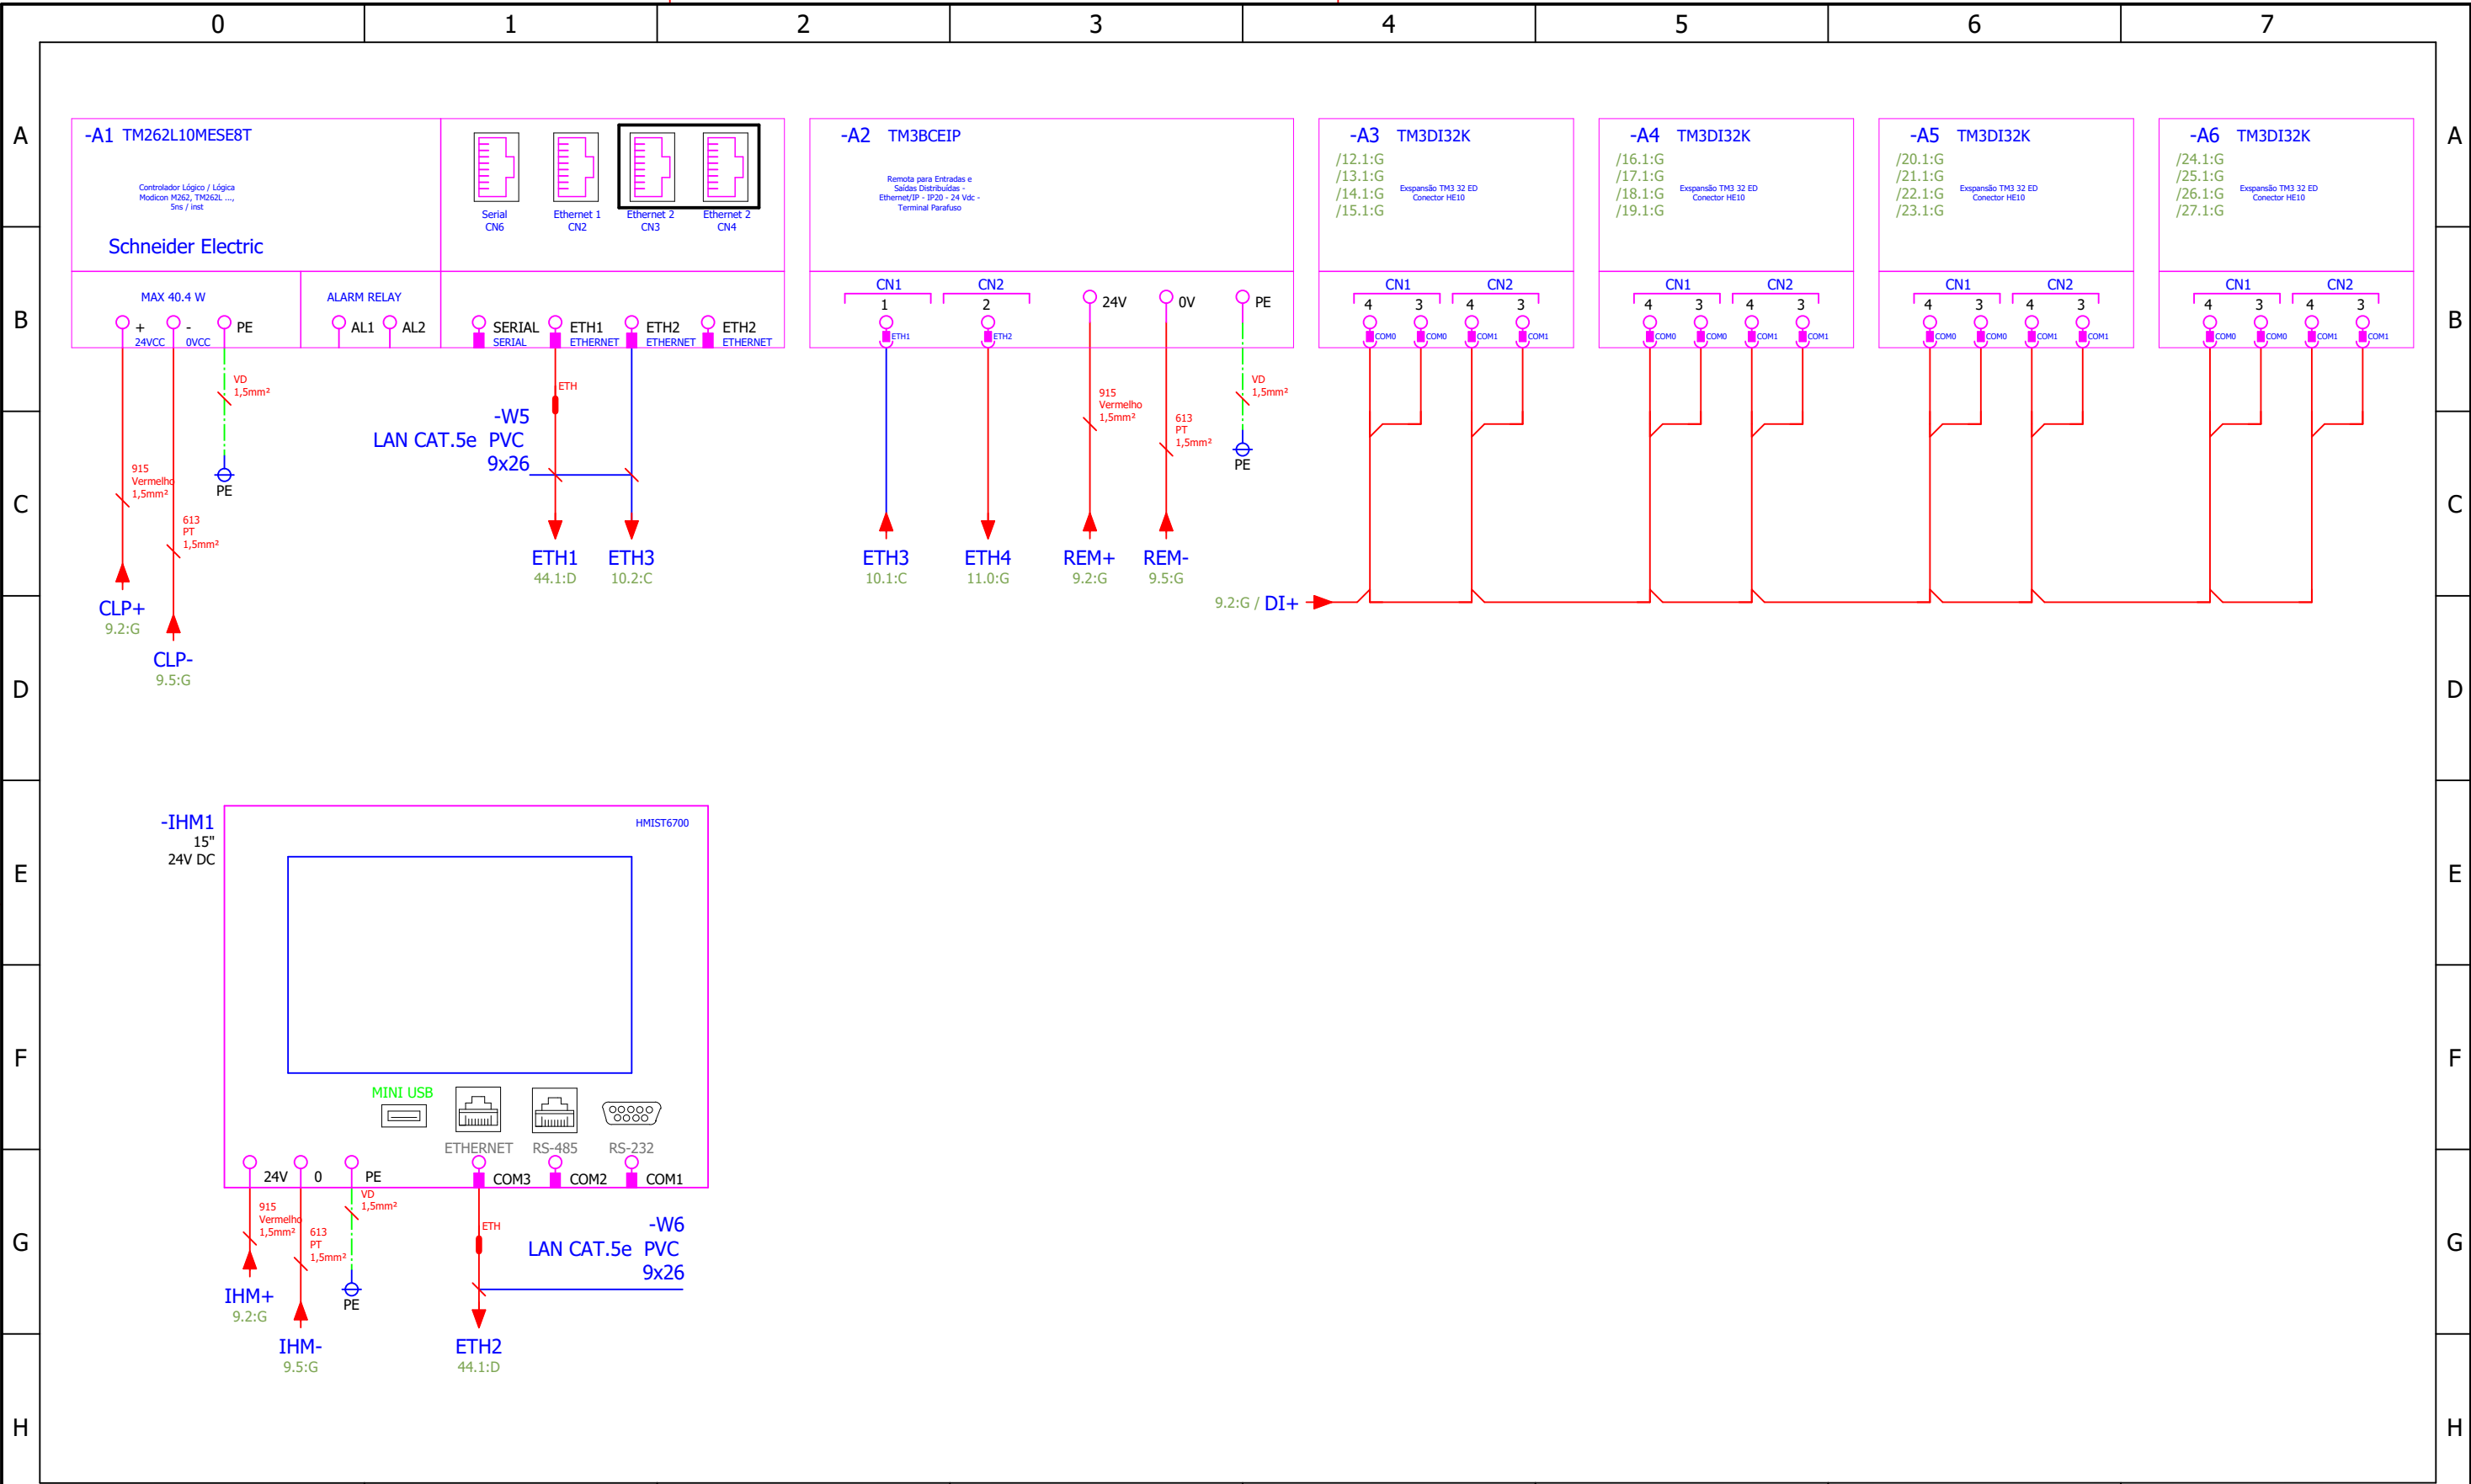


FOLHA: 10 / 58		LEGENDA:							TÍTULO: PCE NEREDA			
									SUB-TÍTULO: DIAGRAMA CLP			
		REVISÃO:	EI						UNID. BRK: SUMARÉ	MUNIC./EST.: SUMARÉ-SP	BAIRRO/ÁREA:	
		DATA:	03/06/2025						RESP. TÊC.: JEAN CARLOS ESSER	APROVAÇÃO BRK AMBIENTAL:	APROVAÇÃO CLIENTE: BRK	
		EXECUÇÃO:	Luiz Corrêa						CREA: 076760-0/SC			
		VERIFICAÇÃO:	Luiz Corrêa				CONTRATANTE: BRK AMBIENTAL		CONTRATO Nº: 230317		CÓDIGO DO PROJETO: HID-PA-DE-ETE-ELQ-005	ESCALA: 1:1
APROVAÇÃO:	Rafael Decker											

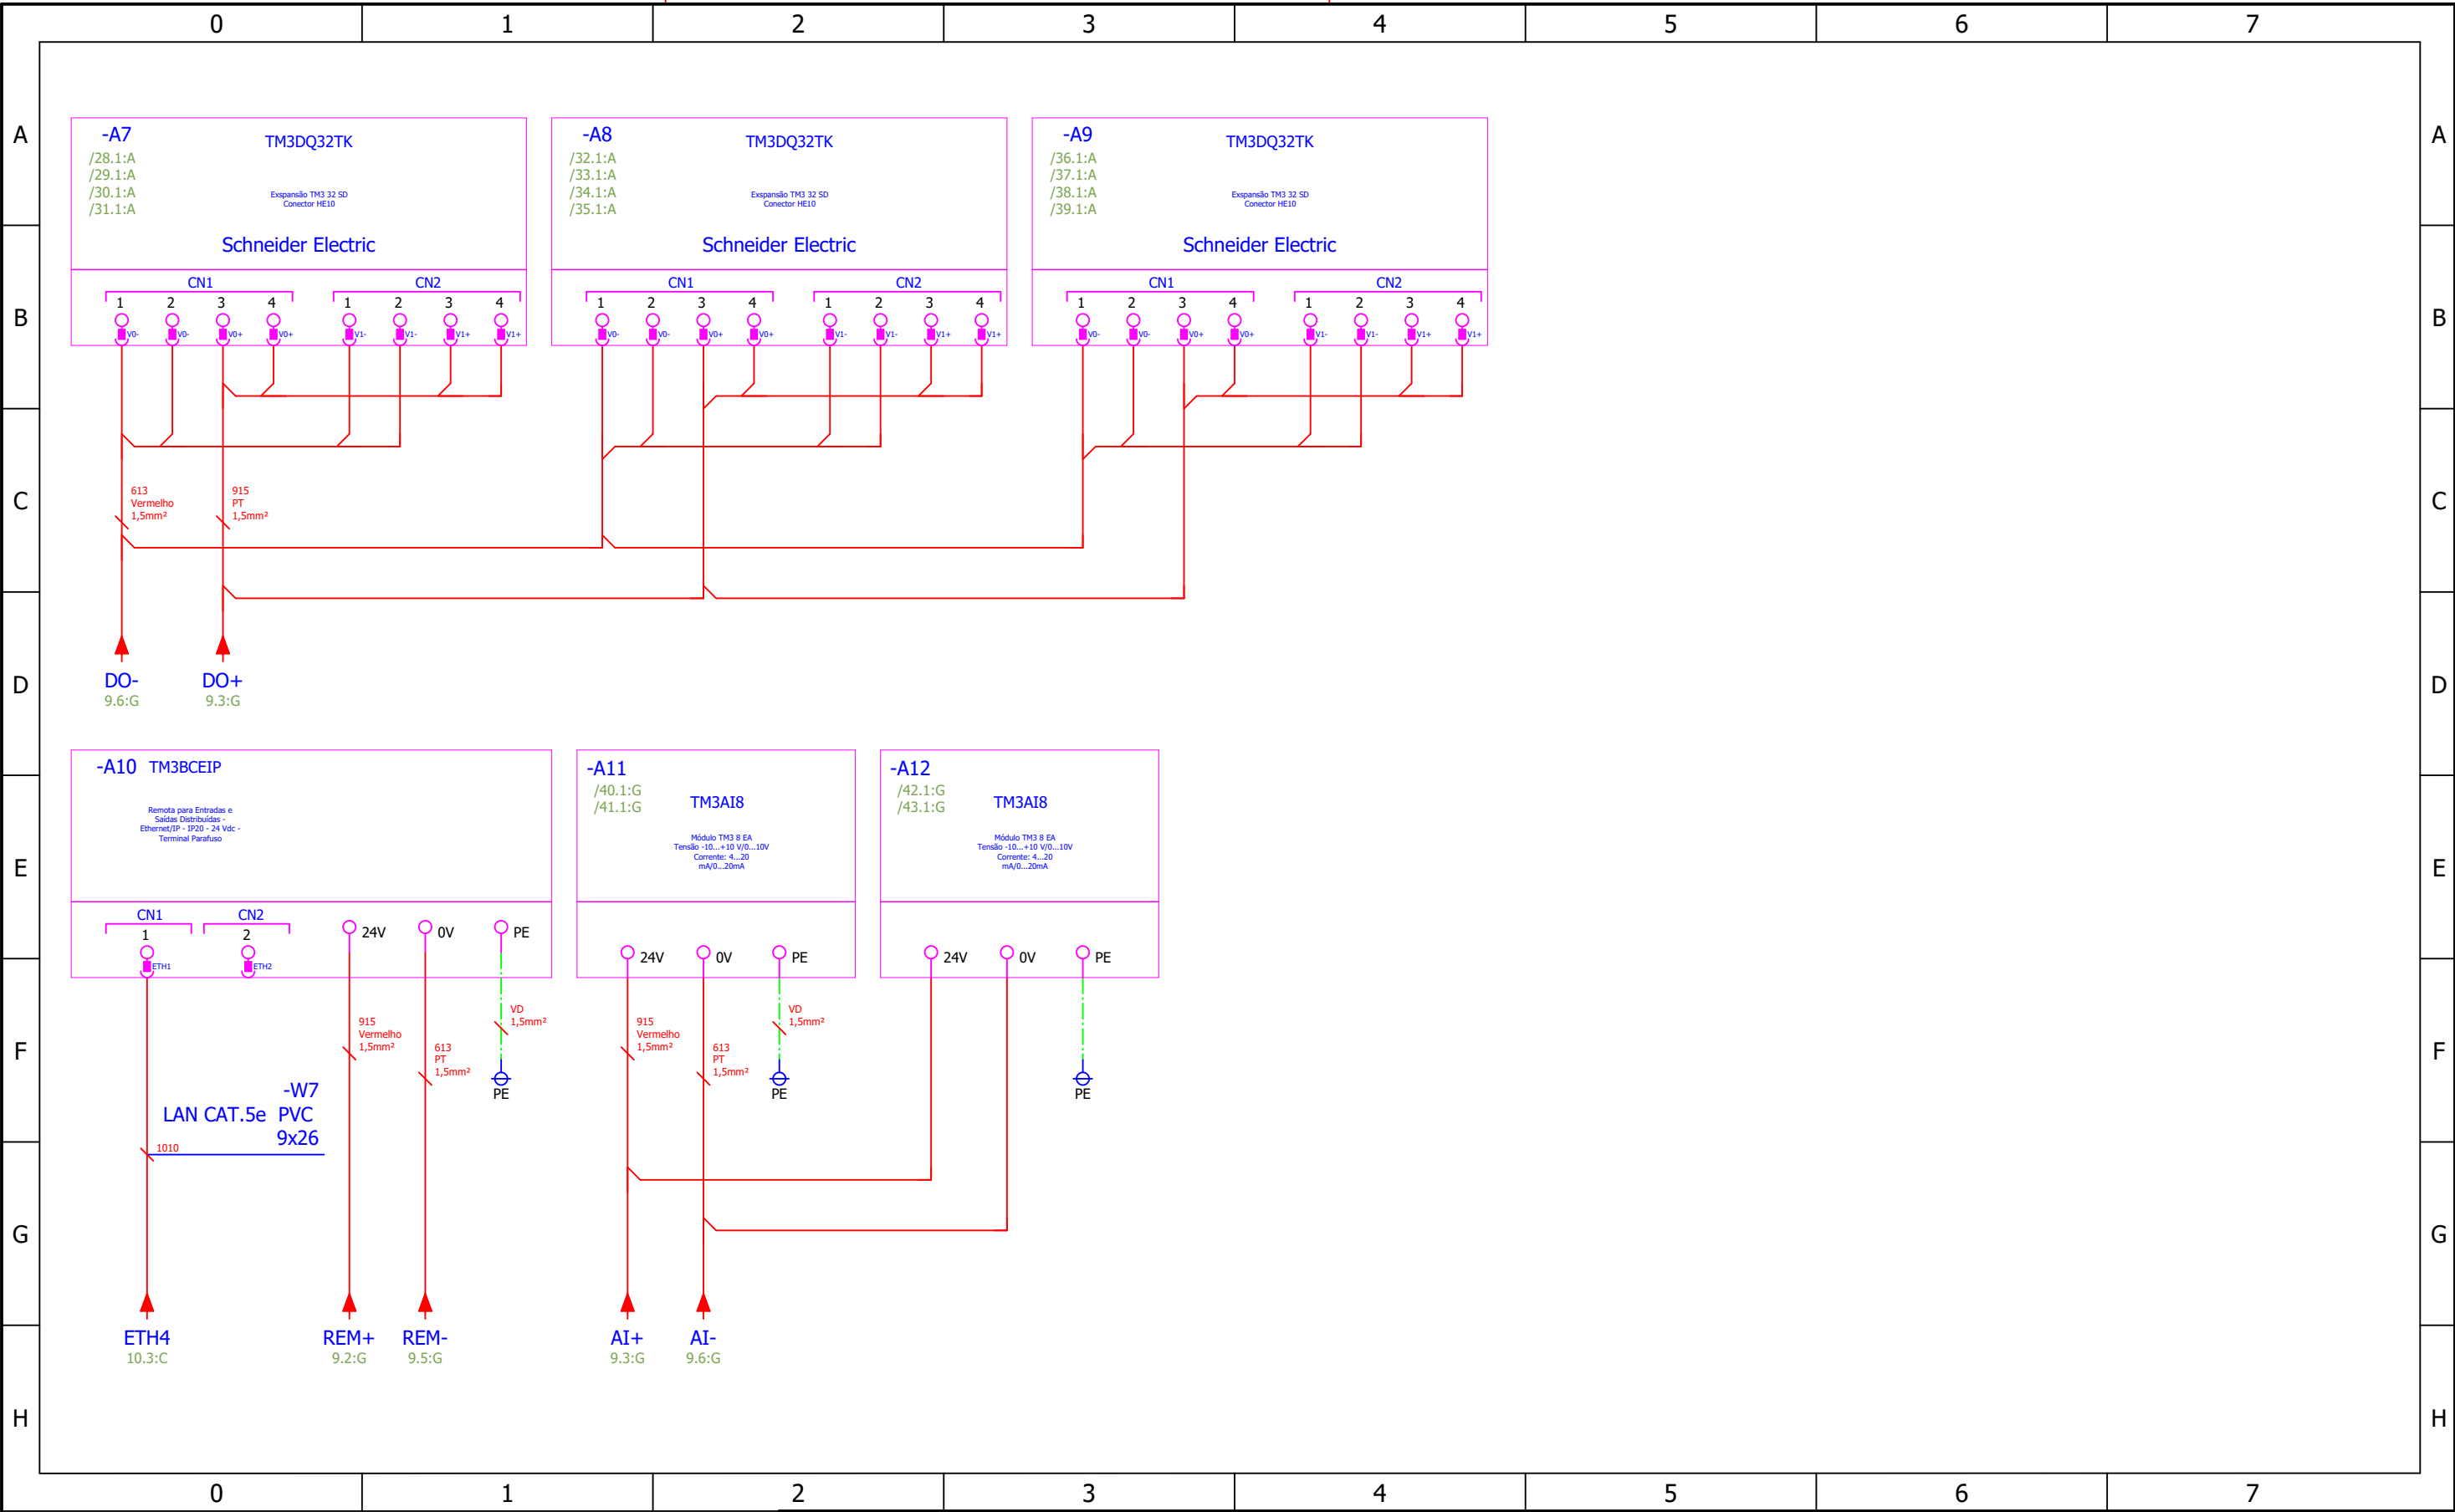

 
FOLHA: 11 / 58		LEGENDA:							TÍTULO: PCE NEREDA						
									SUB-TÍTULO: DIAGRAMA CLP						
		REVISÃO:		EI						UNID. BRK: SUMARÉ		MUNIC./EST.: SUMARÉ-SP		BAIRRO/ÁREA:	
		DATA:		03/06/2025						RESP. TÊC.: JEAN CARLOS ESSER 076760-0/SC		APROVAÇÃO BRK AMBIENTAL:		APROVAÇÃO CLIENTE: BRK	
		EXECUÇÃO:		Luiz Corrêa						CREA:					
		VERIFICAÇÃO:		Luiz Corrêa				CONTRATANTE: BRK AMBIENTAL		CONTRATO Nº: 230317		CÓDIGO DO PROJETO: HID-PA-DE-ETE-ELQ-005		ESCALA: 1:1	
APROVAÇÃO:		Rafael Decker													

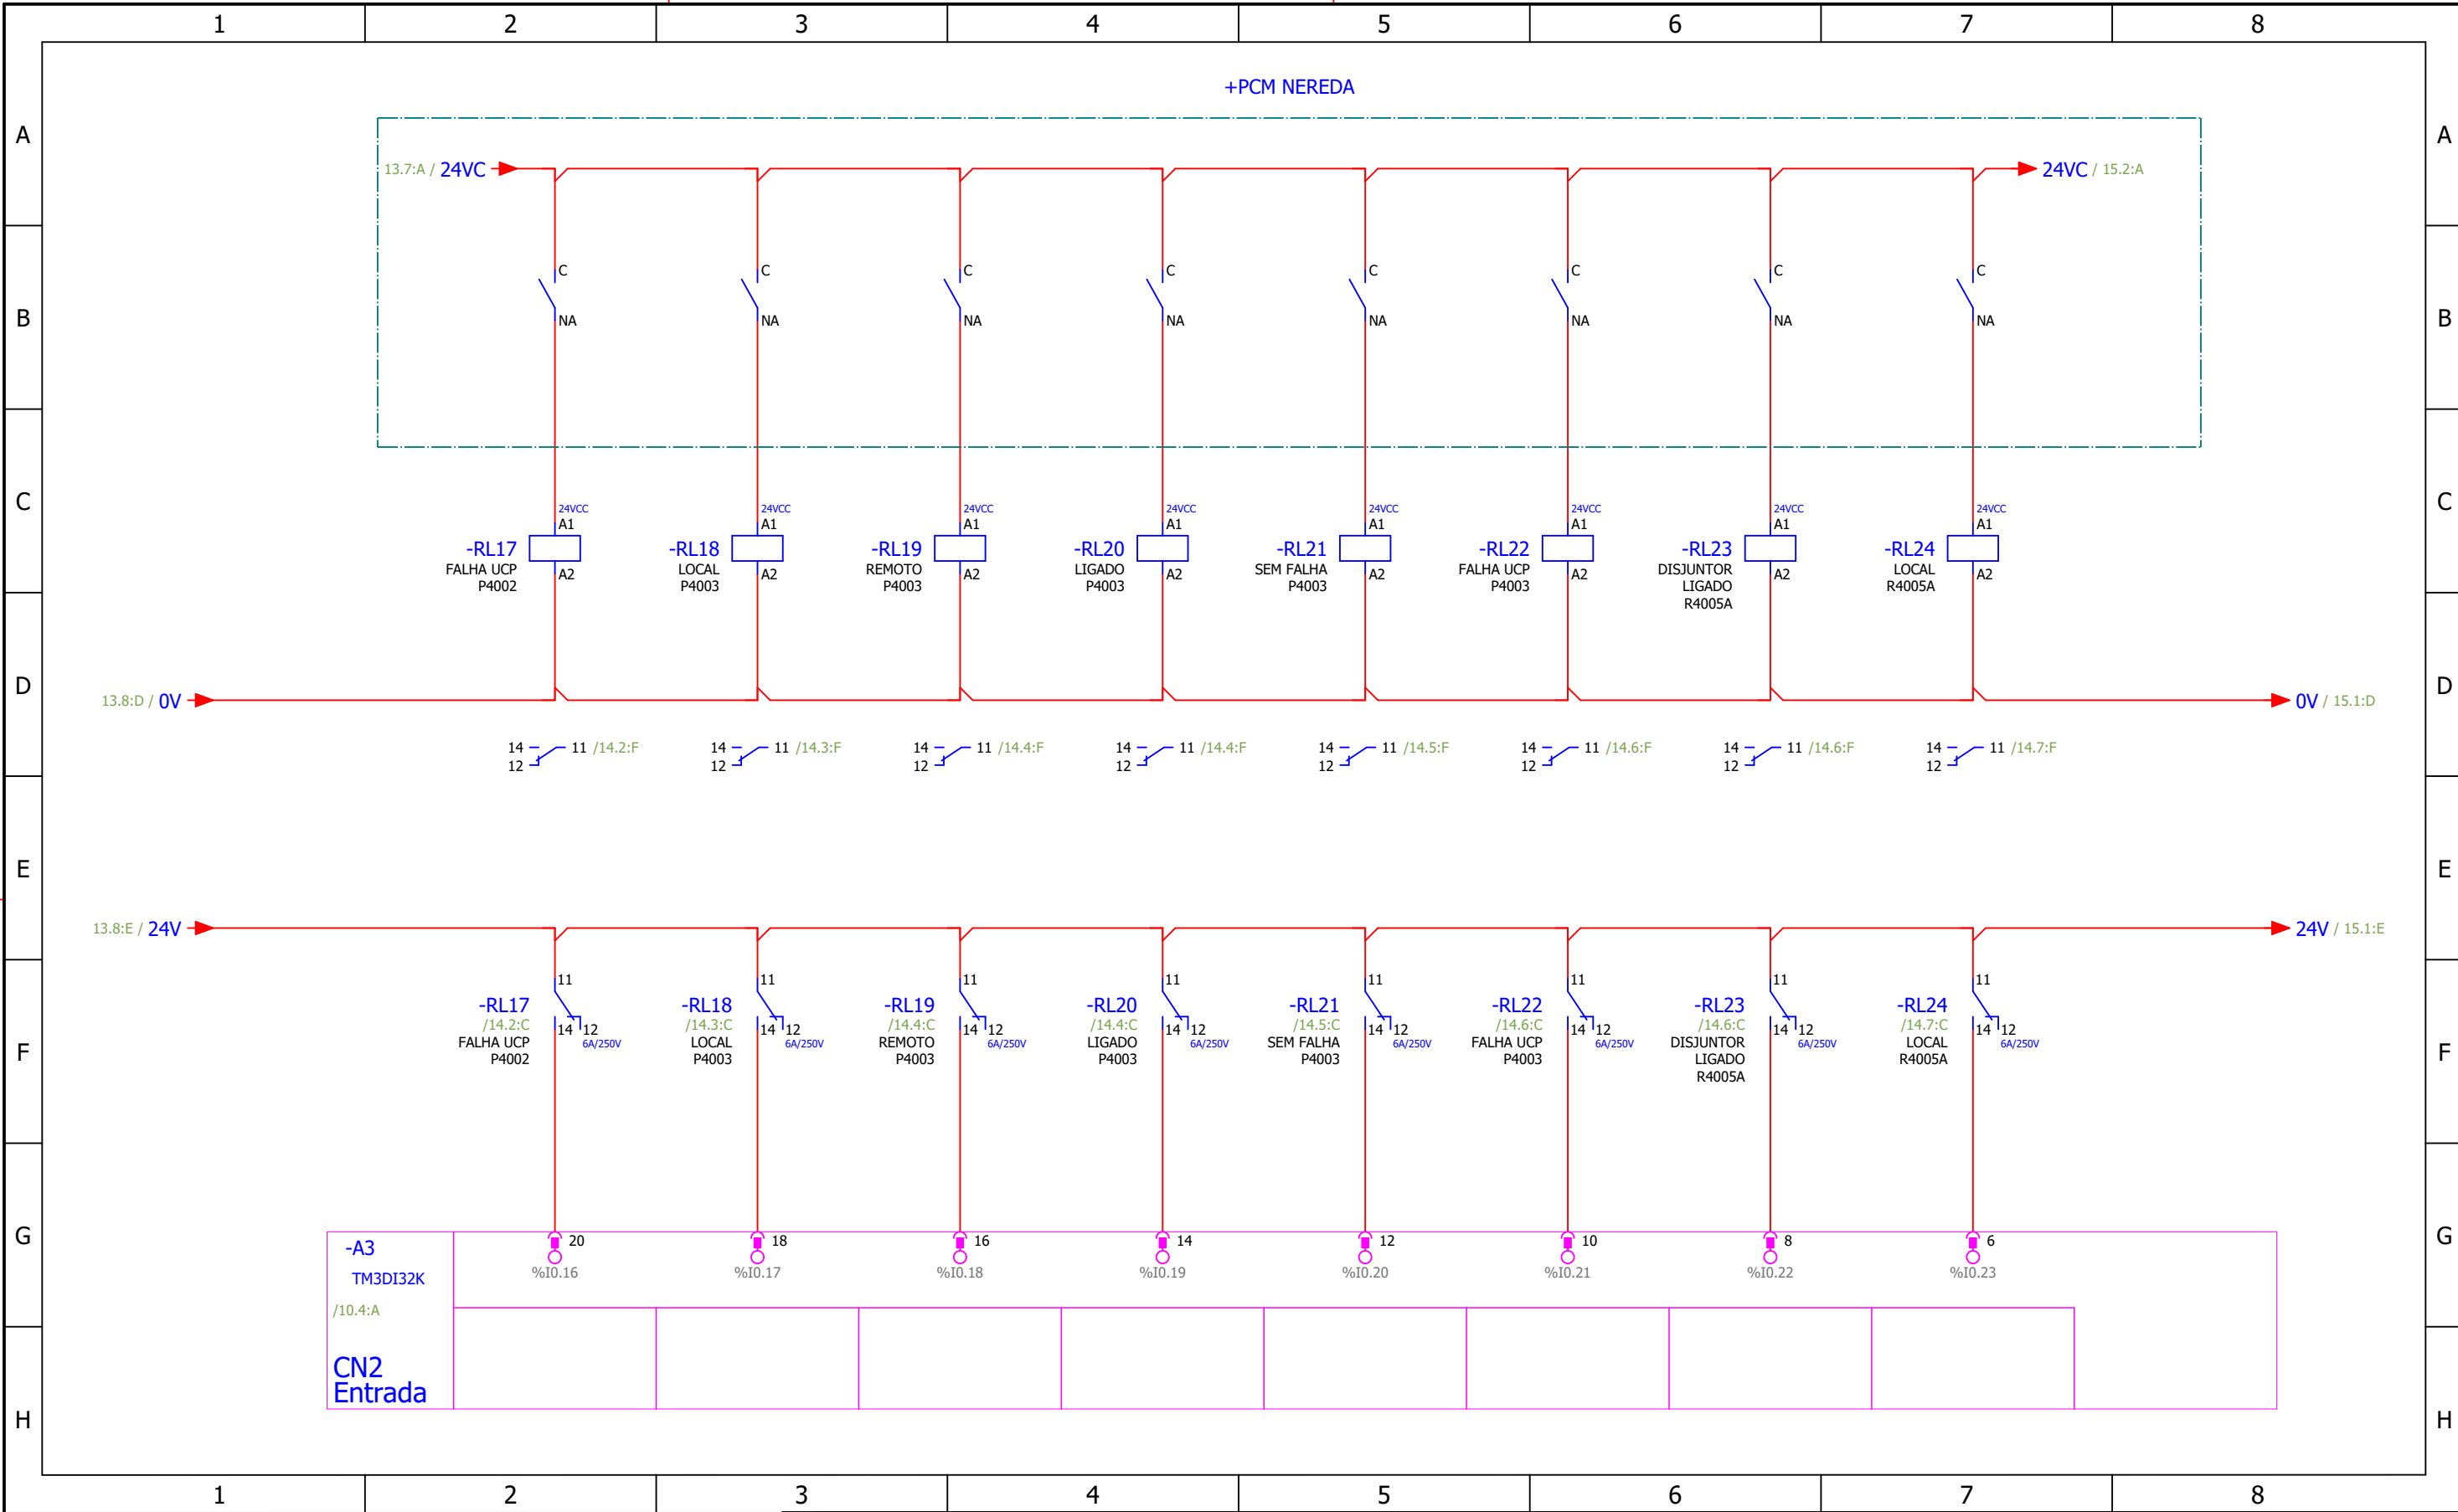


FOLHA: 14 / 58	LEGENDA:						TÍTULO: PCE NEREDA				
							SUB-TÍTULO: Entradas Digitais				
	REVISÃO:	EI					UNID. BRK: SUMARÉ	MUNIC./EST.: SUMARÉ-SP	BAIRRO/ÁREA:		
	DATA:	03/06/2025					RESP. TÊC.: JEAN CARLOS ESSER 076760-0/SC	APROVAÇÃO BRK AMBIENTAL:	APROVAÇÃO CLIENTE: BRK		
	EXECUÇÃO:	Luiz Corrêa					CÓDIGO DO PROJETO: HID-PA-DE-ETE-ELQ-005		ESCALA: 1:1	REVISÃO: EI	
	VERIFICAÇÃO:	Luiz Corrêa									
	APROVAÇÃO:	Rafael Decker				CONTRATANTE: BRK AMBIENTAL	CONTRATO Nº: 230317				

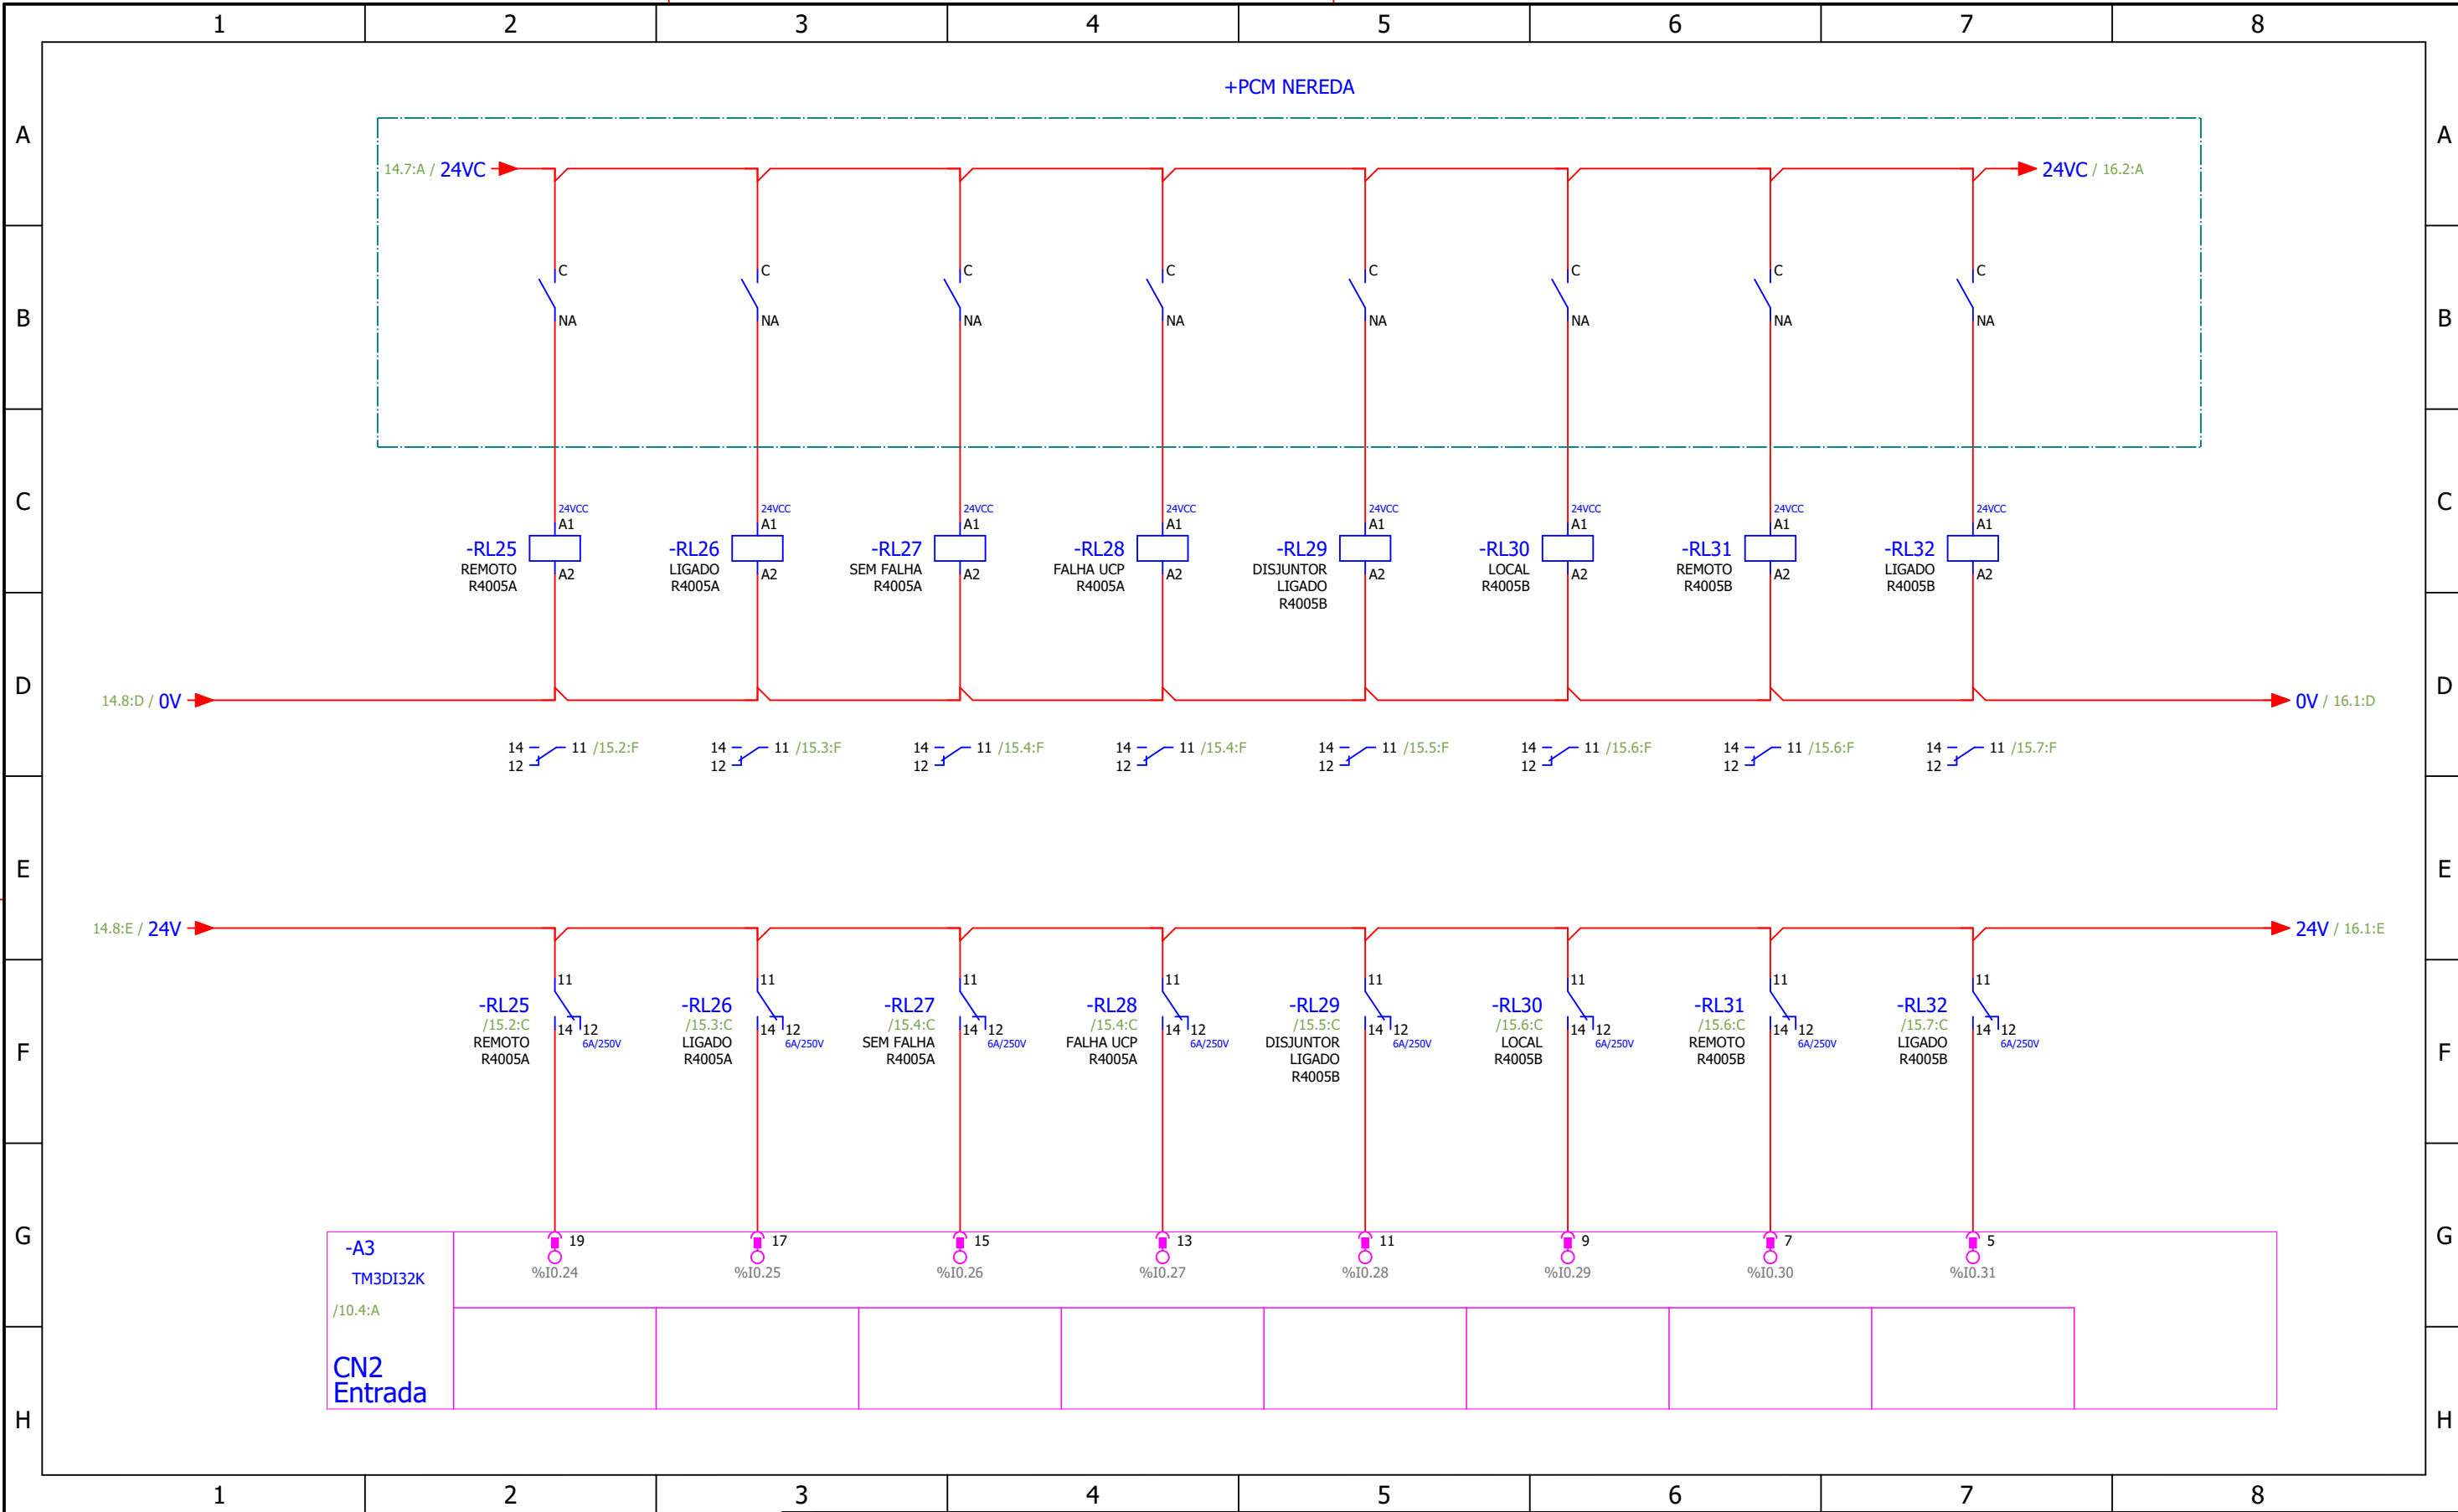


FOLHA: 15 / 58		LEGENDA:						TÍTULO: PCE NEREDA		
								SUB-TÍTULO: Entradas Digitais		
		REVISÃO:	EI					UNID. BRK: SUMARÉ	MUNIC./EST.: SUMARÉ-SP	BAIRRO/ÁREA:
		DATA:	03/06/2025					RESP. TÊC.: JEAN CARLOS ESSER	APROVAÇÃO BRK AMBIENTAL:	APROVAÇÃO CLIENTE: BRK
		EXECUÇÃO:	Luiz Corrêa					CREA: 076760-0/SC		
		VERIFICAÇÃO:	Luiz Corrêa					CÓDIGO DO PROJETO: HID-PA-DE-ETE-ELQ-005		
		APROVAÇÃO:	Rafael Decker					CONTRATANTE: BRK AMBIENTAL	CONTRATO Nº: 230317	ESCALA: 1:1

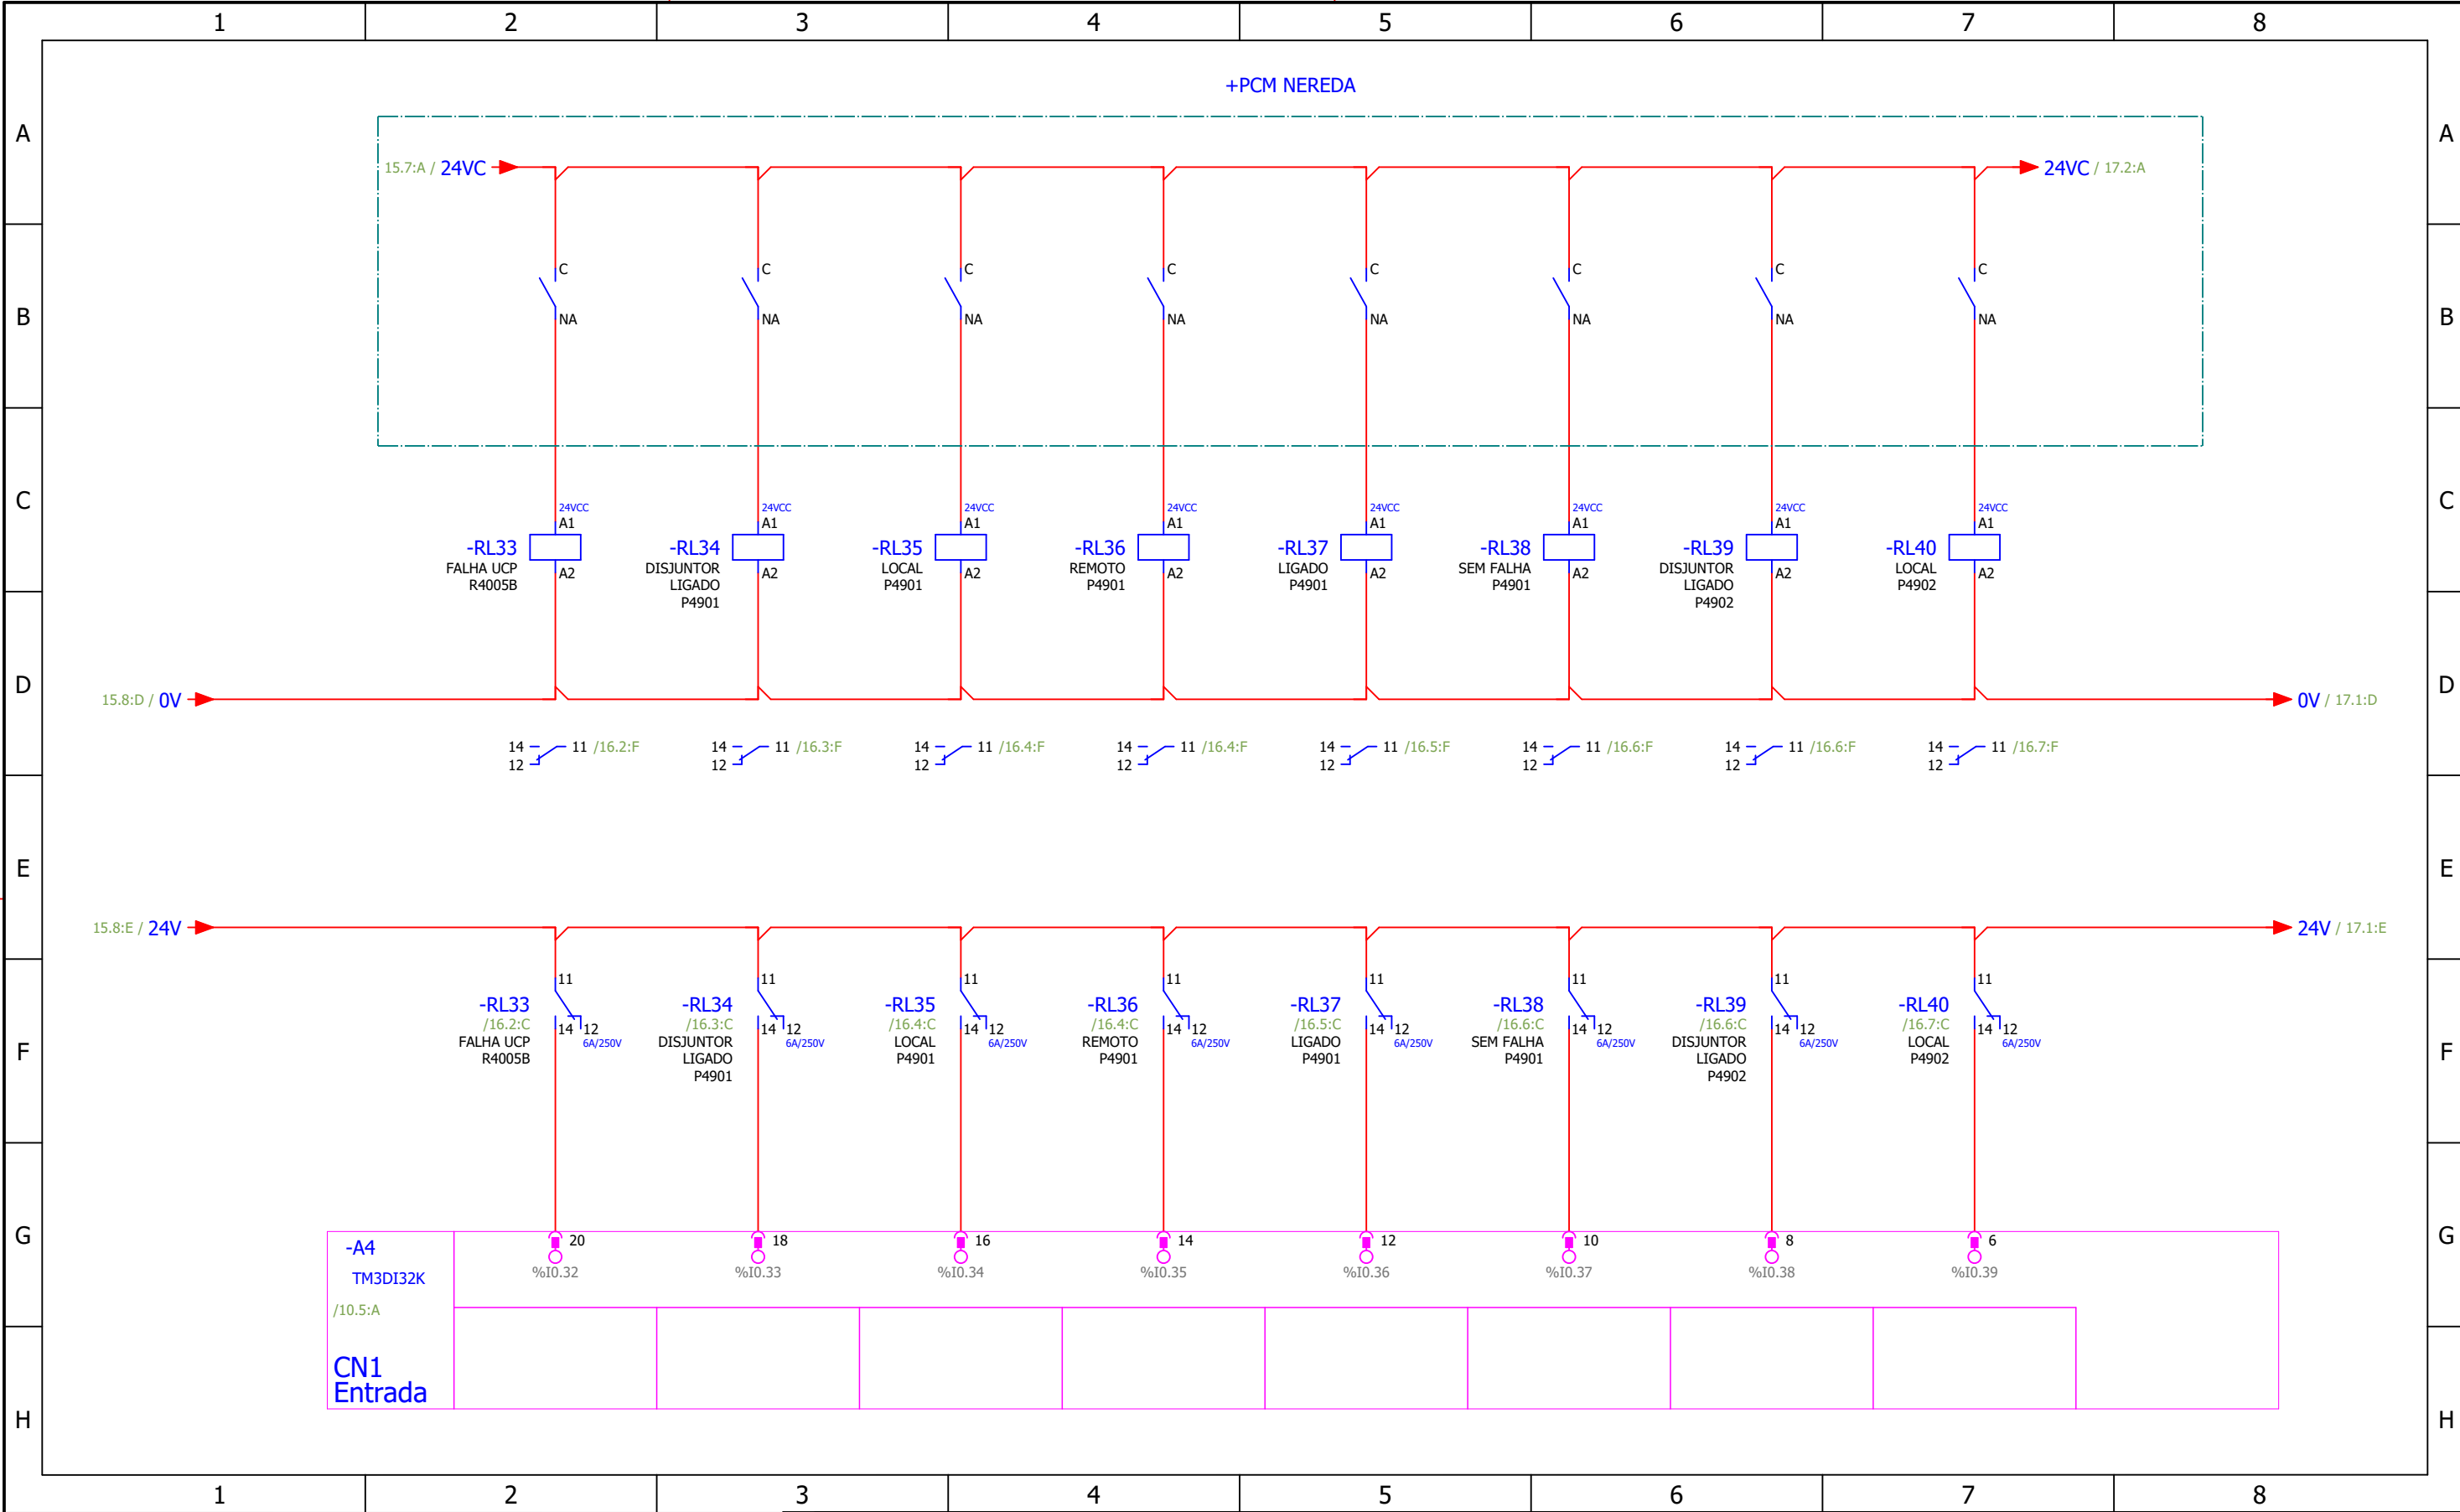


FOLHA: 16 / 58	LEGENDA:					TÍTULO: PCE NEREDA			
						SUB-TÍTULO: Entradas Digitais			
	REVISÃO:	EI					UNID. BRK: SUMARÉ	MUNIC./EST.: SUMARÉ-SP	BAIRRO/ÁREA:
	DATA:	03/06/2025					RESP. TÊC.: JEAN CARLOS ESSER 076760-0/SC	APROVAÇÃO BRK AMBIENTAL:	APROVAÇÃO CLIENTE: BRK
	EXECUÇÃO:	Luiz Corrêa					CÓDIGO DO PROJETO: HID-PA-DE-ETE-ELQ-005		
	VERIFICAÇÃO:	Luiz Corrêa					ESCALA: 1:1	REVISÃO: EI	
	APROVAÇÃO:	Rafael Decker				CONTRATANTE: BRK AMBIENTAL	CONTRATO Nº: 230317		

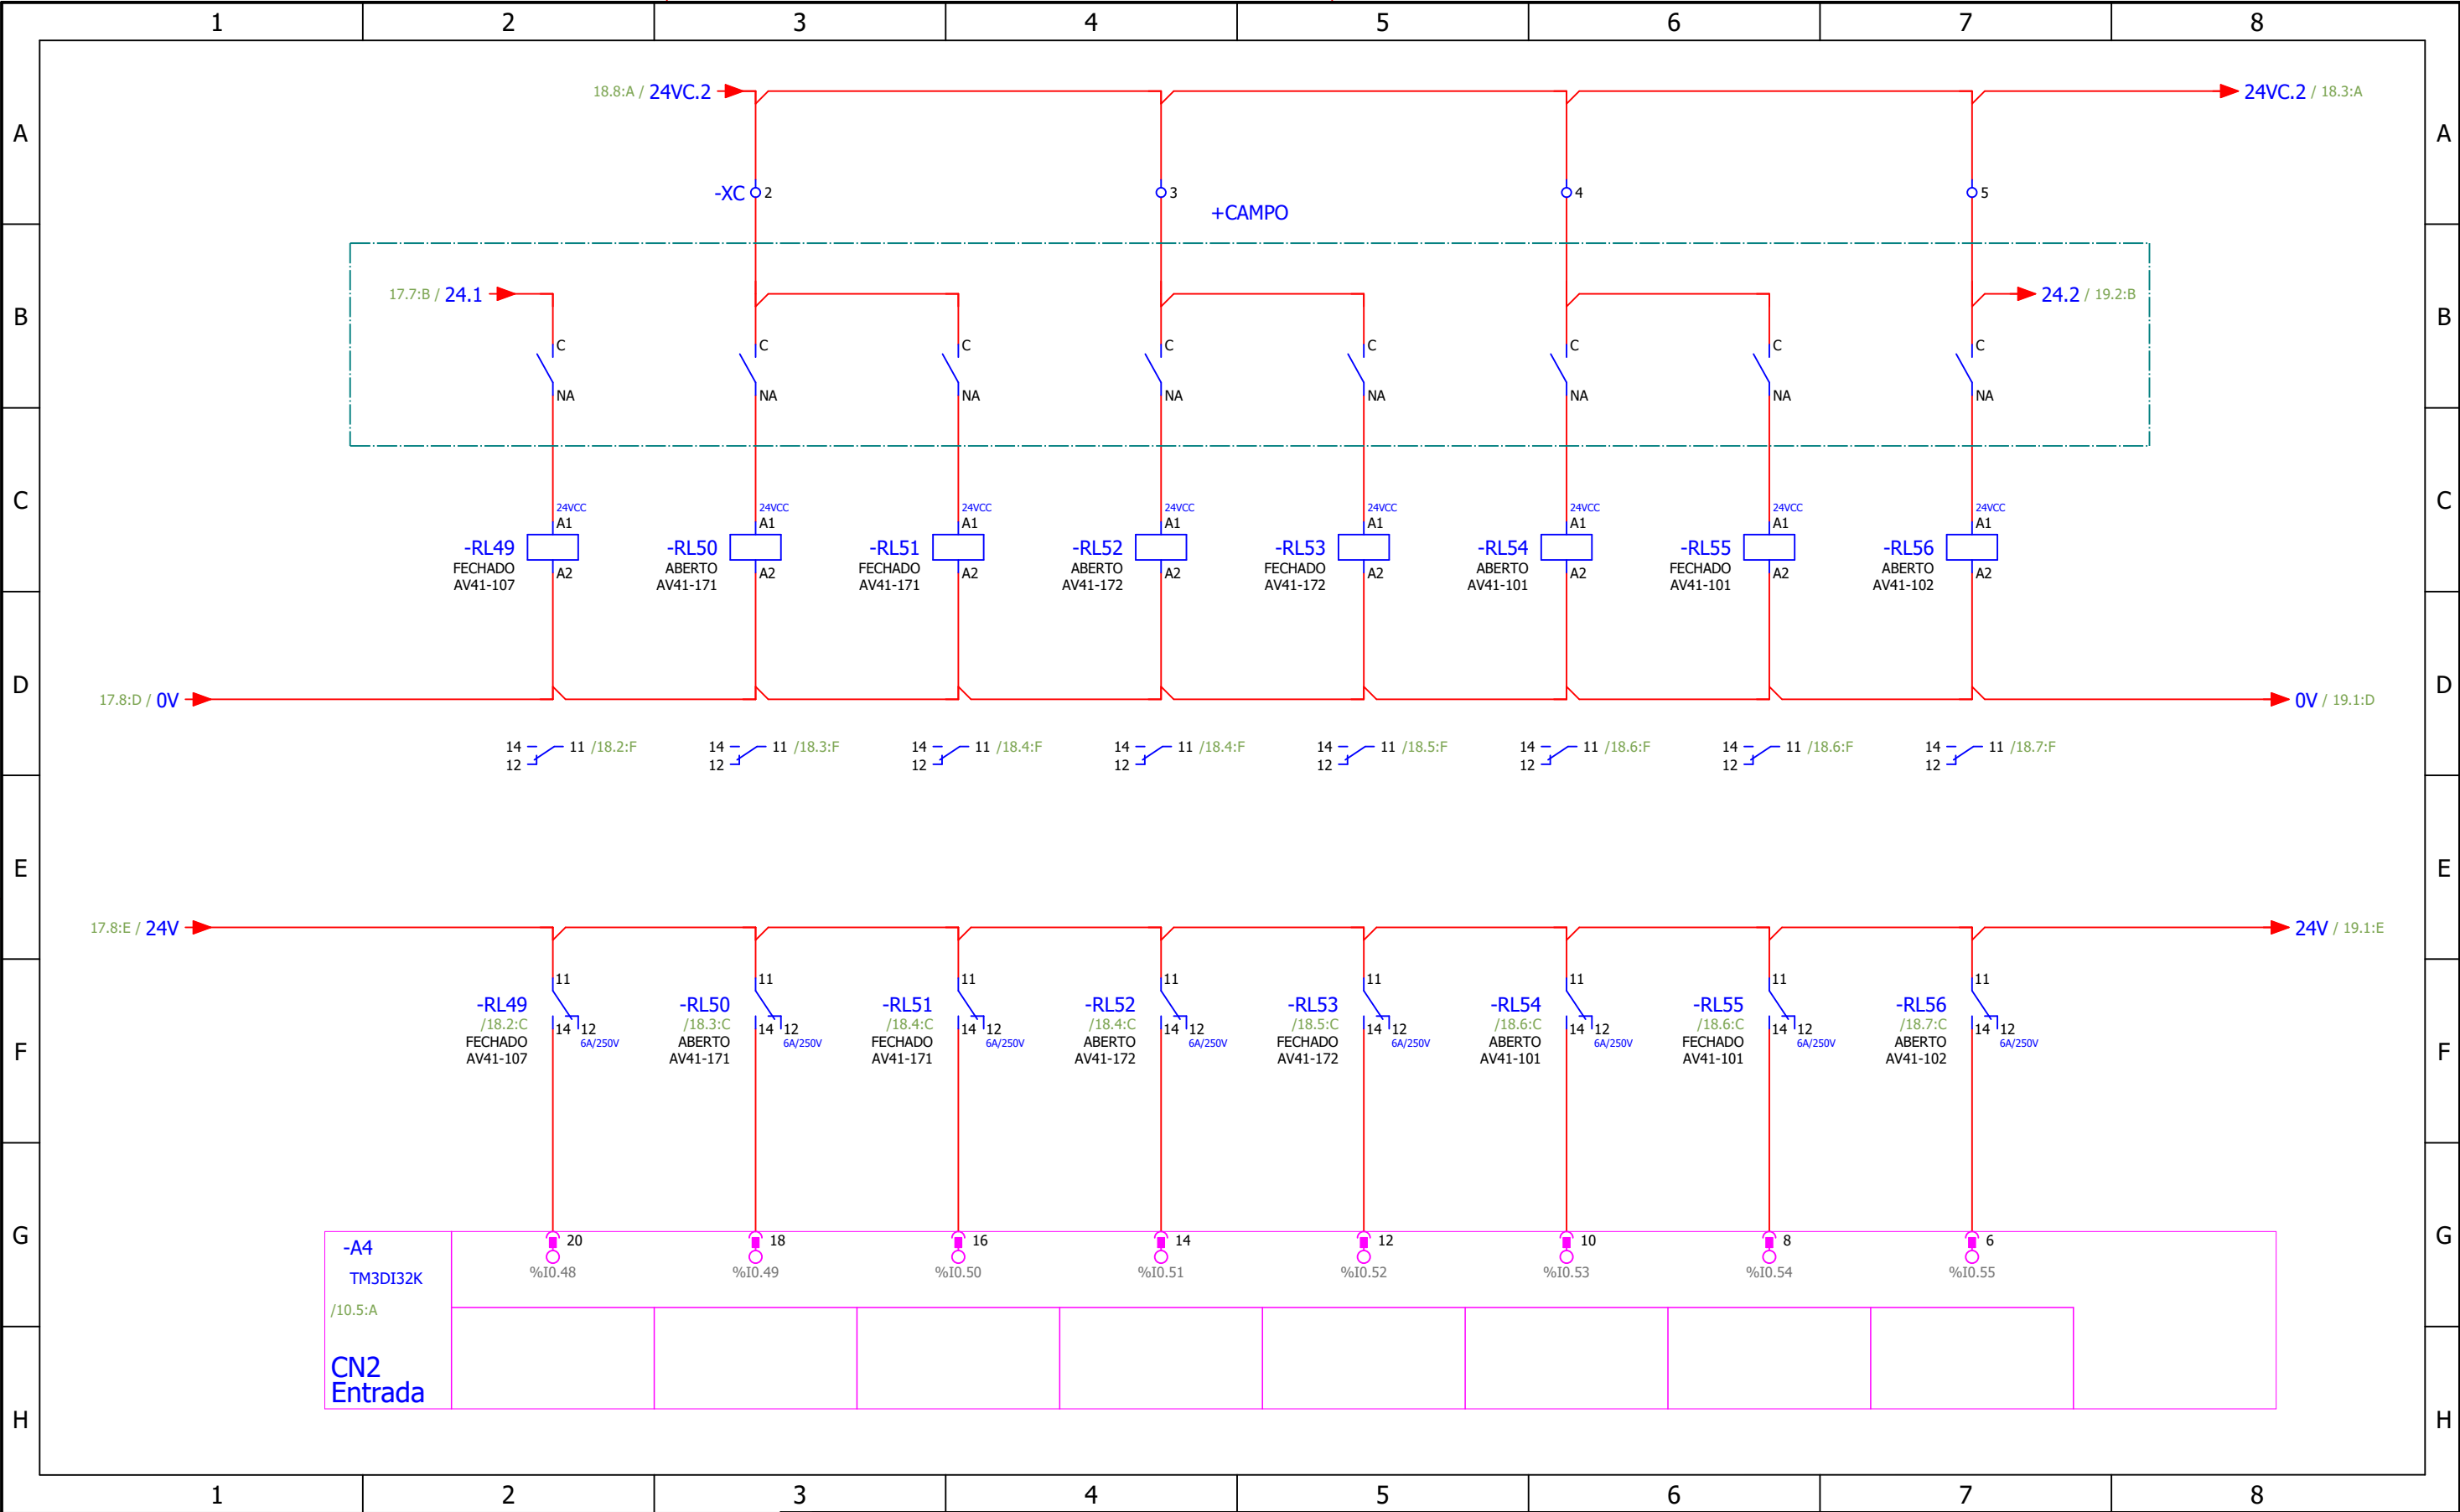



FOLHA: 18 / 58		LEGENDA:							TÍTULO: PCE NEREDA			
									SUB-TÍTULO: Entradas Digitais			
		REVISÃO:		EI						UNID. BRK: SUMARÉ	MUNIC./EST.: SUMARÉ-SP	BAIRRO/ÁREA:
		DATA:		03/06/2025						RESP. TÊC.: JEAN CARLOS ESSER 076760-0/SC	APROVAÇÃO BRK AMBIENTAL:	APROVAÇÃO CLIENTE: BRK
		EXECUÇÃO:		Luiz Corrêa				CONTRATANTE: BRK AMBIENTAL	CONTRATO Nº: 230317	CÓDIGO DO PROJETO: HID-PA-DE-ETE-ELQ-005		ESCALA: 1:1
		VERIFICAÇÃO:		Luiz Corrêa								
		APROVAÇÃO:		Rafael Decker								

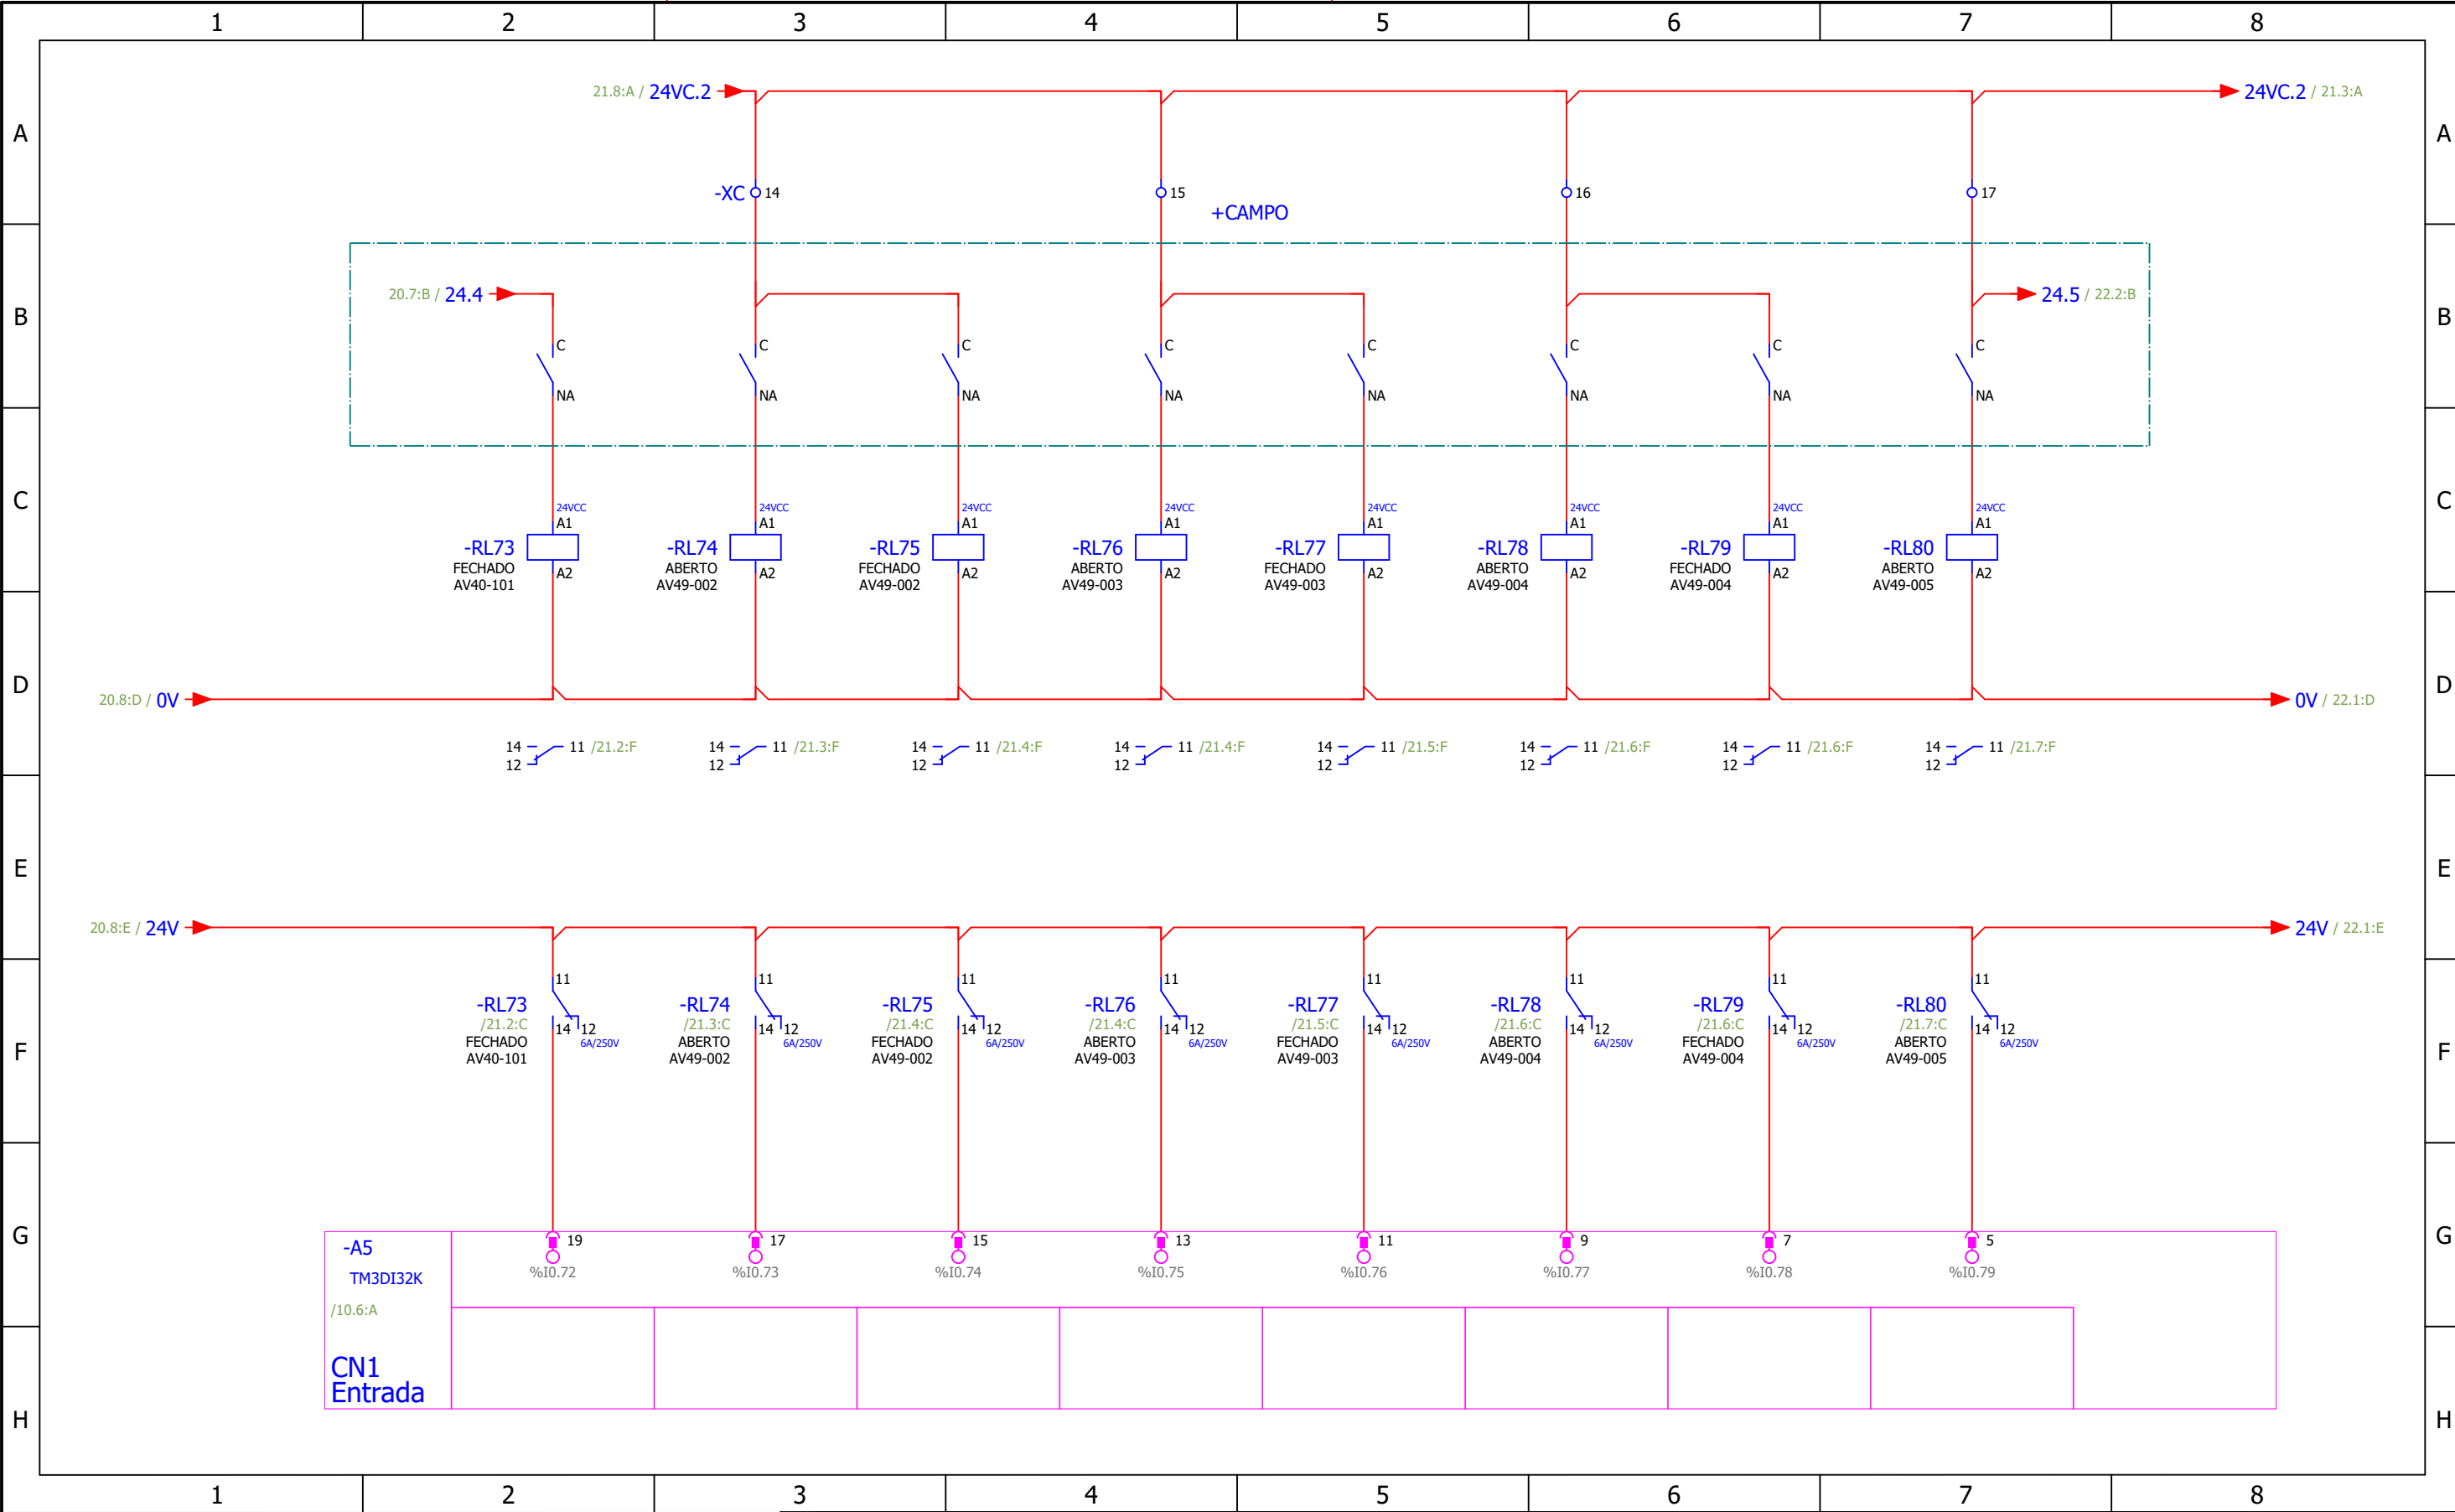


FOLHA: 21 / 58		LEGENDA:						TÍTULO: PCE NEREDA							
								SUB-TÍTULO: Entradas Digitais							
		REVISÃO:	EI						UNID. BRK:	SUMARÉ	MUNIC./EST.:	SUMARÉ-SP	BAIRRO/ÁREA:		
		DATA:	03/06/2025						RESP. TÊC.:	JEAN CARLOS ESSER	APROVAÇÃO BRK AMBIENTAL:		APROVAÇÃO CLIENTE:		
		EXECUÇÃO:	Luiz Corrêa						CREA:	076760-0/SC					
VERIFICAÇÃO:	Luiz Corrêa				CONTRATANTE:		CONTRATO Nº:		CÓDIGO DO PROJETO:						
		APROVAÇÃO:	Rafael Decker				BRK AMBIENTAL	230317	HID-PA-DE-ETE-ELQ-005			ESCALA:	1:1	REVISÃO:	EI

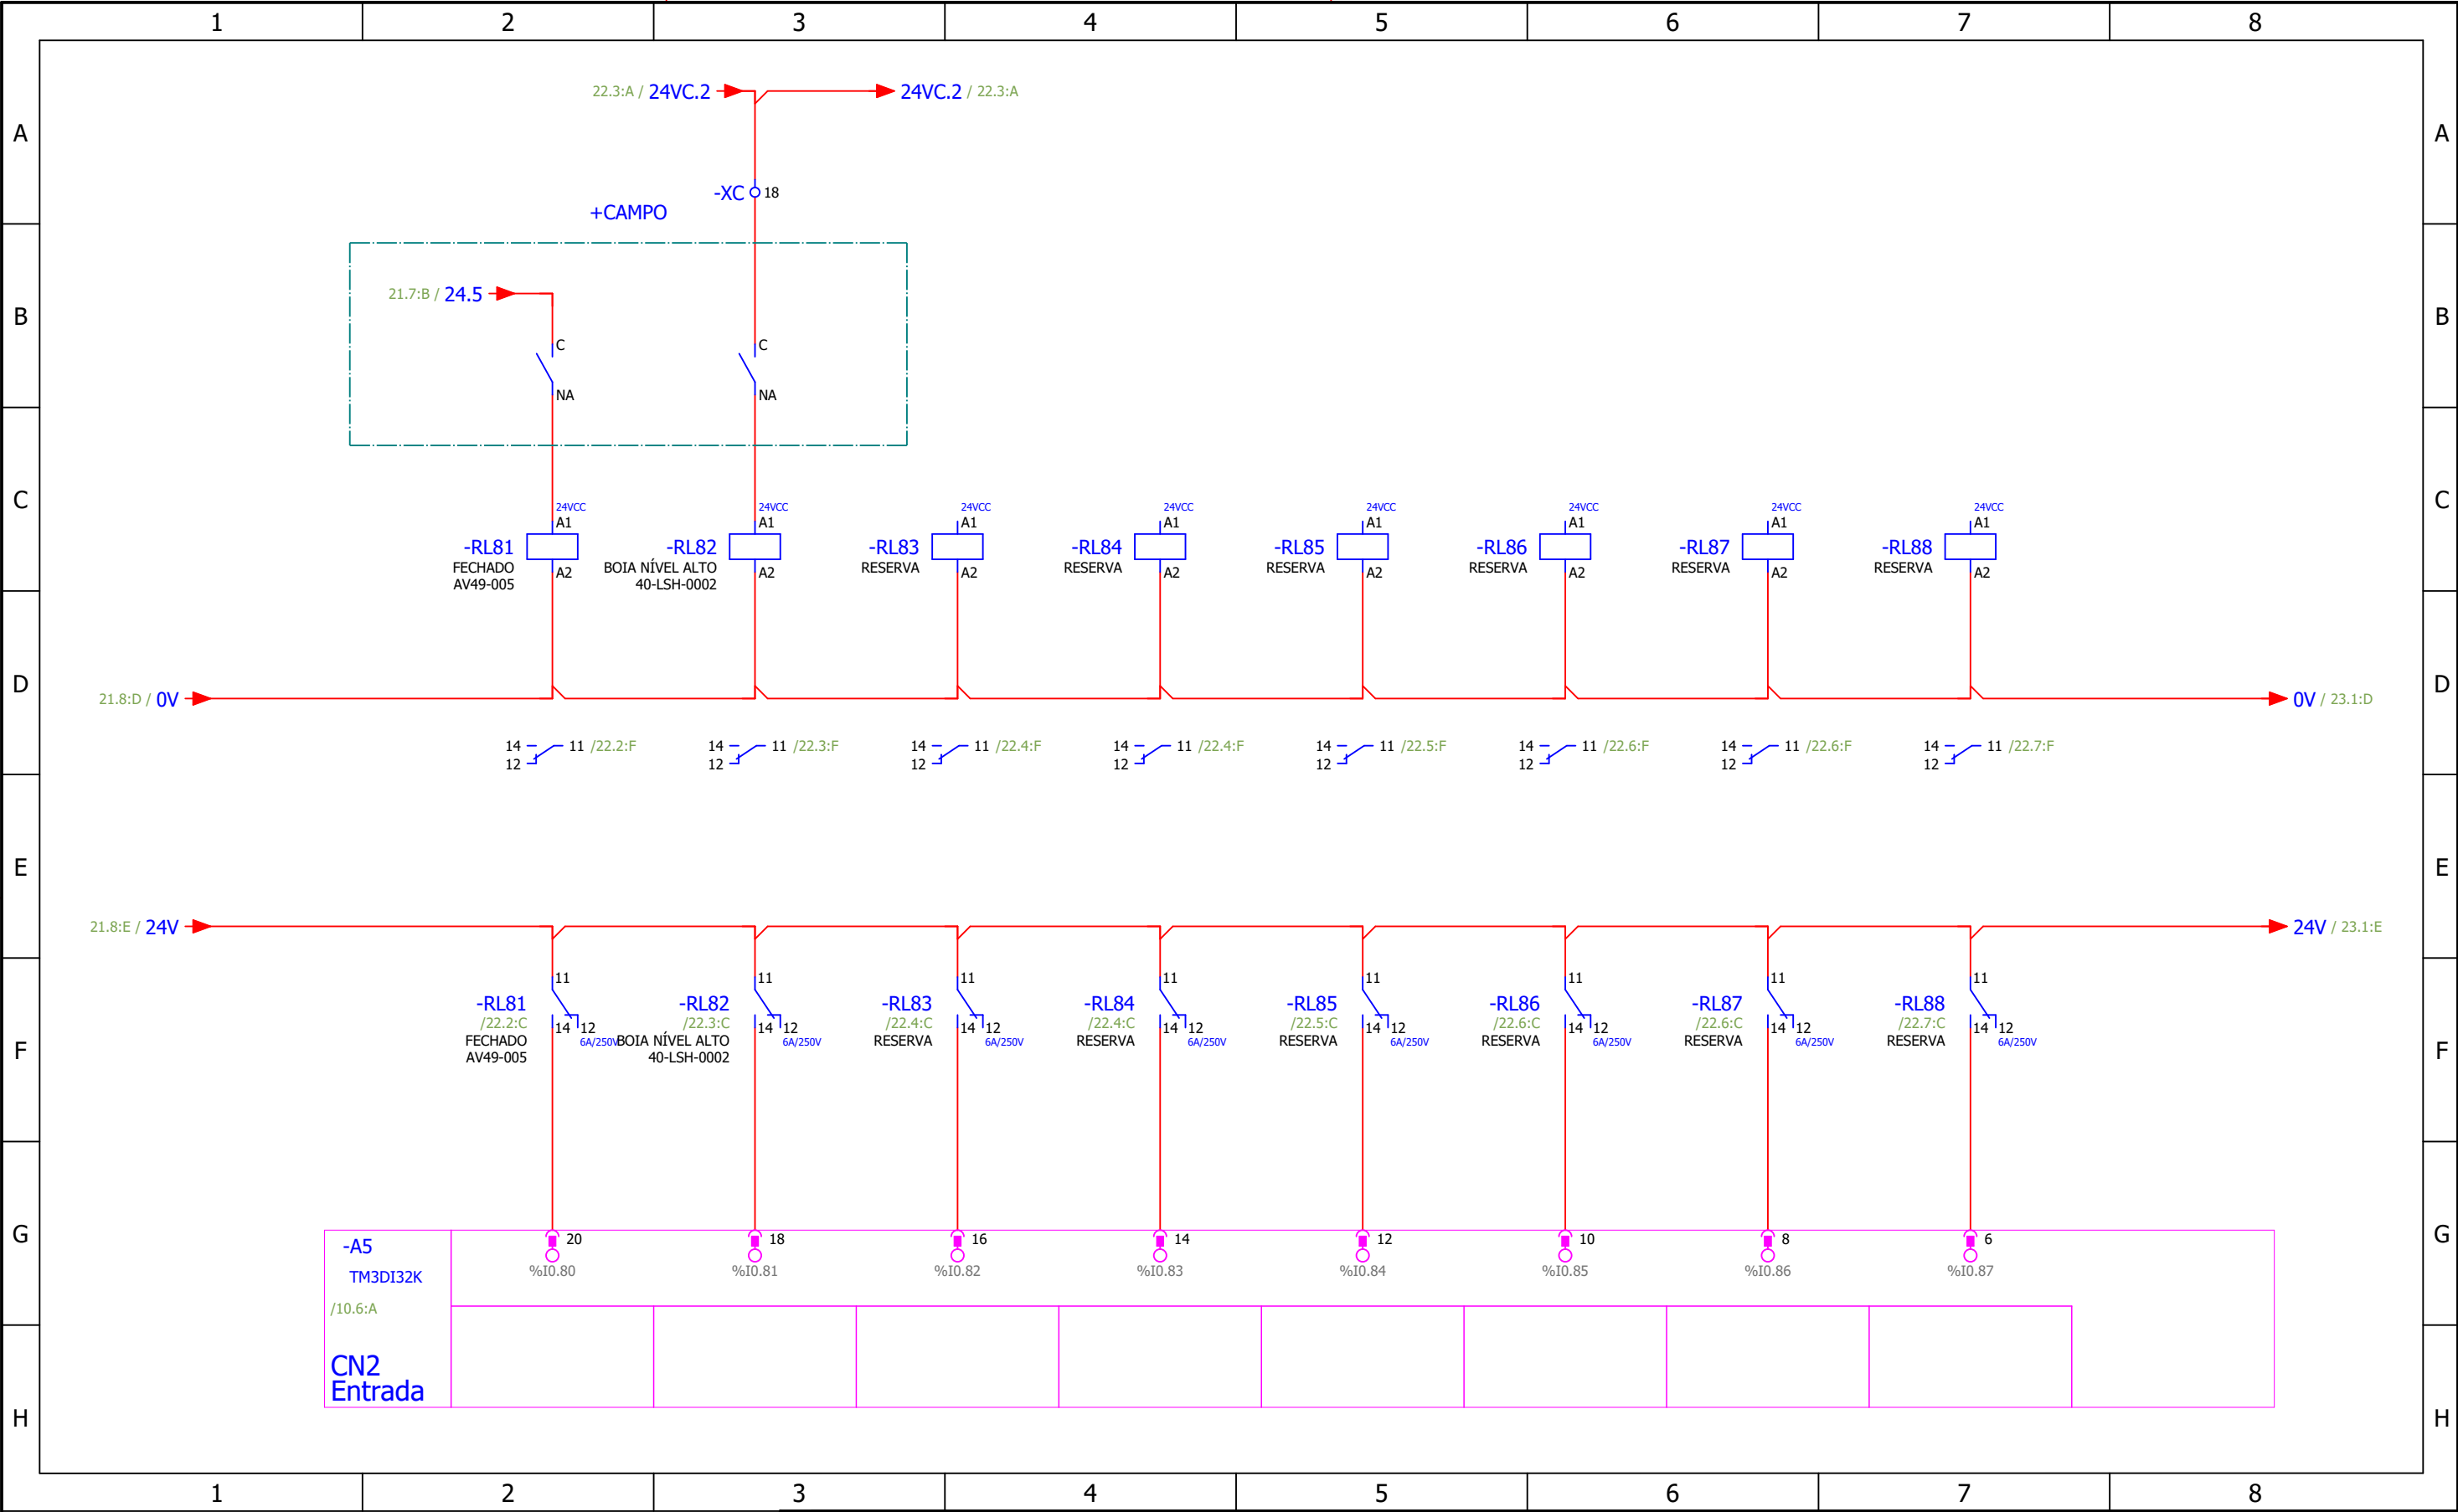


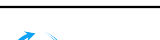
FOLHA: 22 / 58		LEGENDA:							TÍTULO: PCE NEREDA				
									SUB-TÍTULO: Entradas Digitais				
		REVISÃO:		EI						UNID. BRK: SUMARÉ	MUNIC./EST.: SUMARÉ-SP	BAIRRO/ÁREA:	
		DATA:		03/06/2025						RESP. TÊC.: JEAN CARLOS ESSER 076760-0/SC	APROVAÇÃO BRK AMBIENTAL:	APROVAÇÃO CLIENTE: BRK	
		EXECUÇÃO:		Luiz Corrêa									
		VERIFICAÇÃO:		Luiz Corrêa				CÓDIGO DO PROJETO: HID-PA-DE-ETE-ELQ-005			ESCALA: 1:1	REVISÃO: EI	
		APROVAÇÃO:		Rafael Decker				CONTRATANTE: BRK AMBIENTAL	CONTRATO Nº: 230317				

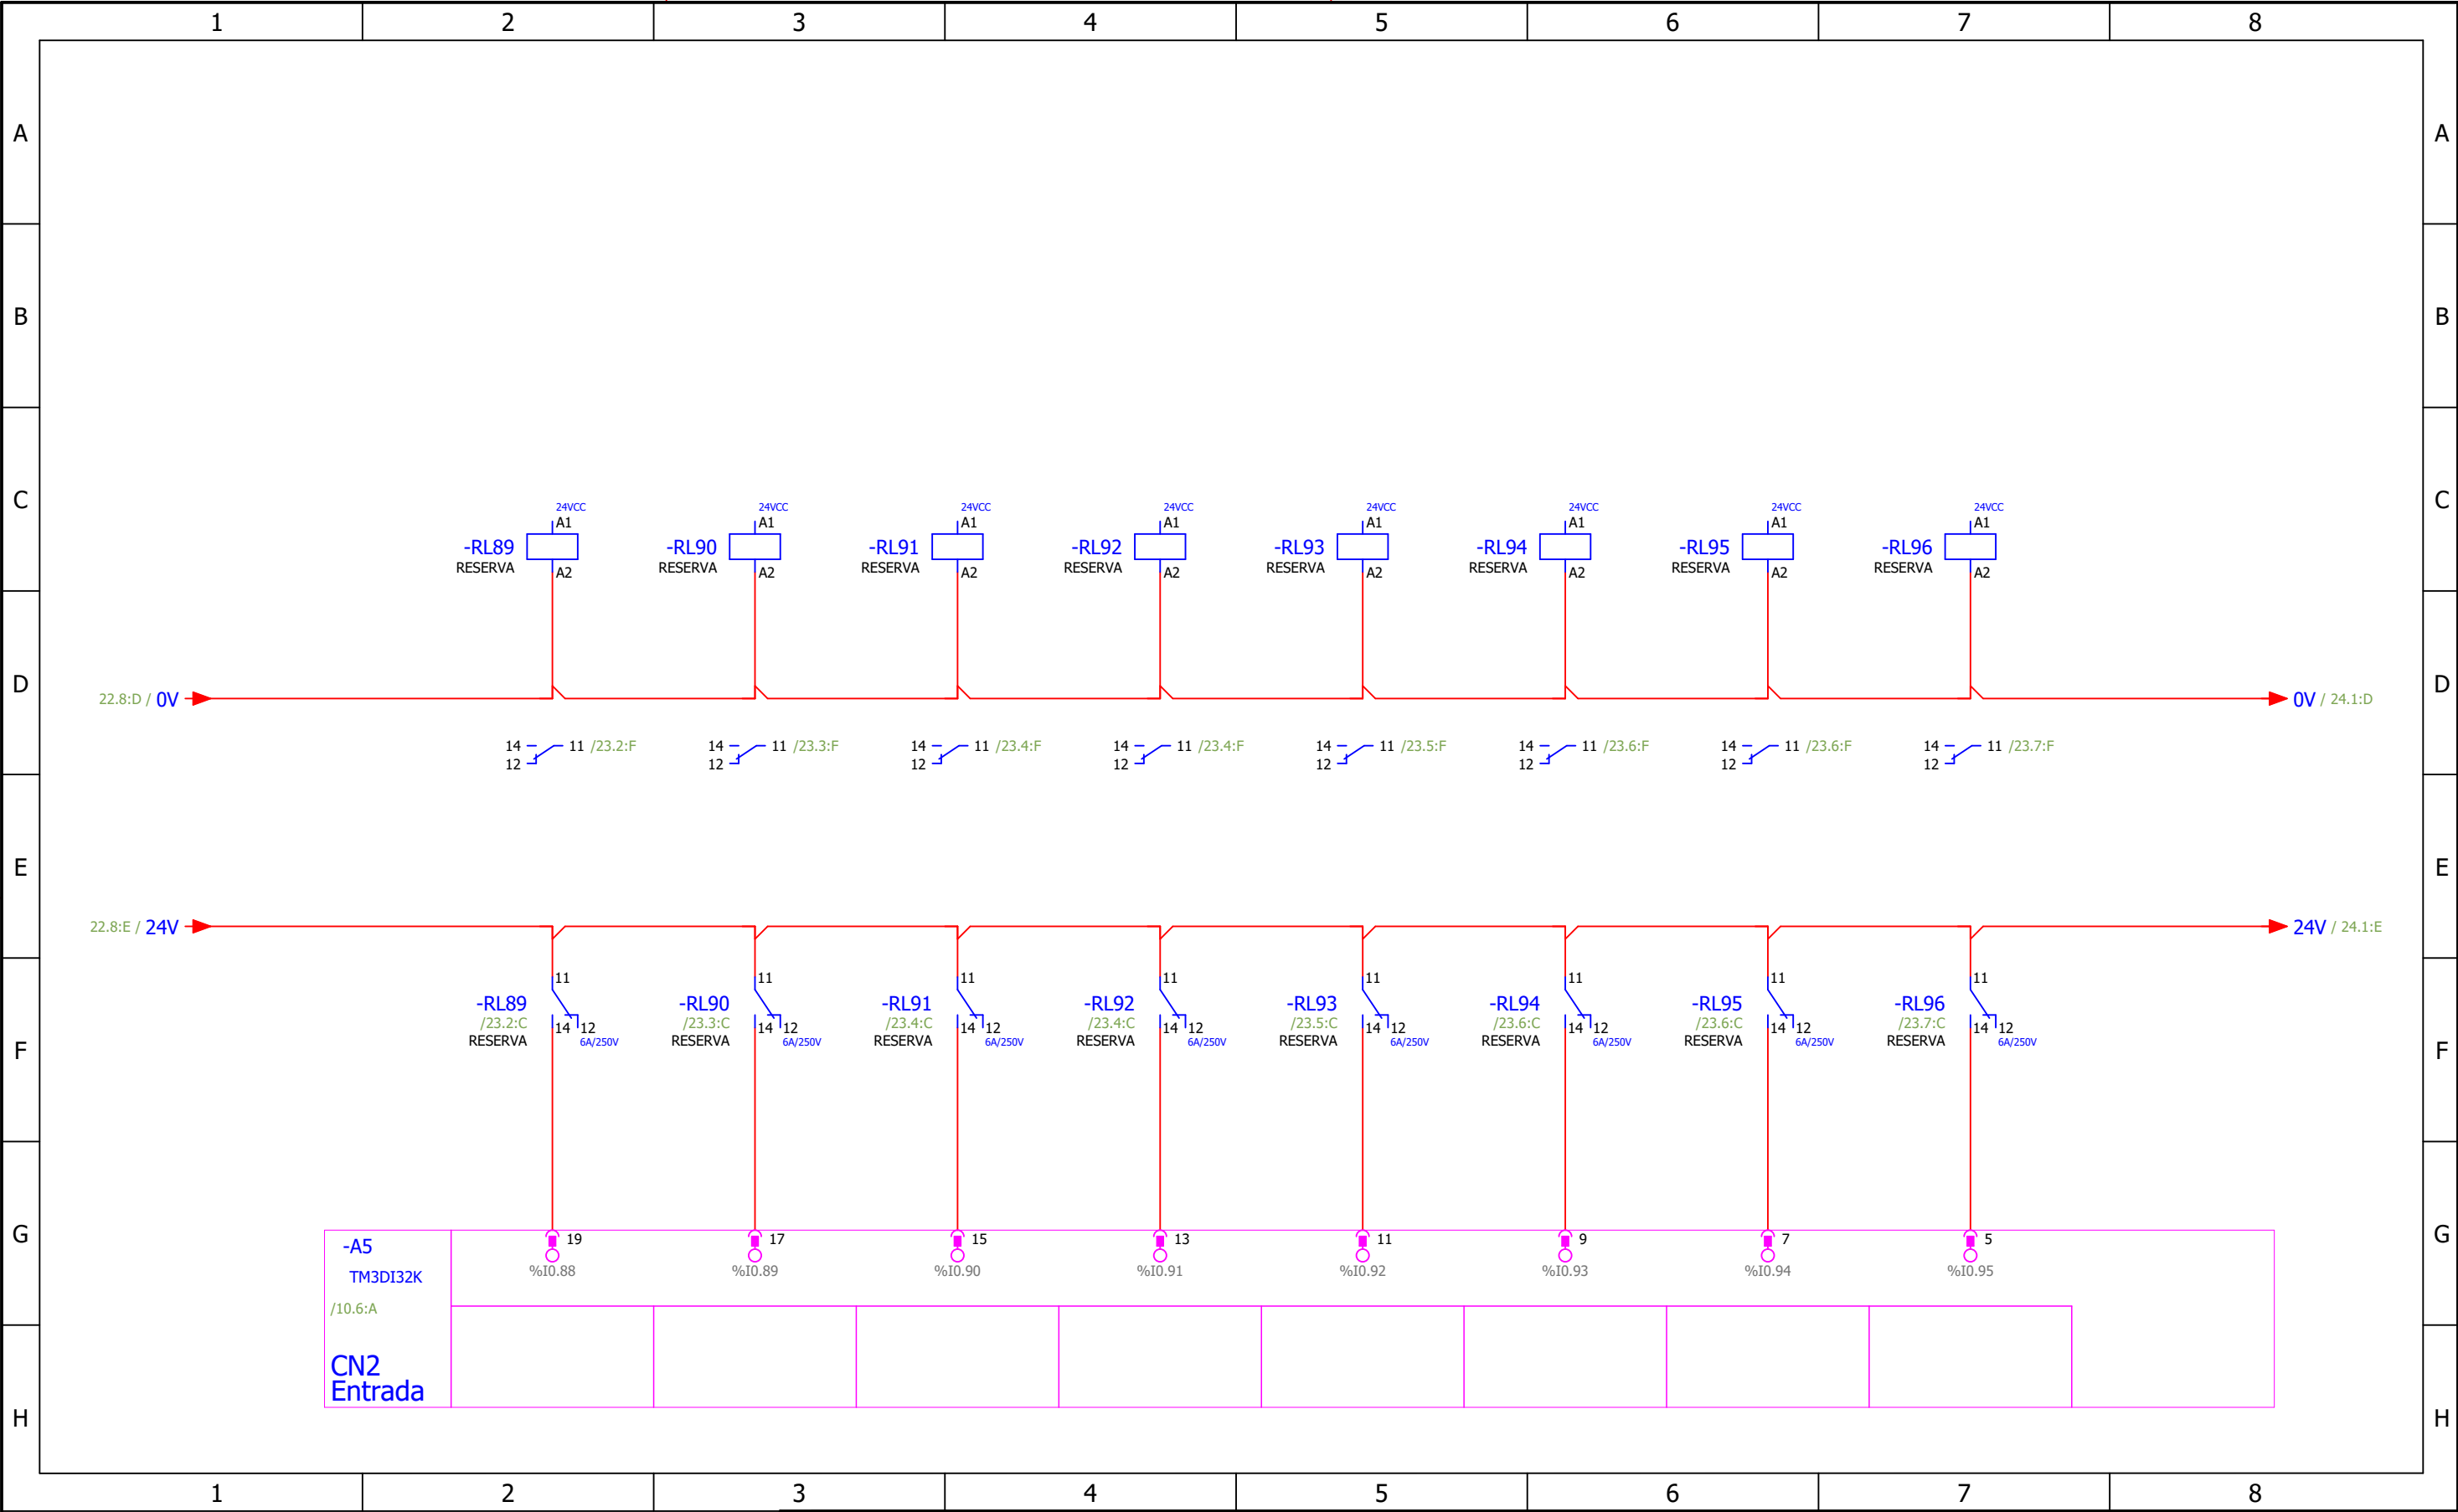



FOLHA: 23 / 58	LEGENDA:						TÍTULO: PCE NEREDA		
							SUB-TÍTULO: Entradas Digitais		
							UNID. BRK:	MUNIC./EST.:	BAIRRO/ÁREA:
							SUMARÉ	SUMARÉ-SP	
			REVISÃO:	EI			RESP. TÍC.: JEAN CARLOS ESSER	APROVAÇÃO BRK AMBIENTAL:	APROVAÇÃO CLIENTE:
			DATA:	03/06/2025			076760-0/SC		BRK
			EXECUÇÃO:	Luiz Corrêa			CREA:		
			VERIFICAÇÃO:	Luiz Corrêa			CÓDIGO DO PROJETO:	ESCALA:	REVISÃO:
			APROVAÇÃO:	Rafael Decker			HID-PA-DE-ETE-ELQ-005	1:1	EI
			CONTRATANTE:	BRK AMBIENTAL			CONTRATO Nº:		
							230317		

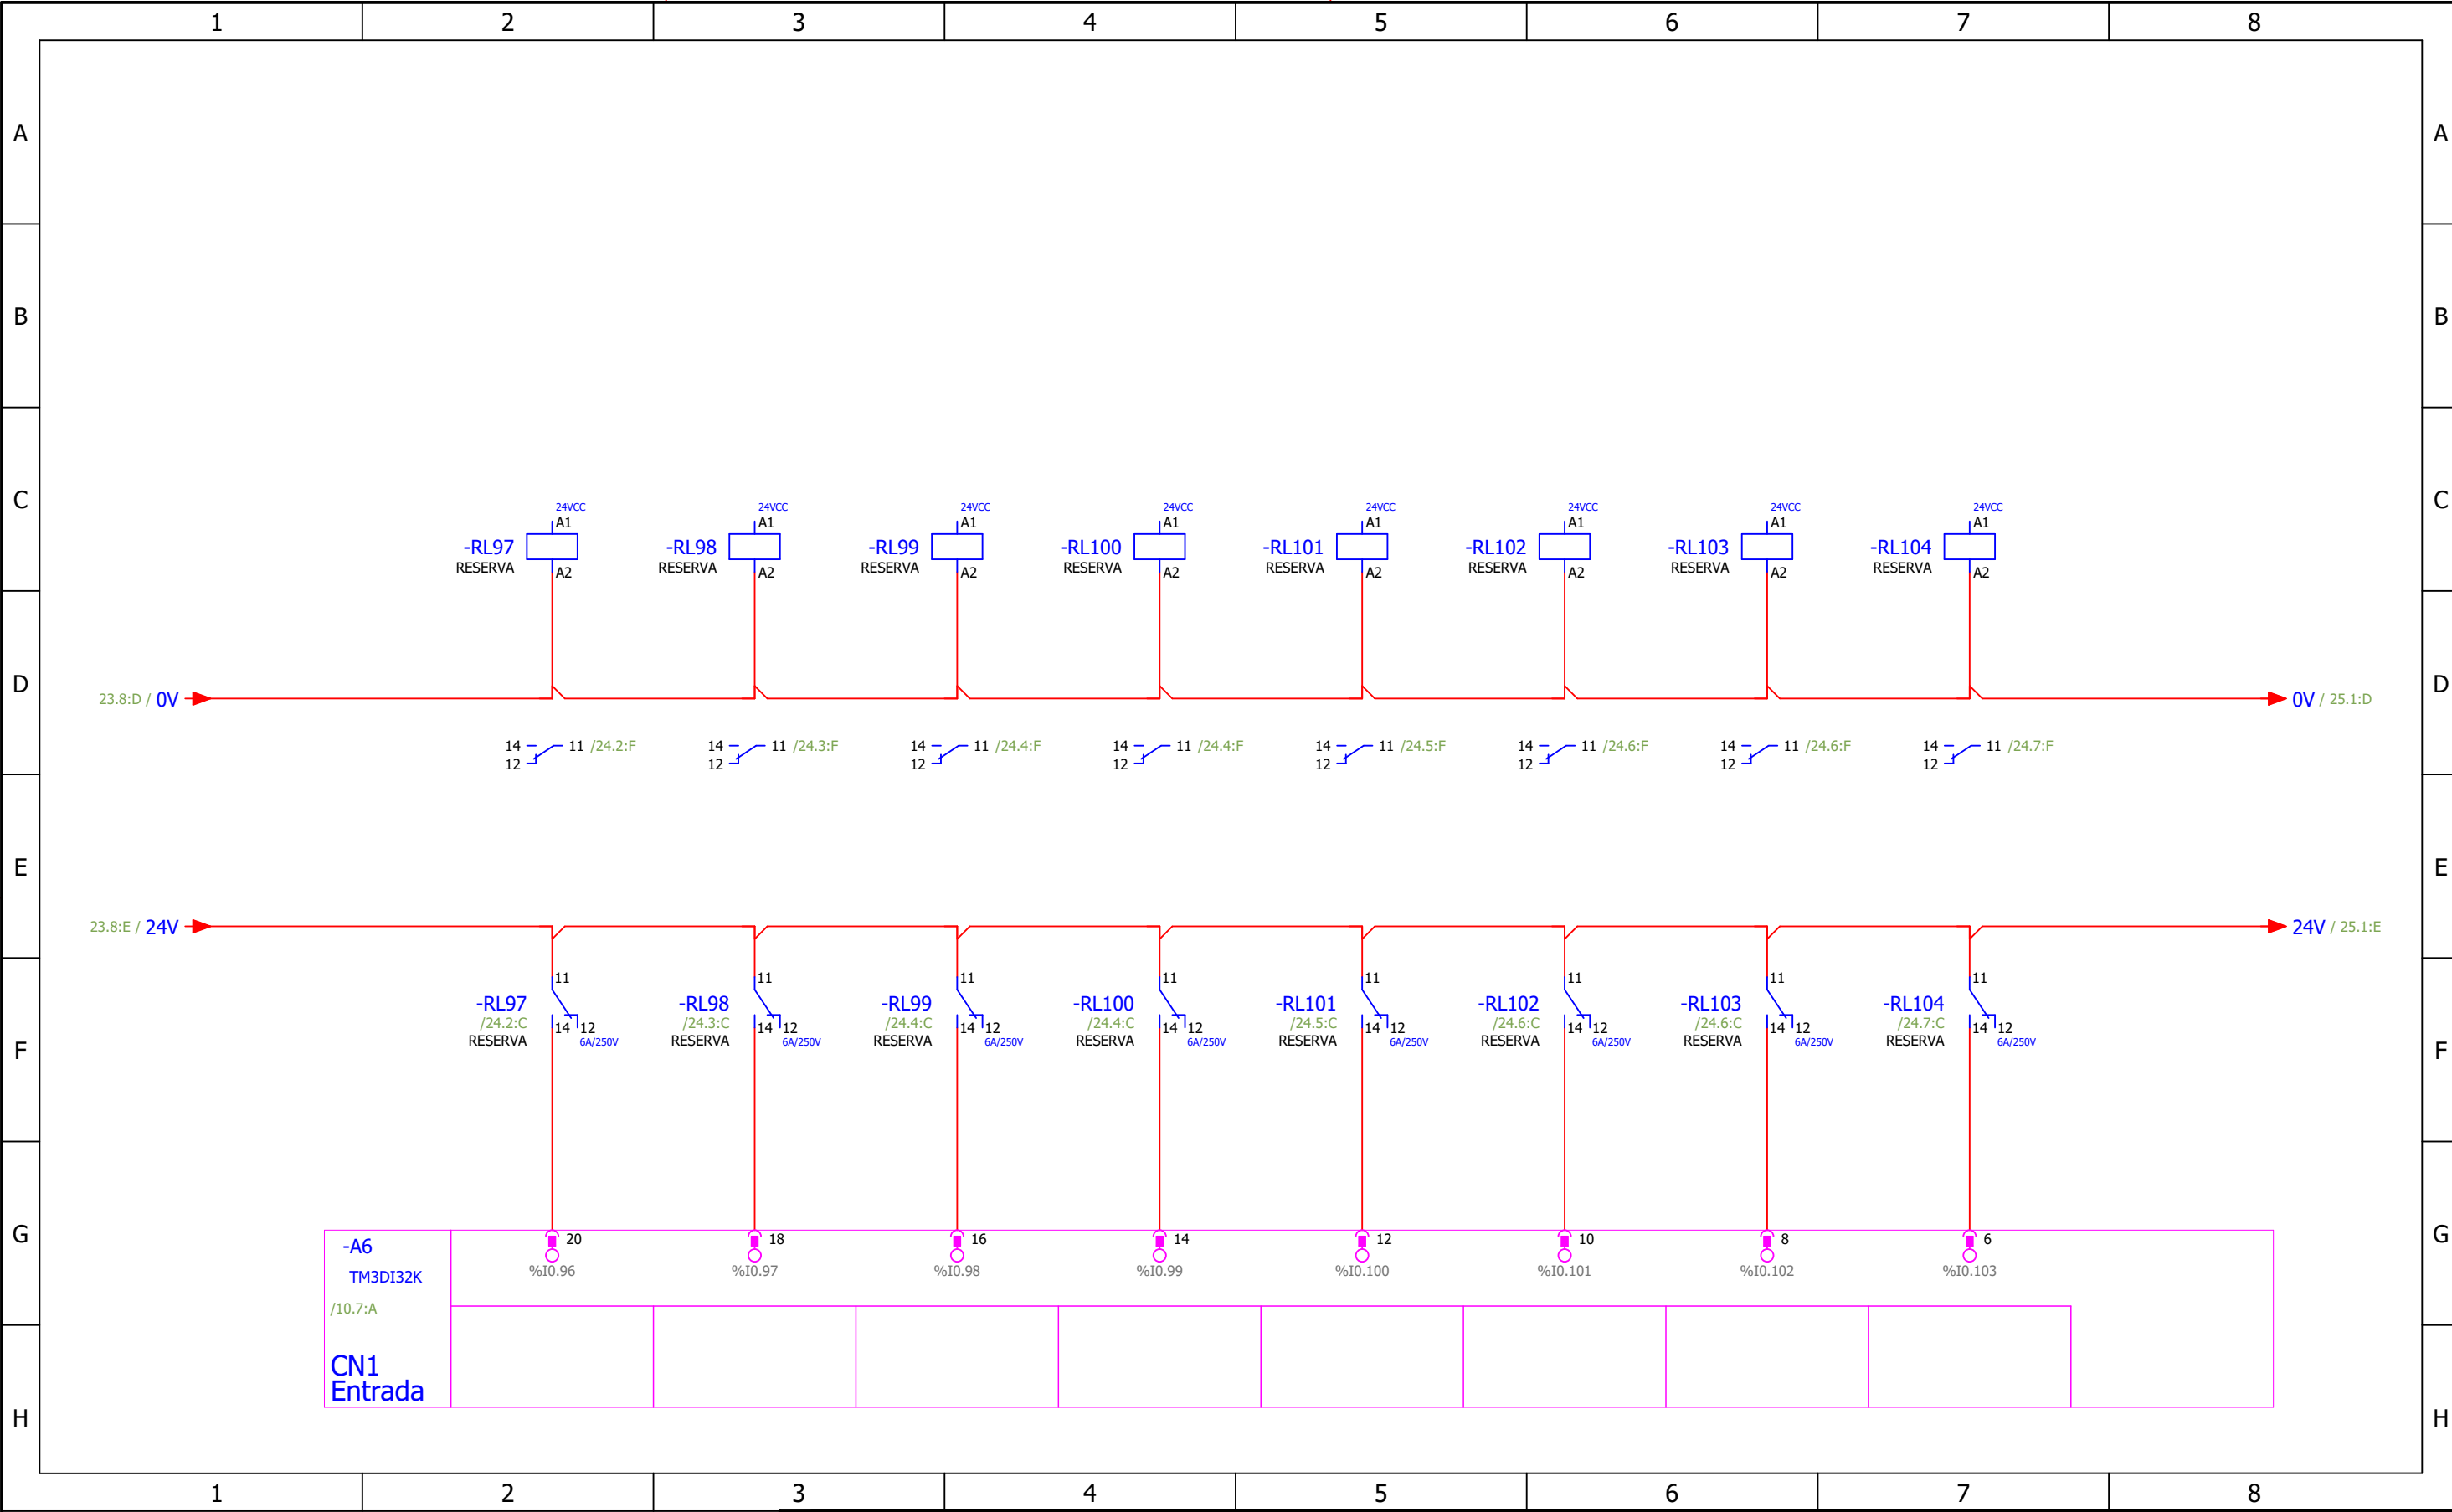

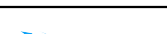
FOLHA: 24 / 58		LEGENDA:							TÍTULO: PCE NEREDA							
									SUB-TÍTULO: Entradas Digitais							
		REVISÃO:		EI							UNID. BRK: SUMARÉ		MUNIC./EST.: SUMARÉ-SP		BAIRRO/ÁREA:	
		DATA:		03/06/2025							RESP. TÊC.: JEAN CARLOS ESSER 076760-0/SC		APROVAÇÃO BRK AMBIENTAL:		APROVAÇÃO CLIENTE: BRK	
		EXECUÇÃO:		Luiz Corrêa							CREA:					
VERIFICAÇÃO:		Luiz Corrêa					CONTRATANTE: BRK AMBIENTAL				CONTRATO Nº: 230317		CÓDIGO DO PROJETO: HID-PA-DE-ETE-ELQ-005		ESCALA: 1:1	
		APROVAÇÃO:		Rafael Decker												

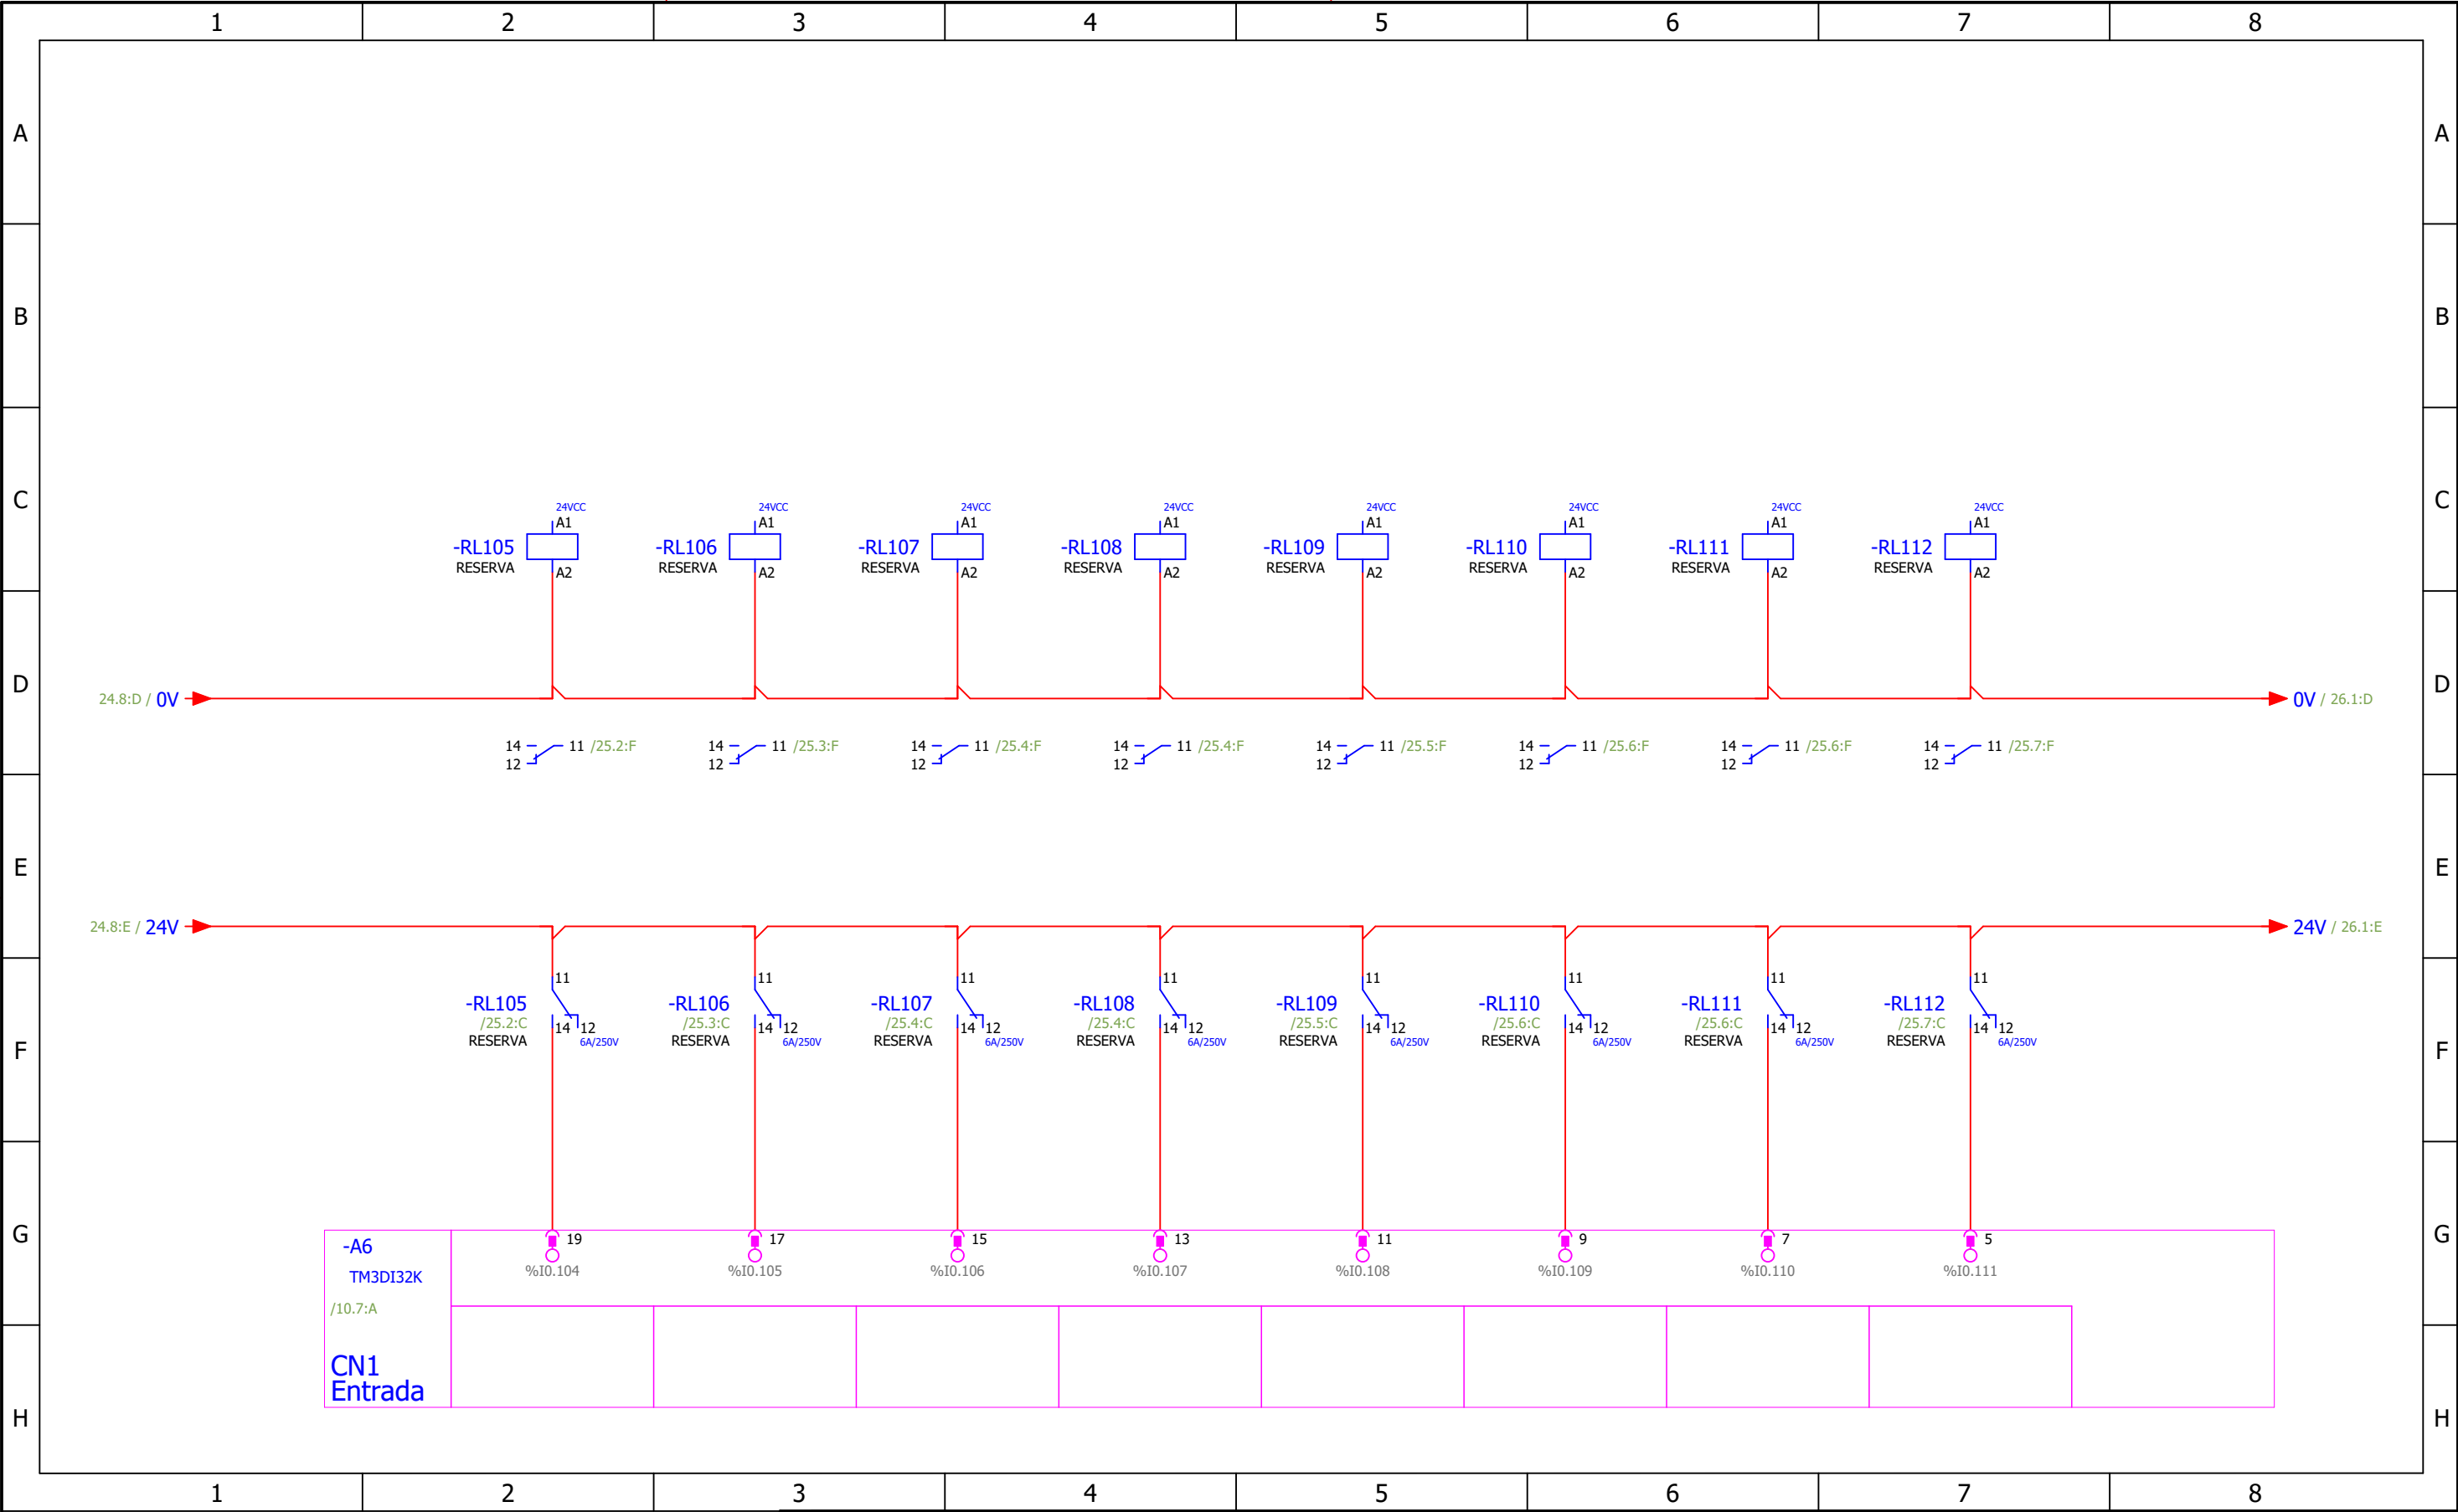

 
FOLHA: 25 / 58		LEGENDA:							TÍTULO: PCE NEREDA							
									SUB-TÍTULO: Entradas Digitais							
		REVISÃO:		EI						UNID. BRK: SUMARÉ		MUNIC./EST.: SUMARÉ-SP		BAIRRO/ÁREA:		
		DATA:		03/06/2025						RESP. TÊC.: JEAN CARLOS ESSER 076760-0/SC		APROVAÇÃO BRK AMBIENTAL:		APROVAÇÃO CLIENTE: BRK		
		EXECUÇÃO:		Luiz Corrêa												
VERIFICAÇÃO:		Luiz Corrêa														
		APROVAÇÃO:		Rafael Decker				CONTRATANTE: BRK AMBIENTAL	CONTRATO Nº: 230317		CÓDIGO DO PROJETO: HID-PA-DE-ETE-ELQ-005				ESCALA: 1:1	REVISÃO: EI

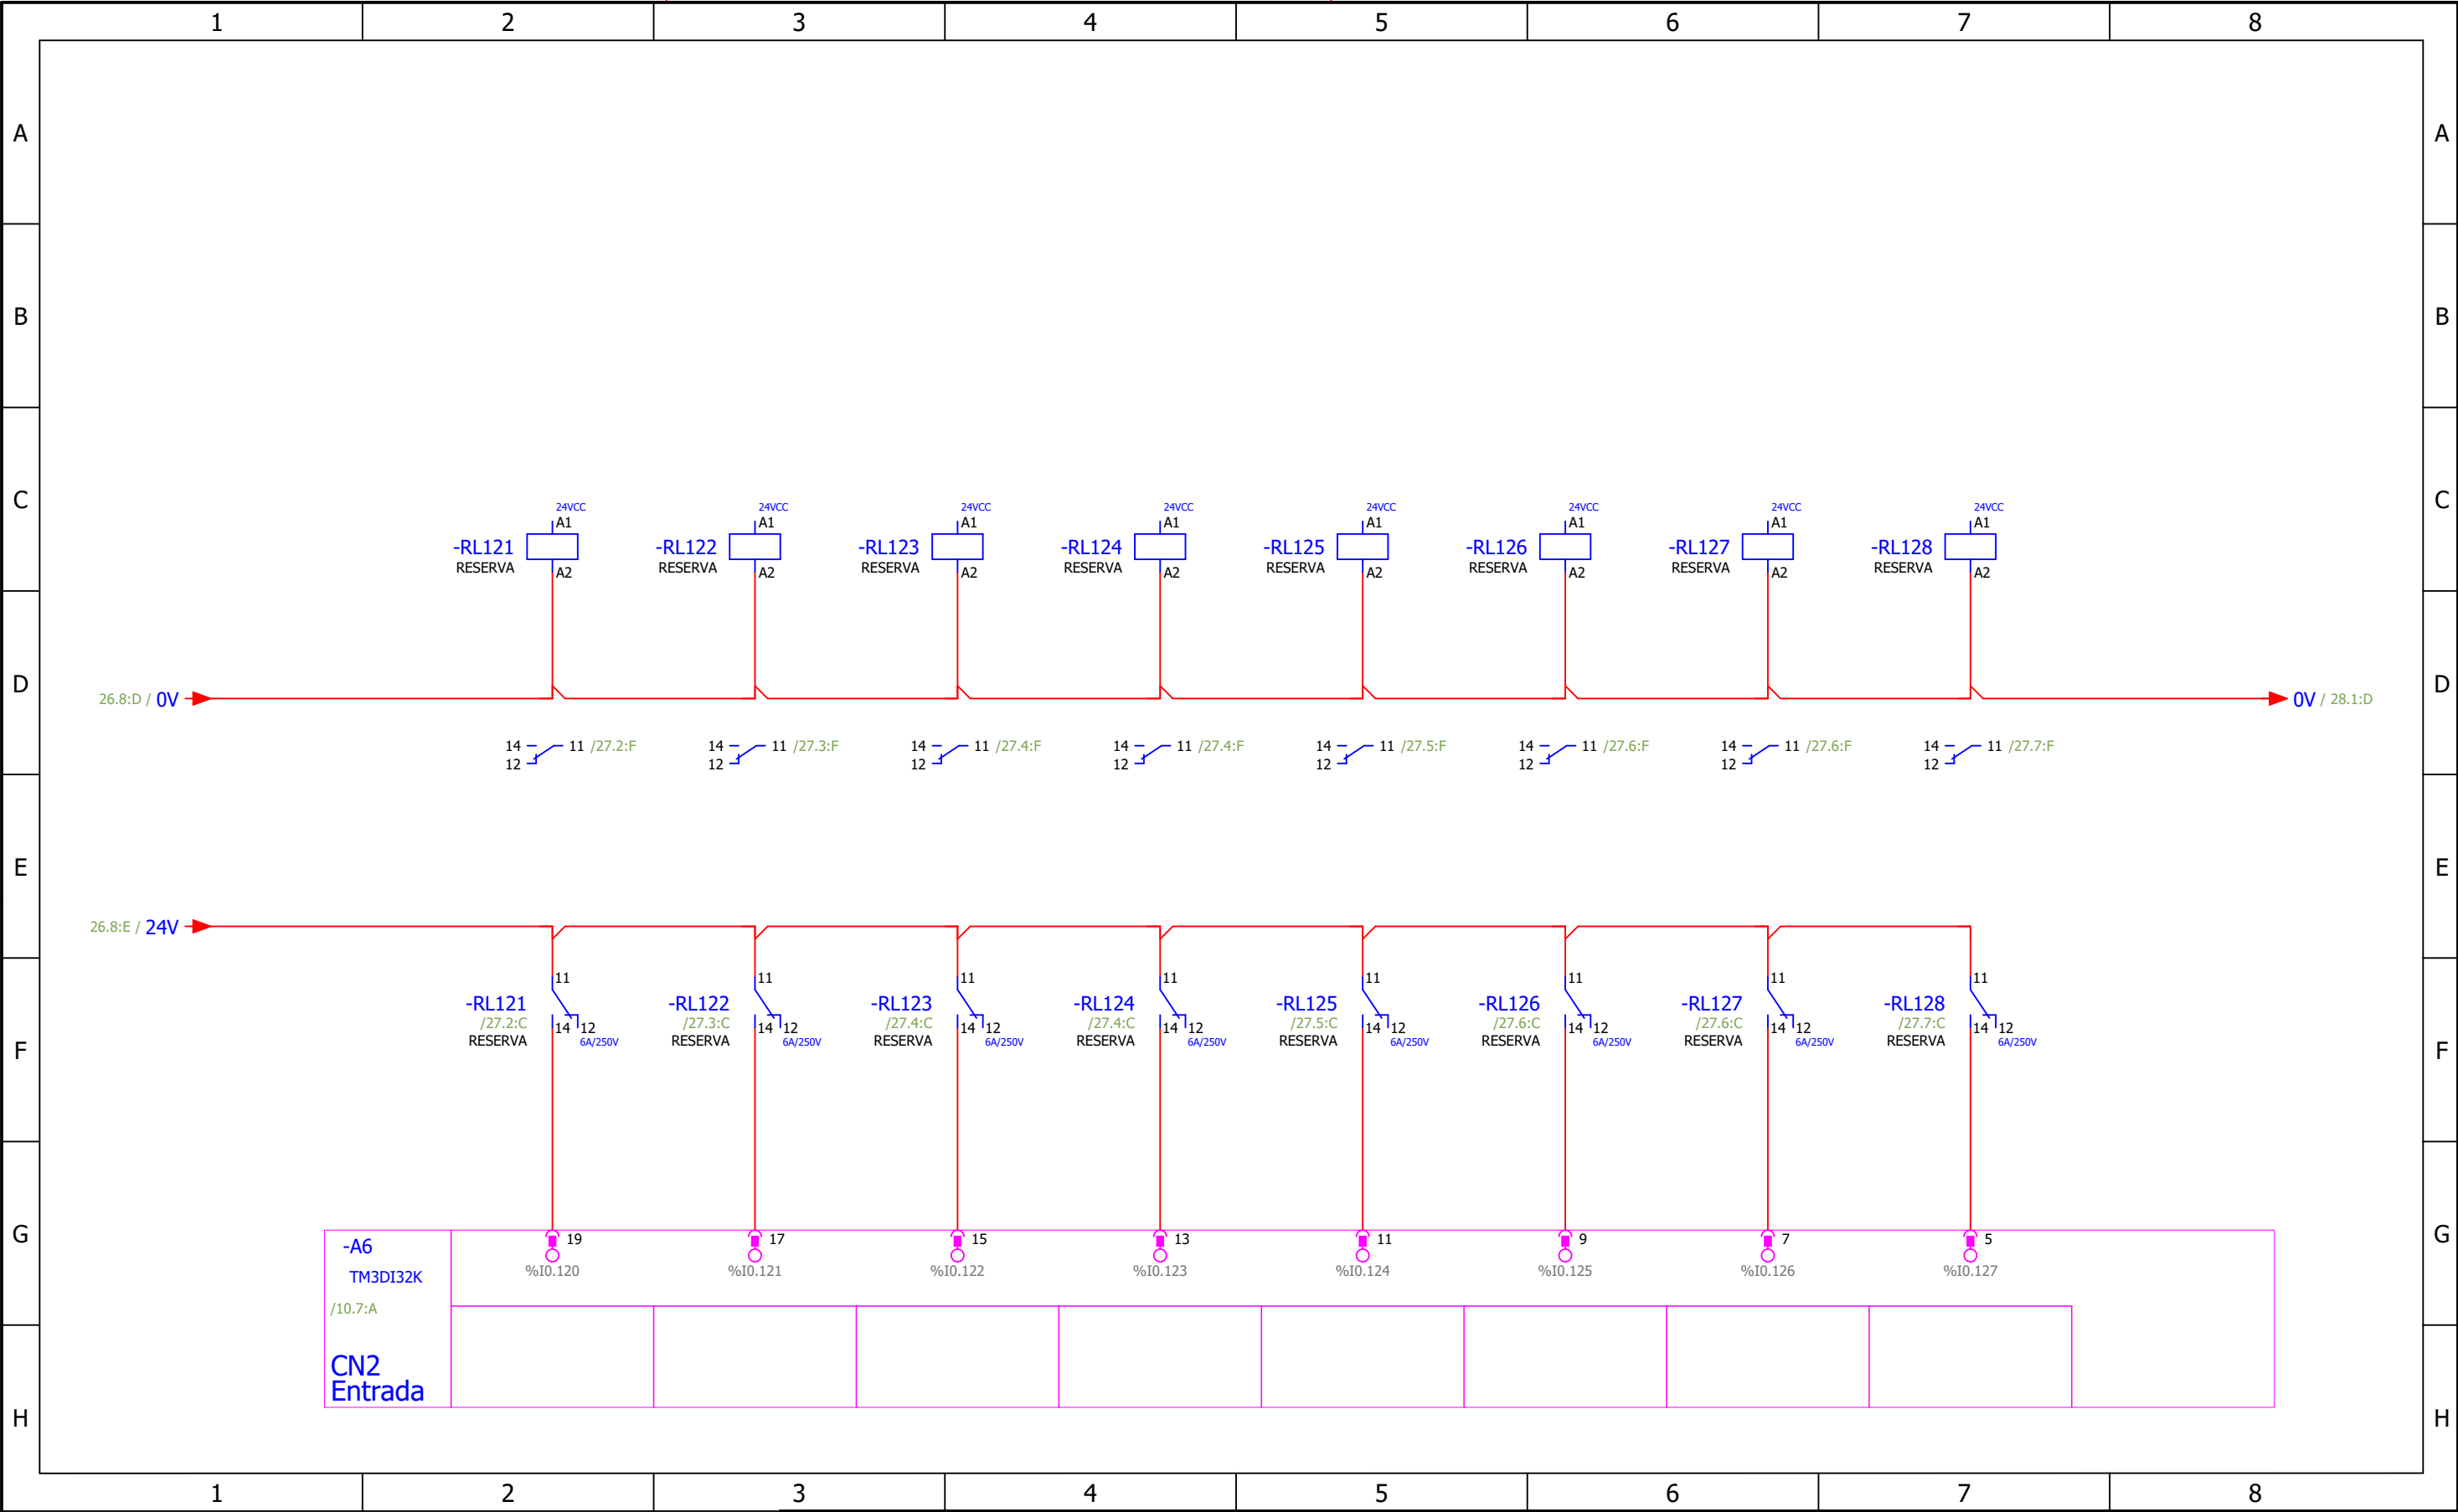



FOLHA: 27 / 58		LEGENDA:							TÍTULO: PCE NEREDA						
									SUB-TÍTULO: Entradas Digitais						
		REVISÃO:		EI						UNID. BRK: SUMARÉ		MUNIC./EST.: SUMARÉ-SP	BAIRRO/ÁREA:		
		DATA:		03/06/2025						RESP. TÊC.: JEAN CARLOS ESSER 076760-0/SC		APROVAÇÃO BRK AMBIENTAL:		APROVAÇÃO CLIENTE: BRK	
		EXECUÇÃO:		Luiz Corrêa						CÓDIGO DO PROJETO: HID-PA-DE-ETE-ELQ-005		ESCALA: 1:1		REVISÃO: EI	
		VERIFICAÇÃO:		Luiz Corrêa				CONTRATANTE: BRK AMBIENTAL		CONTRATO Nº: 230317					
		APROVAÇÃO:		Rafael Decker											

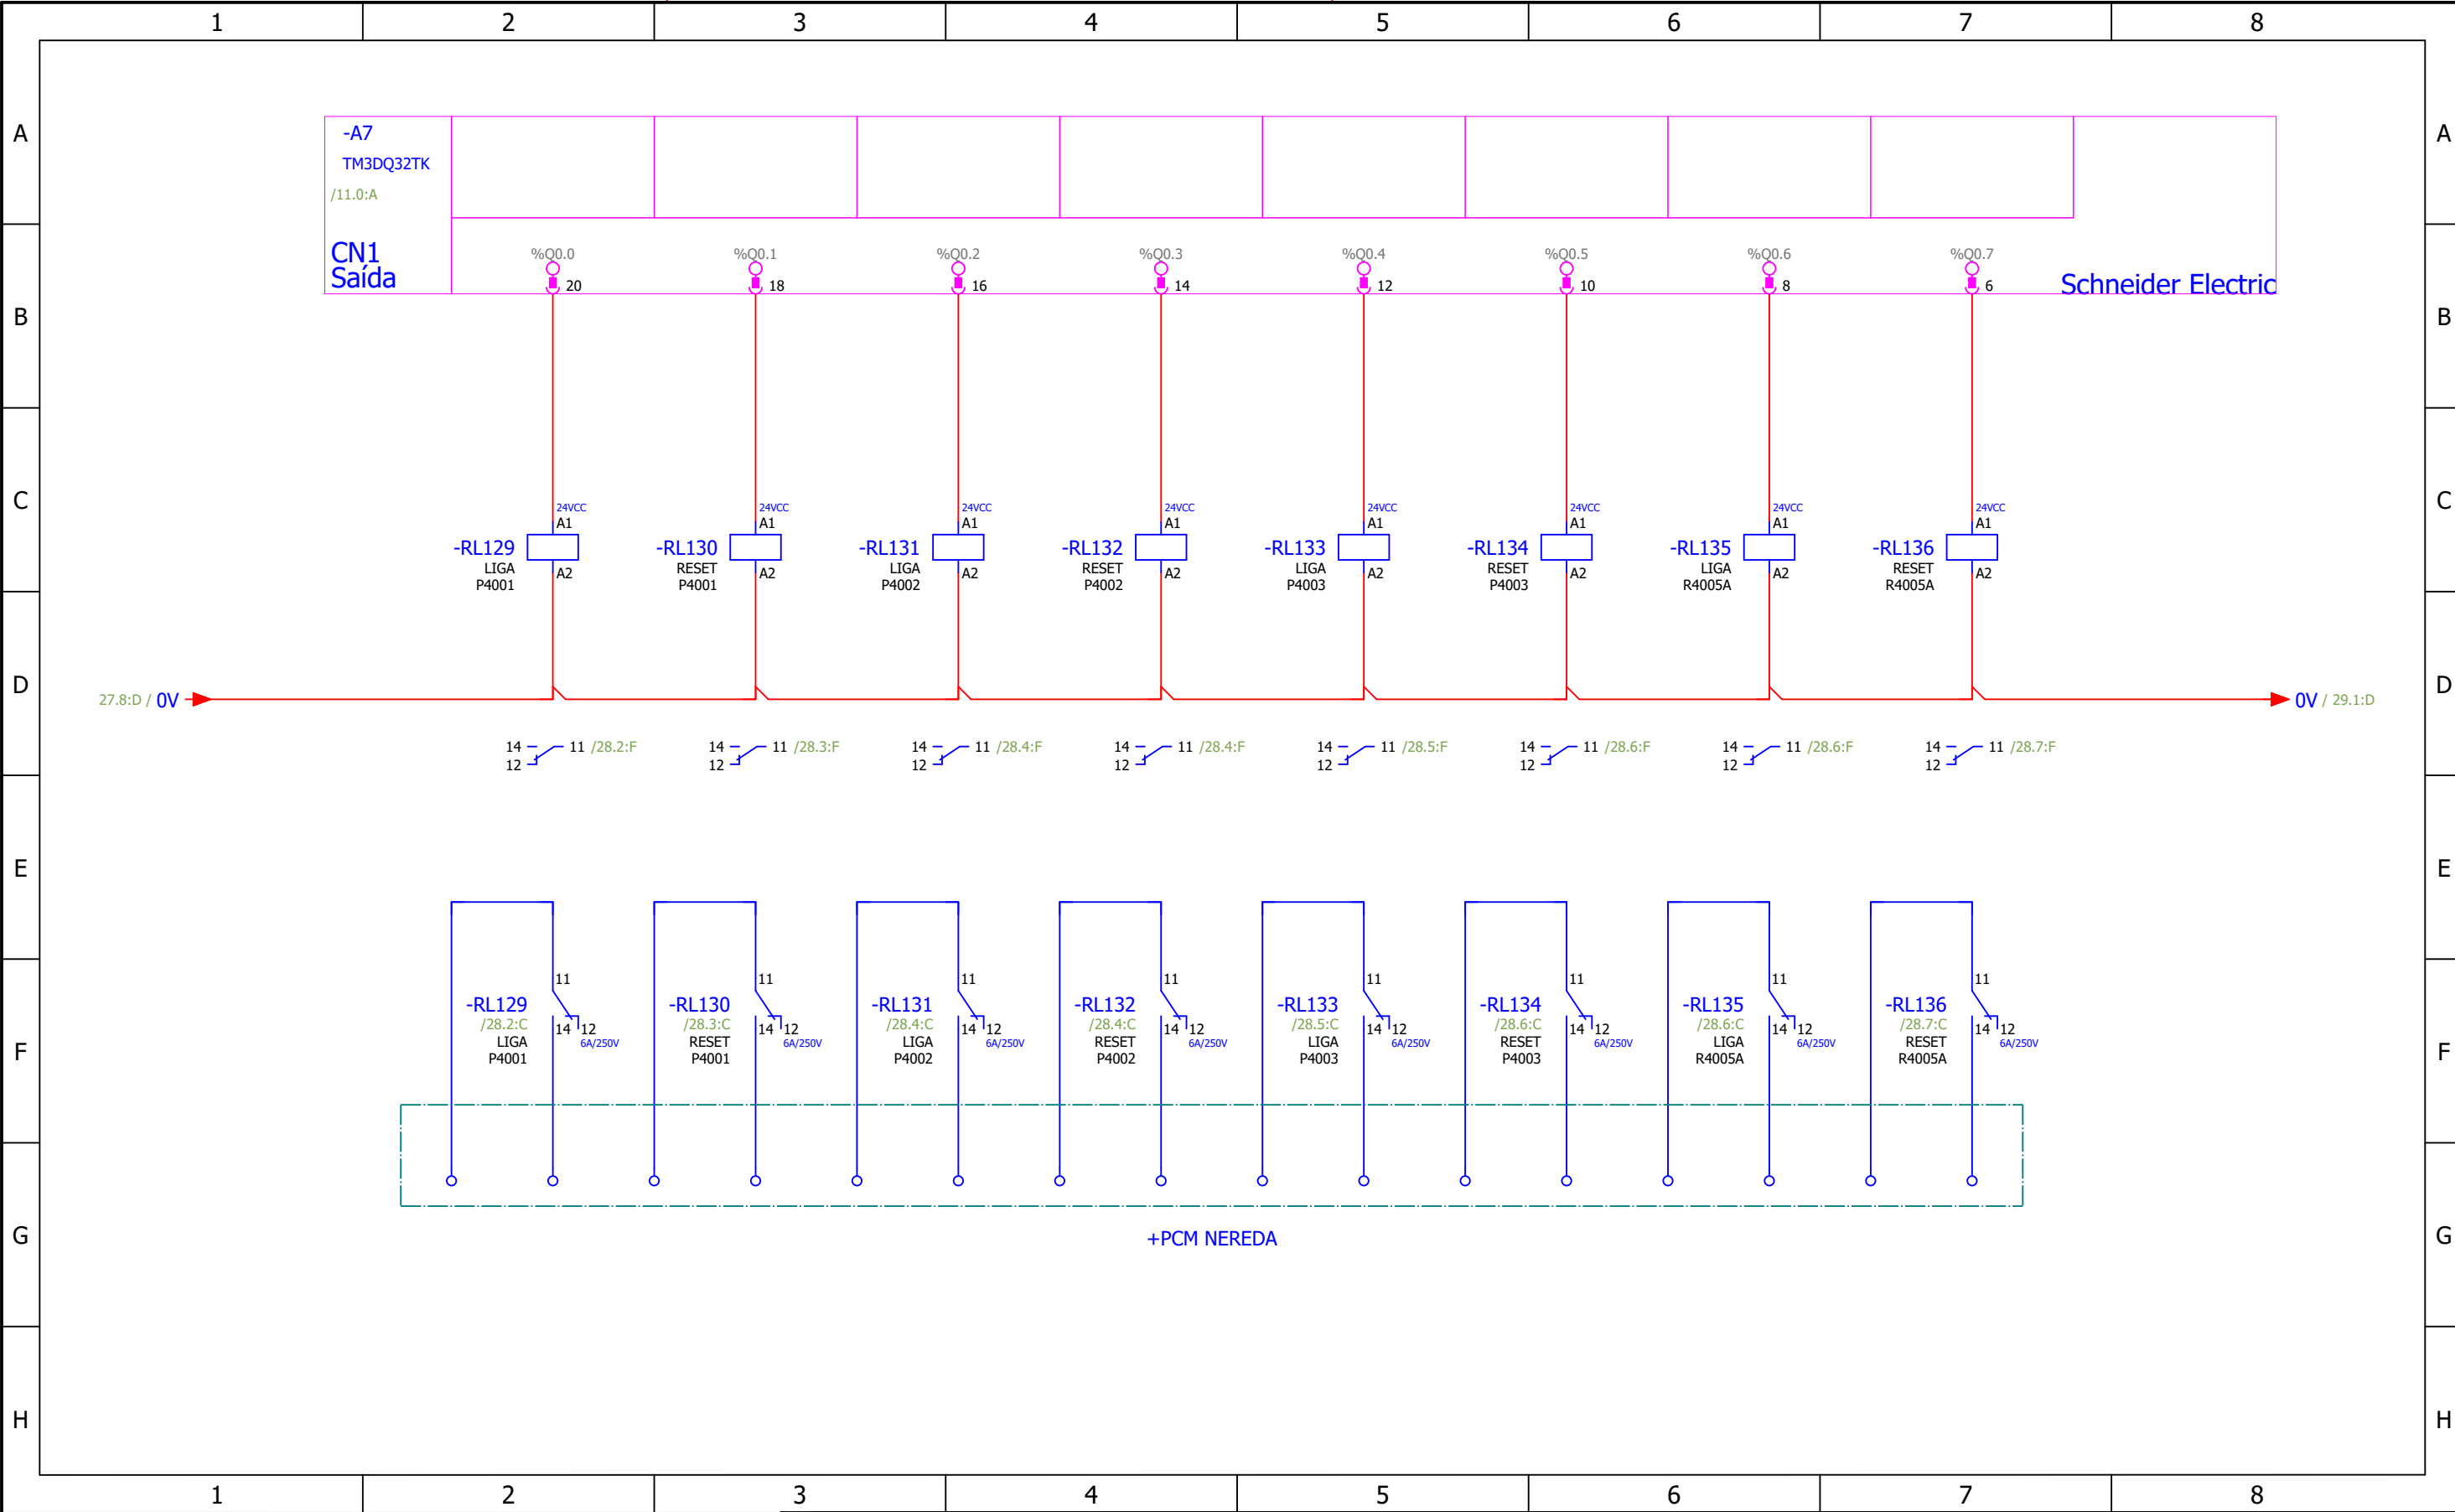



FOLHA: 28 / 58	LEGENDA:					TÍTULO: PCE NEREDA			
						SUB-TÍTULO: Saídas Digitais			
	REVISÃO:	EI					UNID. BRK: SUMARÉ	MUNIC./EST.: SUMARÉ-SP	BAIRRO/ÁREA:
	DATA:	03/06/2025					RESP. TÊC.: JEAN CARLOS ESSER 076760-0/SC	APROVAÇÃO BRK AMBIENTAL:	APROVAÇÃO CLIENTE: BRK
	EXECUÇÃO:	Luiz Corrêa					CÓDIGO DO PROJETO: HID-PA-DE-ETE-ELQ-005		ESCALA: 1:1
VERIFICAÇÃO:	Luiz Corrêa								
APROVAÇÃO:	Rafael Decker				CONTRATANTE: BRK AMBIENTAL	CONTRATO Nº: 230317			

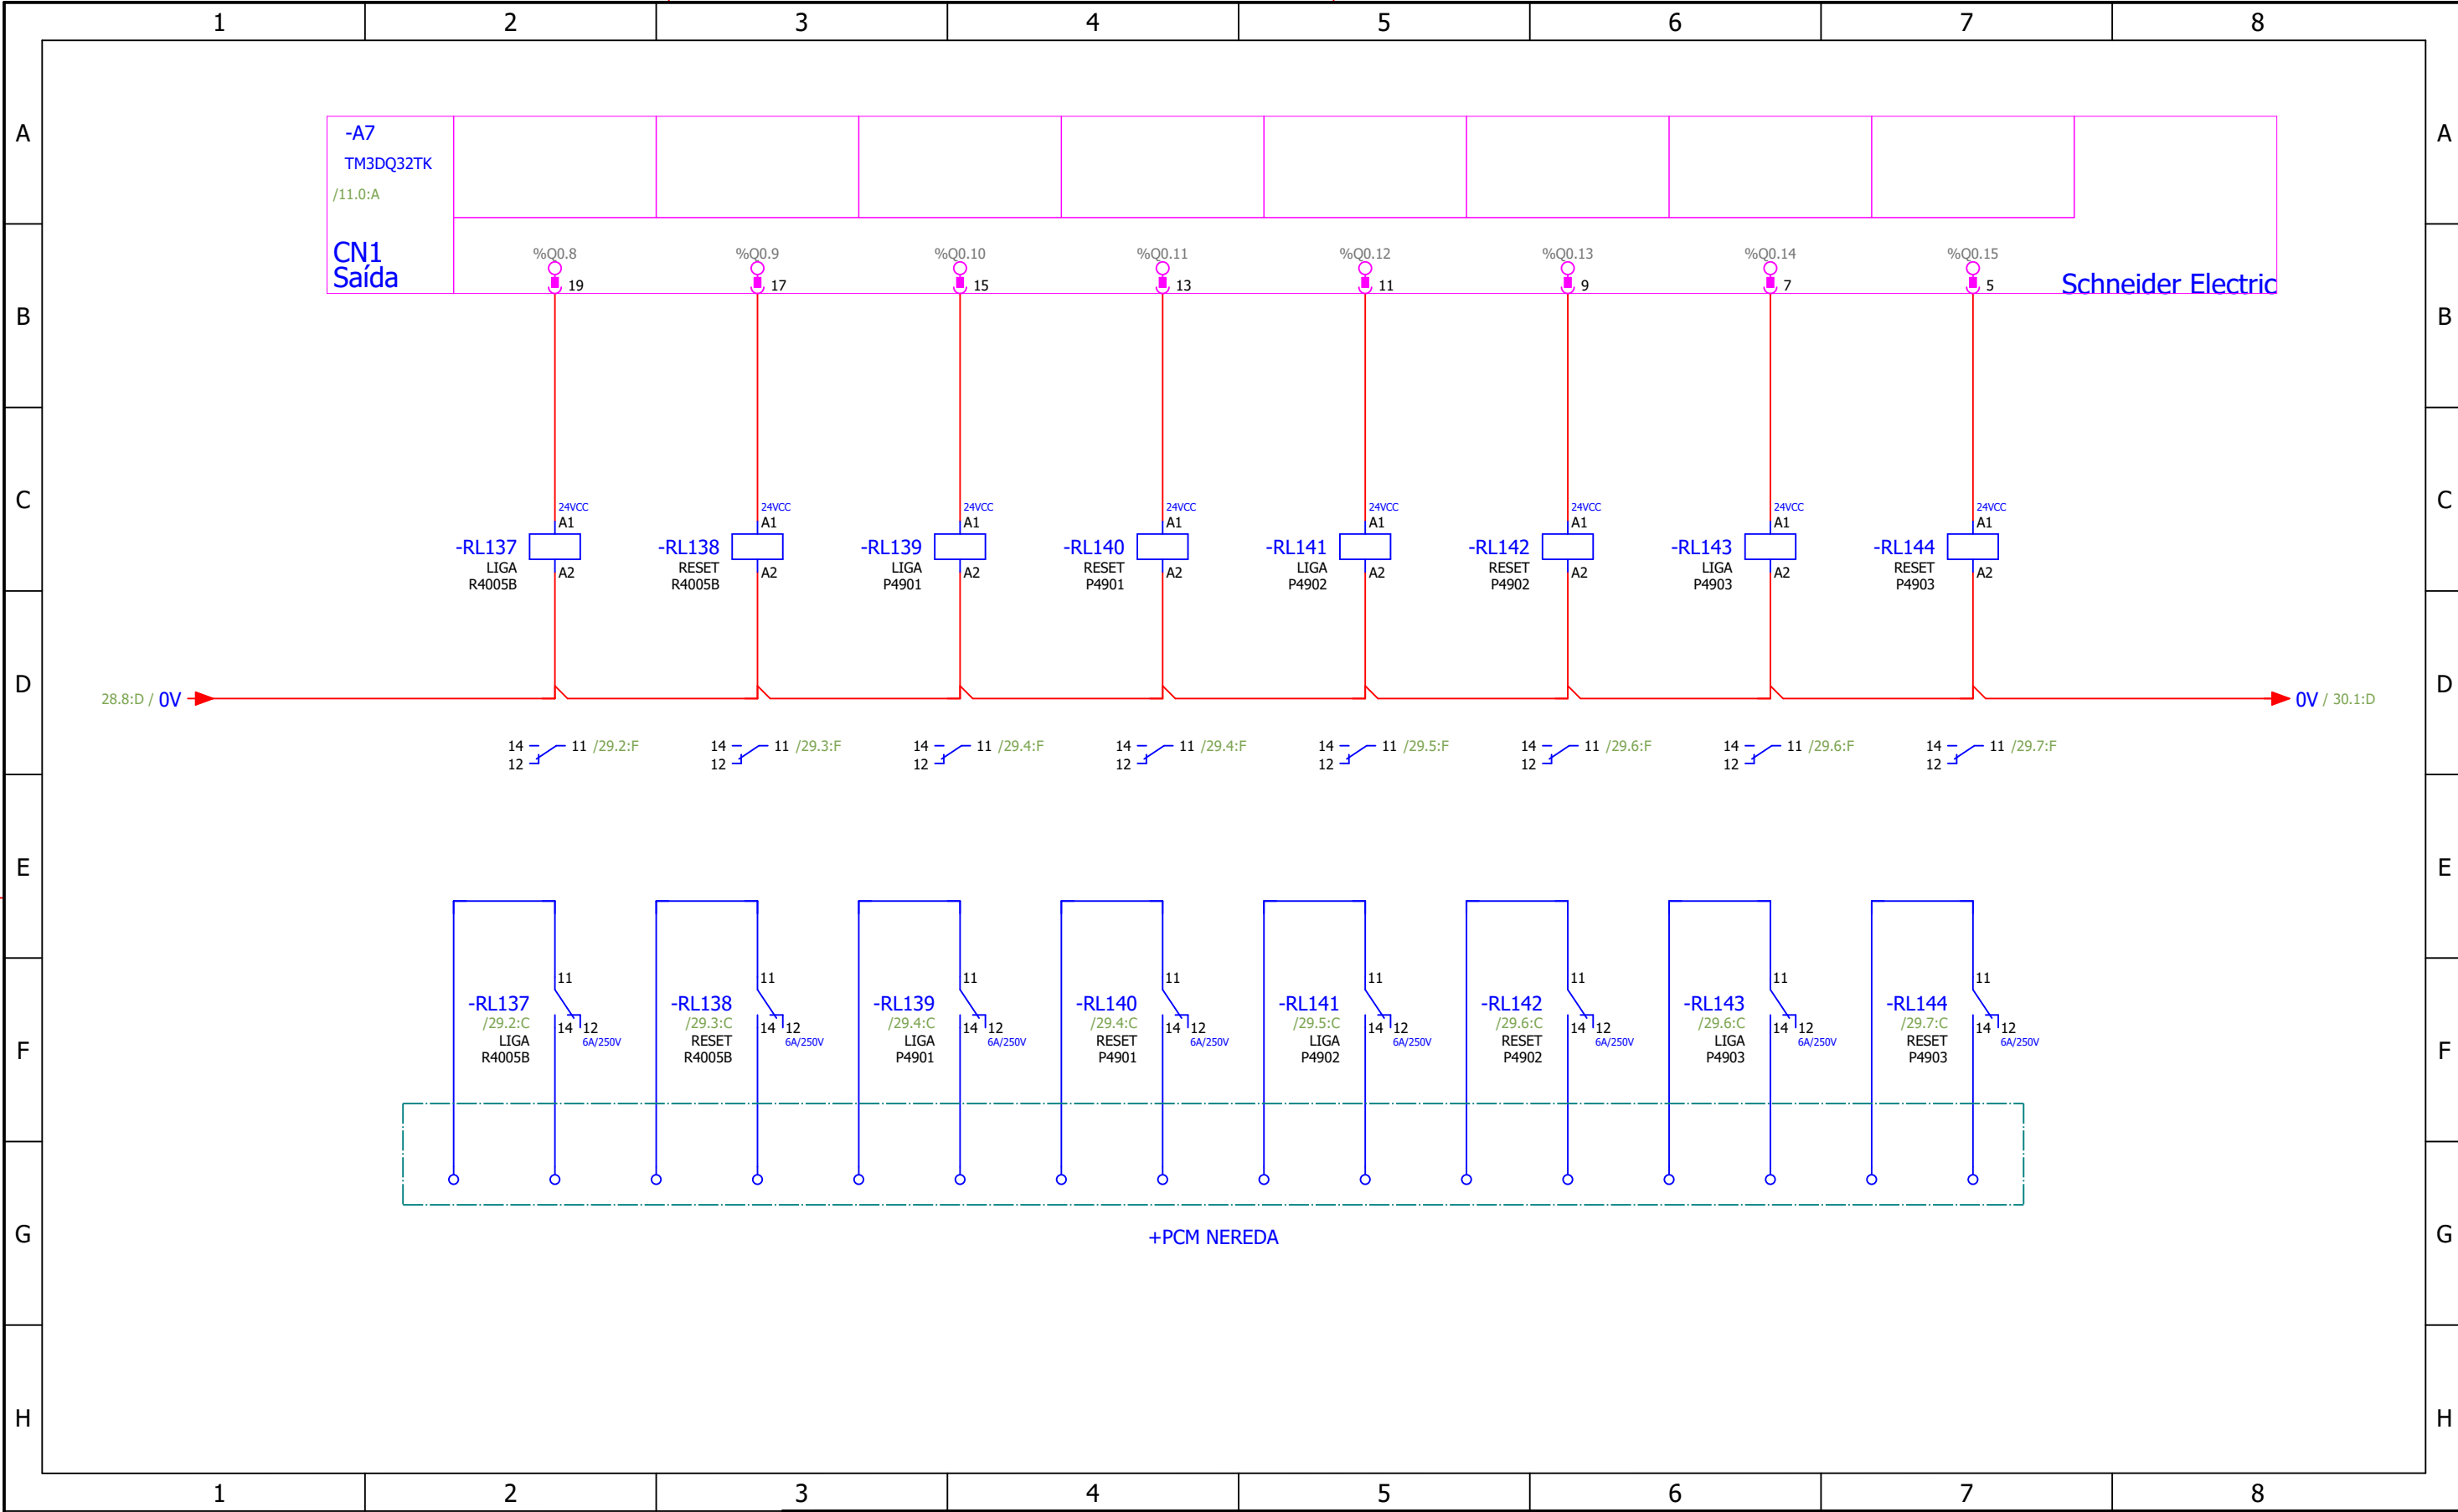

 
FOLHA: 29 / 58		LEGENDA:							TÍTULO: PCE NEREDA									
									SUB-TÍTULO: Saídas Digitais									
		REVISÃO:		EI						UNID. BRK: SUMARÉ		MUNIC./EST.: SUMARÉ-SP		BAIRRO/ÁREA:				
		DATA:		03/06/2025						RESP. TÊC.: JEAN CARLOS ESSER 076760-0/SC		APROVAÇÃO BRK AMBIENTAL:		APROVAÇÃO CLIENTE: BRK				
		EXECUÇÃO:		Luiz Corrêa														
VERIFICAÇÃO:		Luiz Corrêa																
		APROVAÇÃO:		Rafael Decker				CONTRATANTE: BRK AMBIENTAL		CONTRATO Nº: 230317		CÓDIGO DO PROJETO: HID-PA-DE-ETE-ELQ-005			ESCALA: 1:1		REVISÃO: EI	

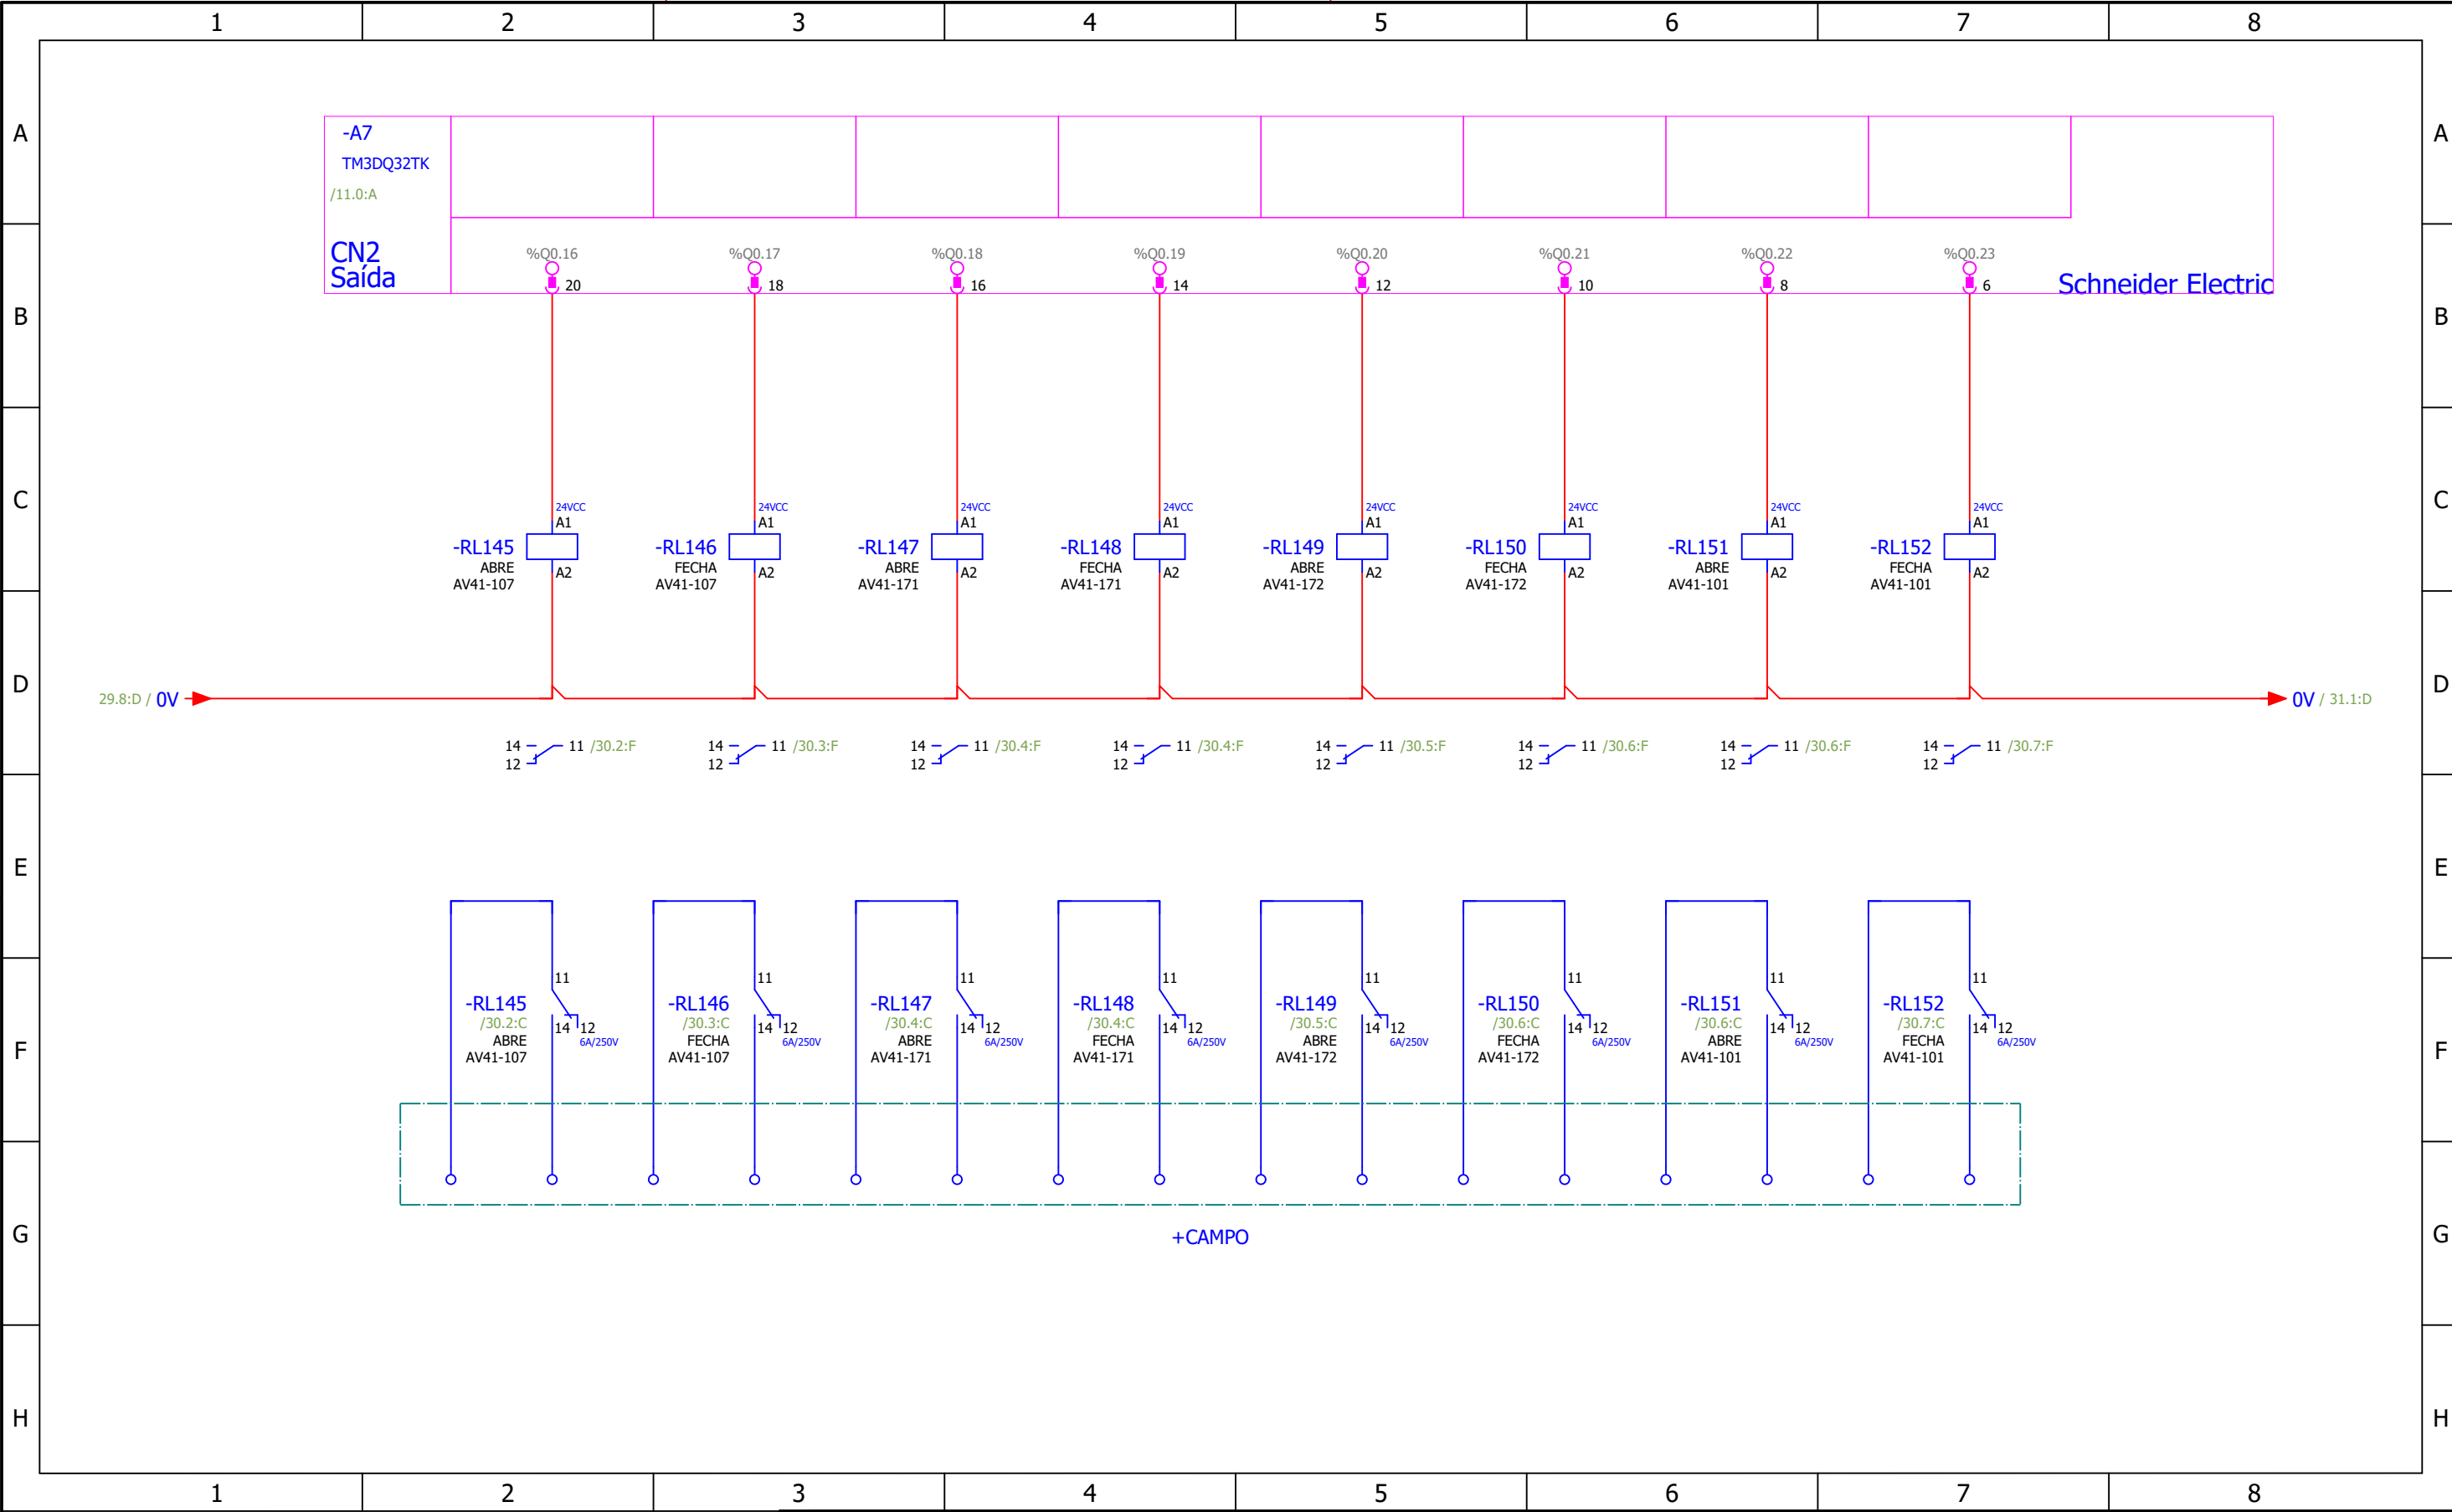


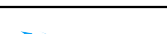
FOLHA: 30 / 58		LEGENDA:							TÍTULO: PCE NEREDA							
									SUB-TÍTULO: Saídas Digitais							
		REVISÃO:		EI							UNID. BRK: SUMARÉ		MUNIC./EST.: SUMARÉ-SP		BAIRRO/ÁREA:	
		DATA:		03/06/2025							RESP. TÊC.: JEAN CARLOS ESSER 076760-0/SC		APROVAÇÃO BRK AMBIENTAL:		APROVAÇÃO CLIENTE: BRK	
		EXECUÇÃO:		Luiz Corrêa							CREA:					
VERIFICAÇÃO:		Luiz Corrêa					CONTRATANTE: BRK AMBIENTAL				CONTRATO Nº: 230317		CÓDIGO DO PROJETO: HID-PA-DE-ETE-ELQ-005		ESCALA: 1:1	
		APROVAÇÃO:		Rafael Decker												

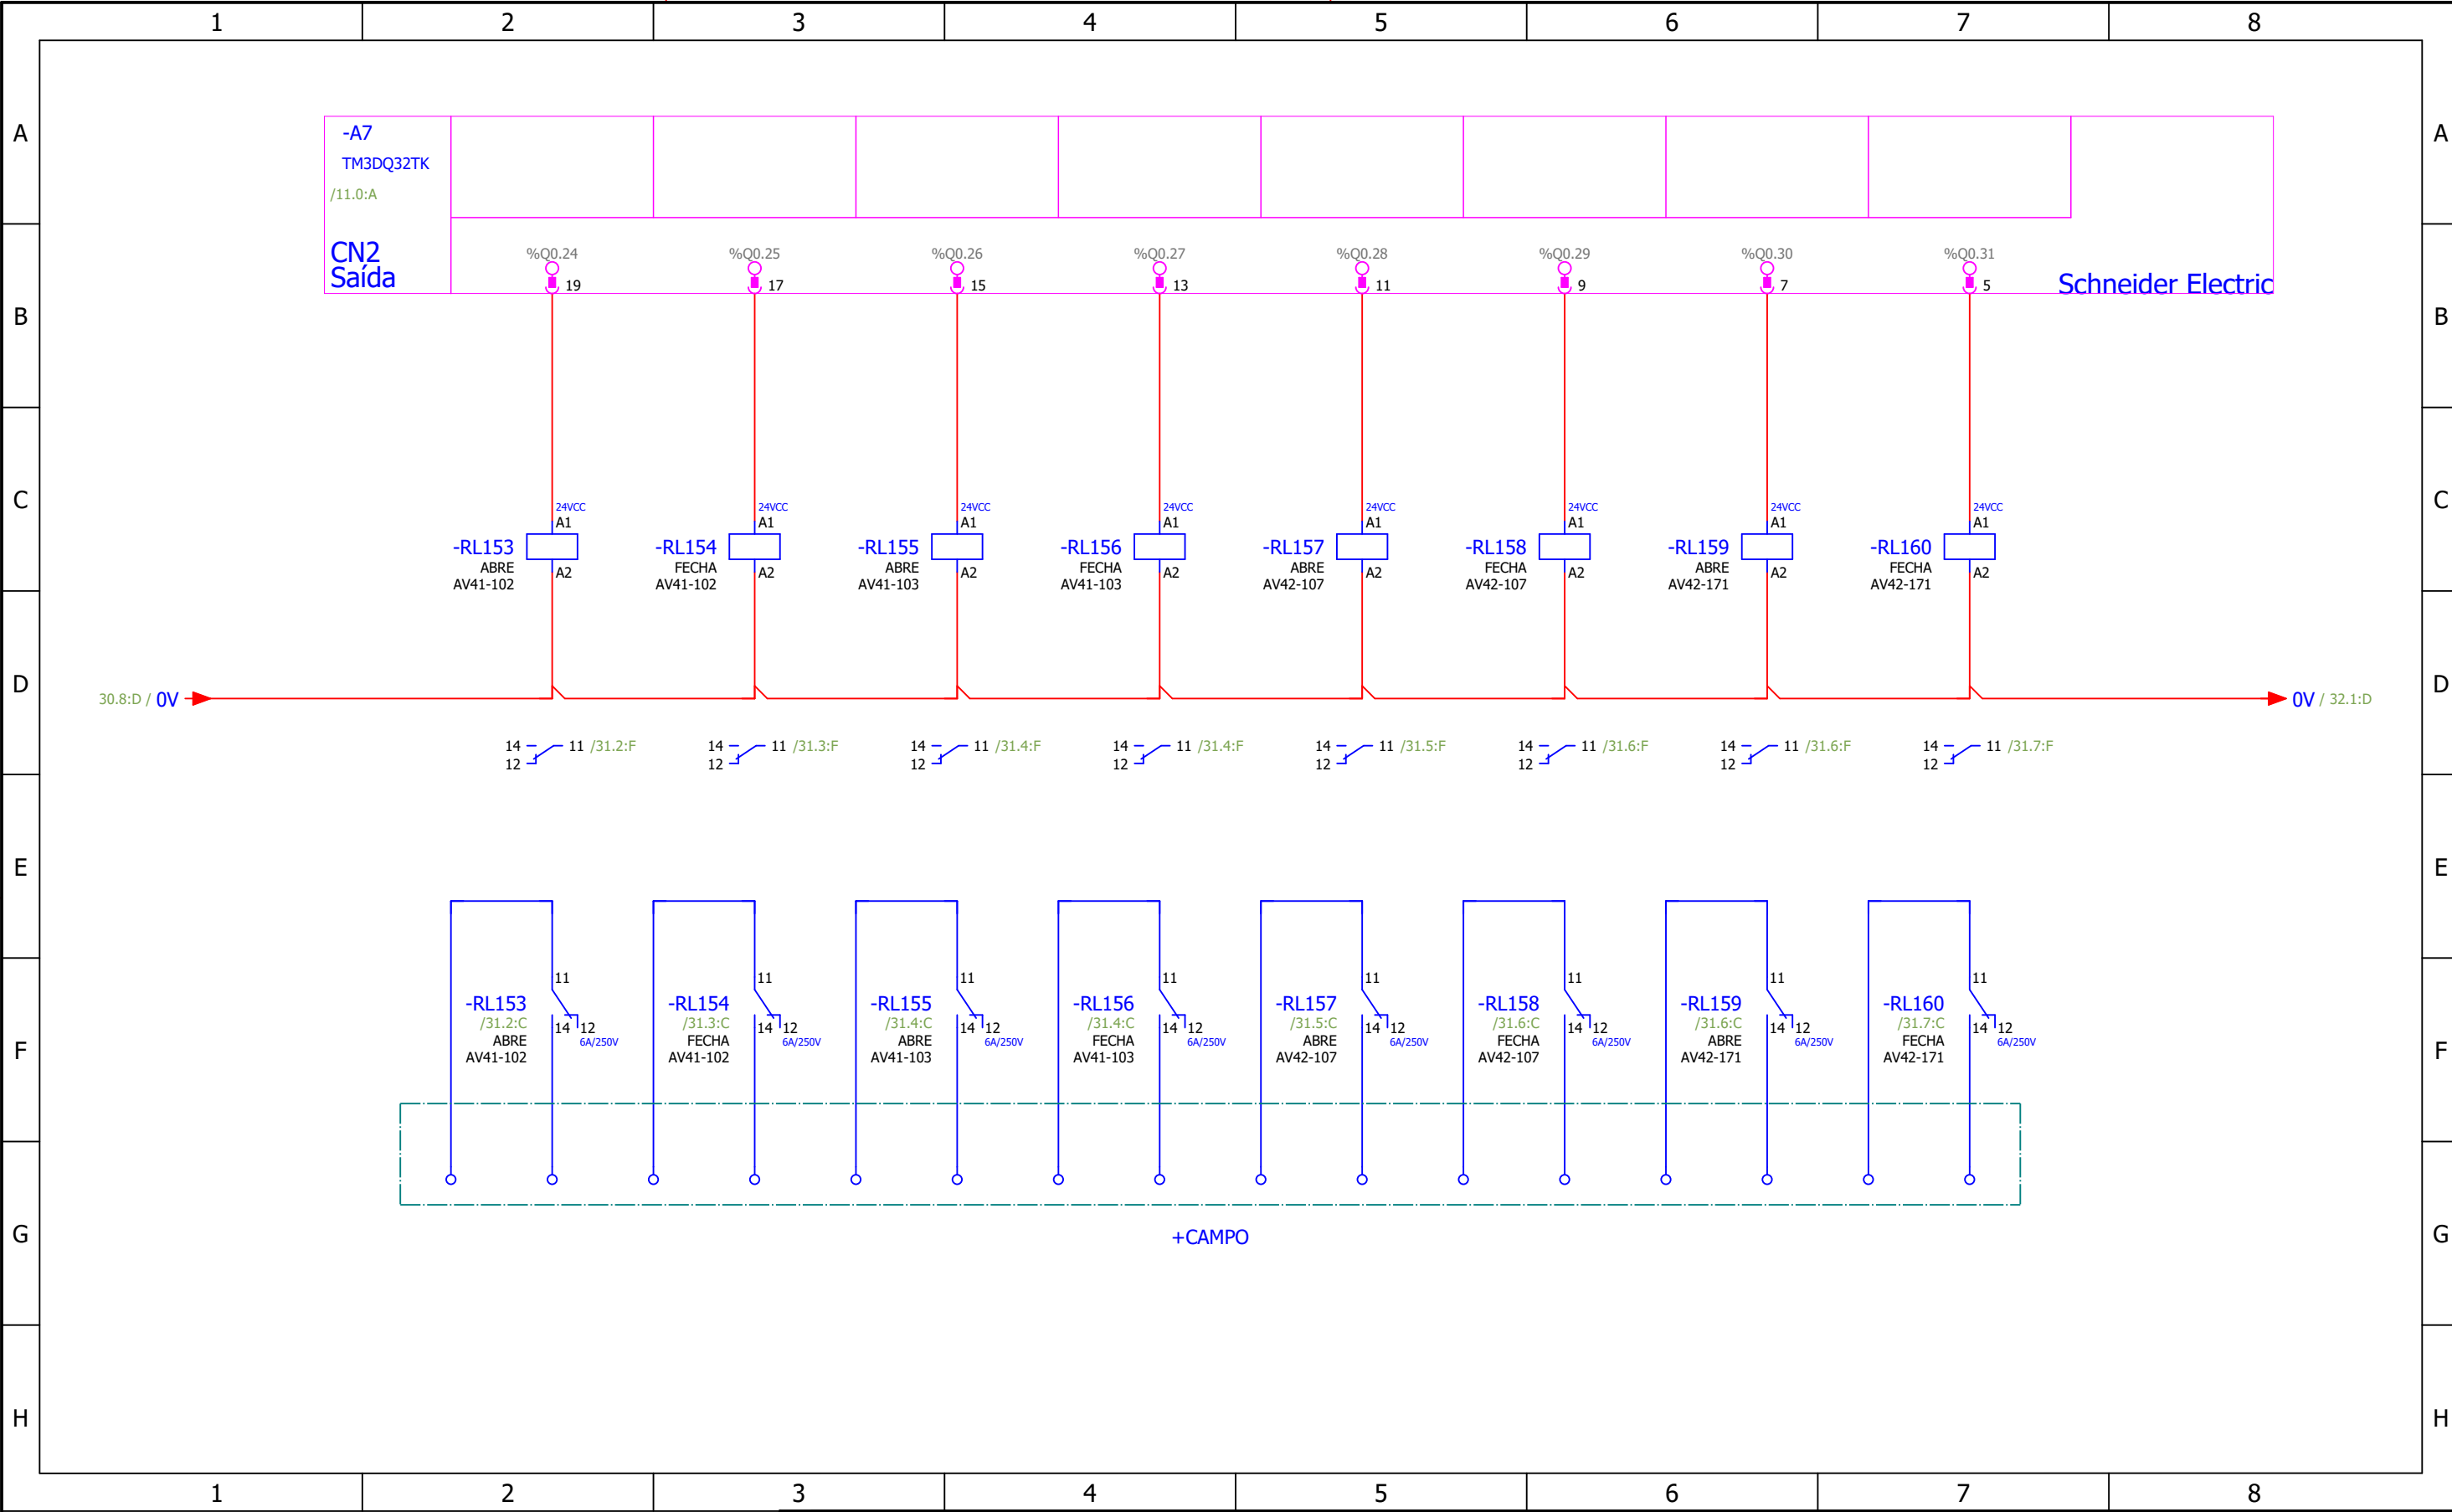


FOLHA: 31 / 58			LEGENDA:							TÍTULO: PCE NEREDA									
										SUB-TÍTULO: Saídas Digitais									
			REVISÃO:		EI								UNID. BRK: SUMARÉ		MUNIC./EST.: SUMARÉ-SP		BAIRRO/ÁREA:		
			DATA:		03/06/2025								RESP. TÊC.: JEAN CARLOS ESSER 076760-0/SC		APROVAÇÃO BRK AMBIENTAL:		APROVAÇÃO CLIENTE: BRK		
			EXECUÇÃO:		Luiz Corrêa								CONTRATANTE: BRK AMBIENTAL		CONTRATO Nº: 230317		CÓDIGO DO PROJETO: HID-PA-DE-ETE-ELQ-005		ESCALA: 1:1
VERIFICAÇÃO:		Luiz Corrêa																	
APROVAÇÃO:		Rafael Decker																	

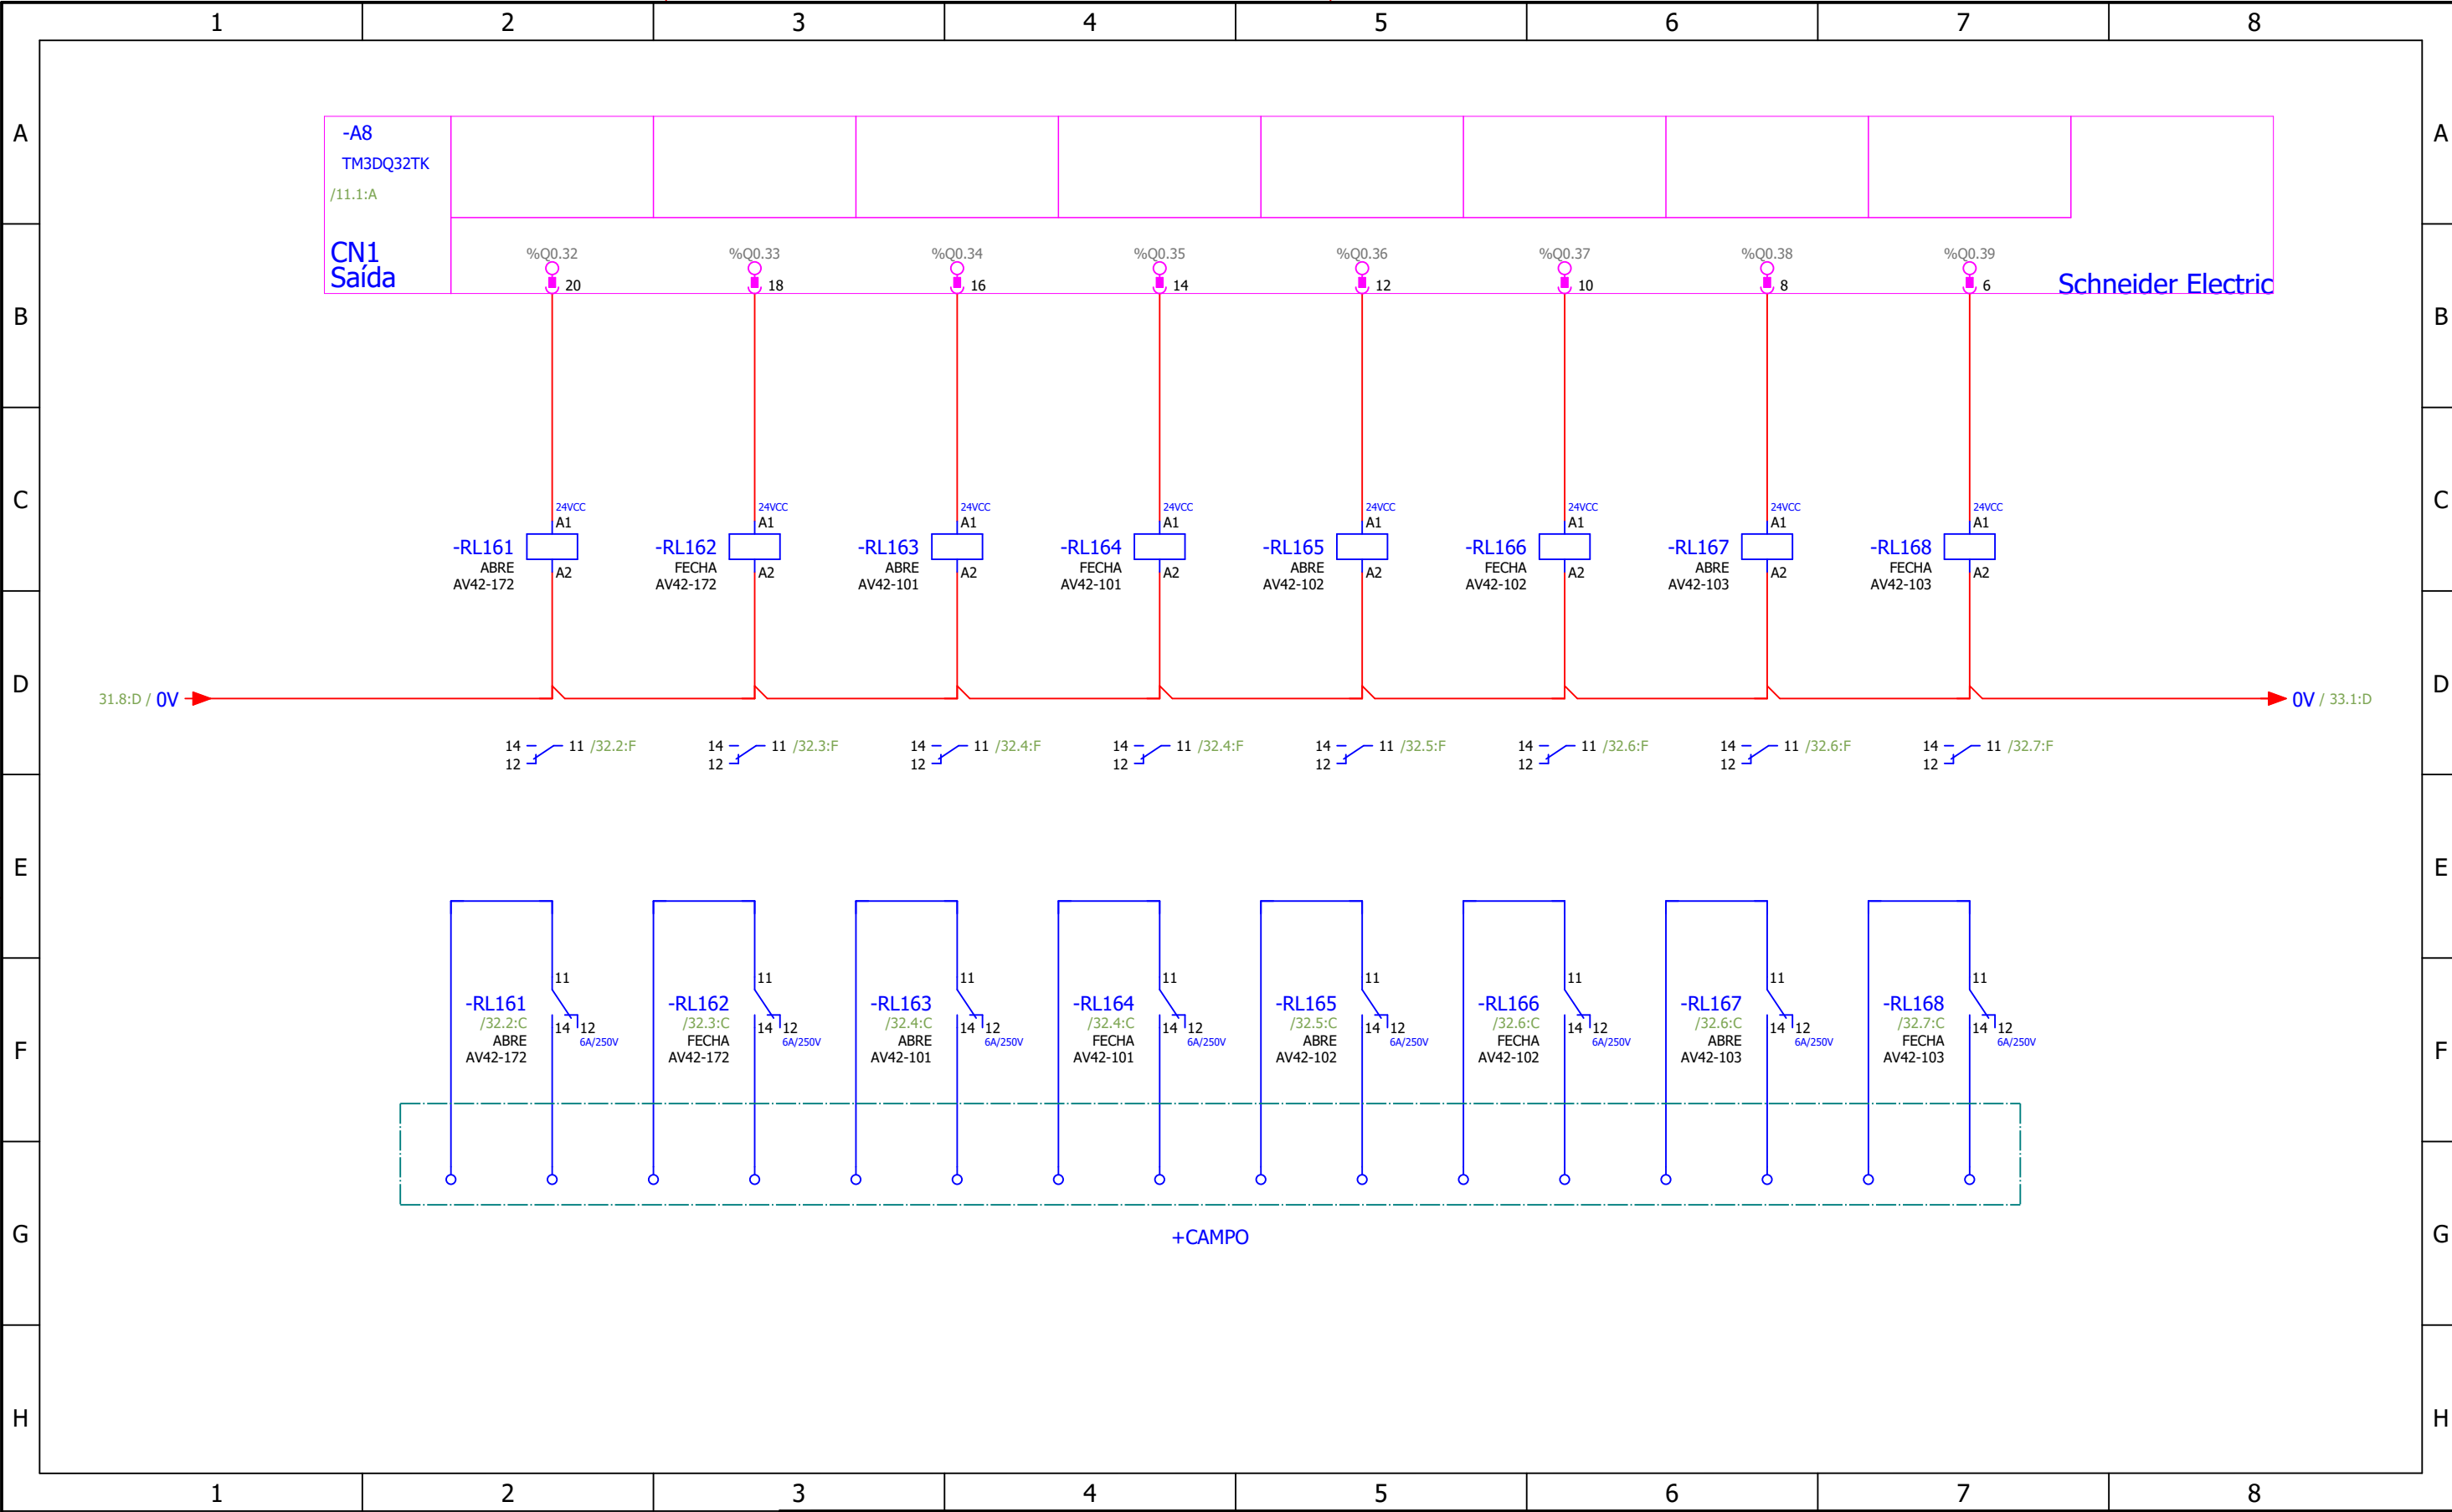


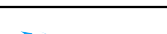
FOLHA: 32 / 58		LEGENDA:							TÍTULO: PCE NEREDA						
									SUB-TÍTULO: Saídas Digitais						
		REVISÃO:		EI						UNID. BRK: SUMARÉ	MUNIC./EST.: SUMARÉ-SP	BAIRRO/ÁREA:			
		DATA:		03/06/2025						RESP. TÊC.: JEAN CARLOS ESSER 076760-0/SC	APROVAÇÃO BRK AMBIENTAL:	APROVAÇÃO CLIENTE: BRK			
		EXECUÇÃO:		Luiz Corrêa											
VERIFICAÇÃO:		Luiz Corrêa													
		APROVAÇÃO:		Rafael Decker				CONTRATANTE: BRK AMBIENTAL		CONTRATO Nº: 230317		CÓDIGO DO PROJETO: HID-PA-DE-ETE-ELQ-005		ESCALA: 1:1	REVISÃO: EI

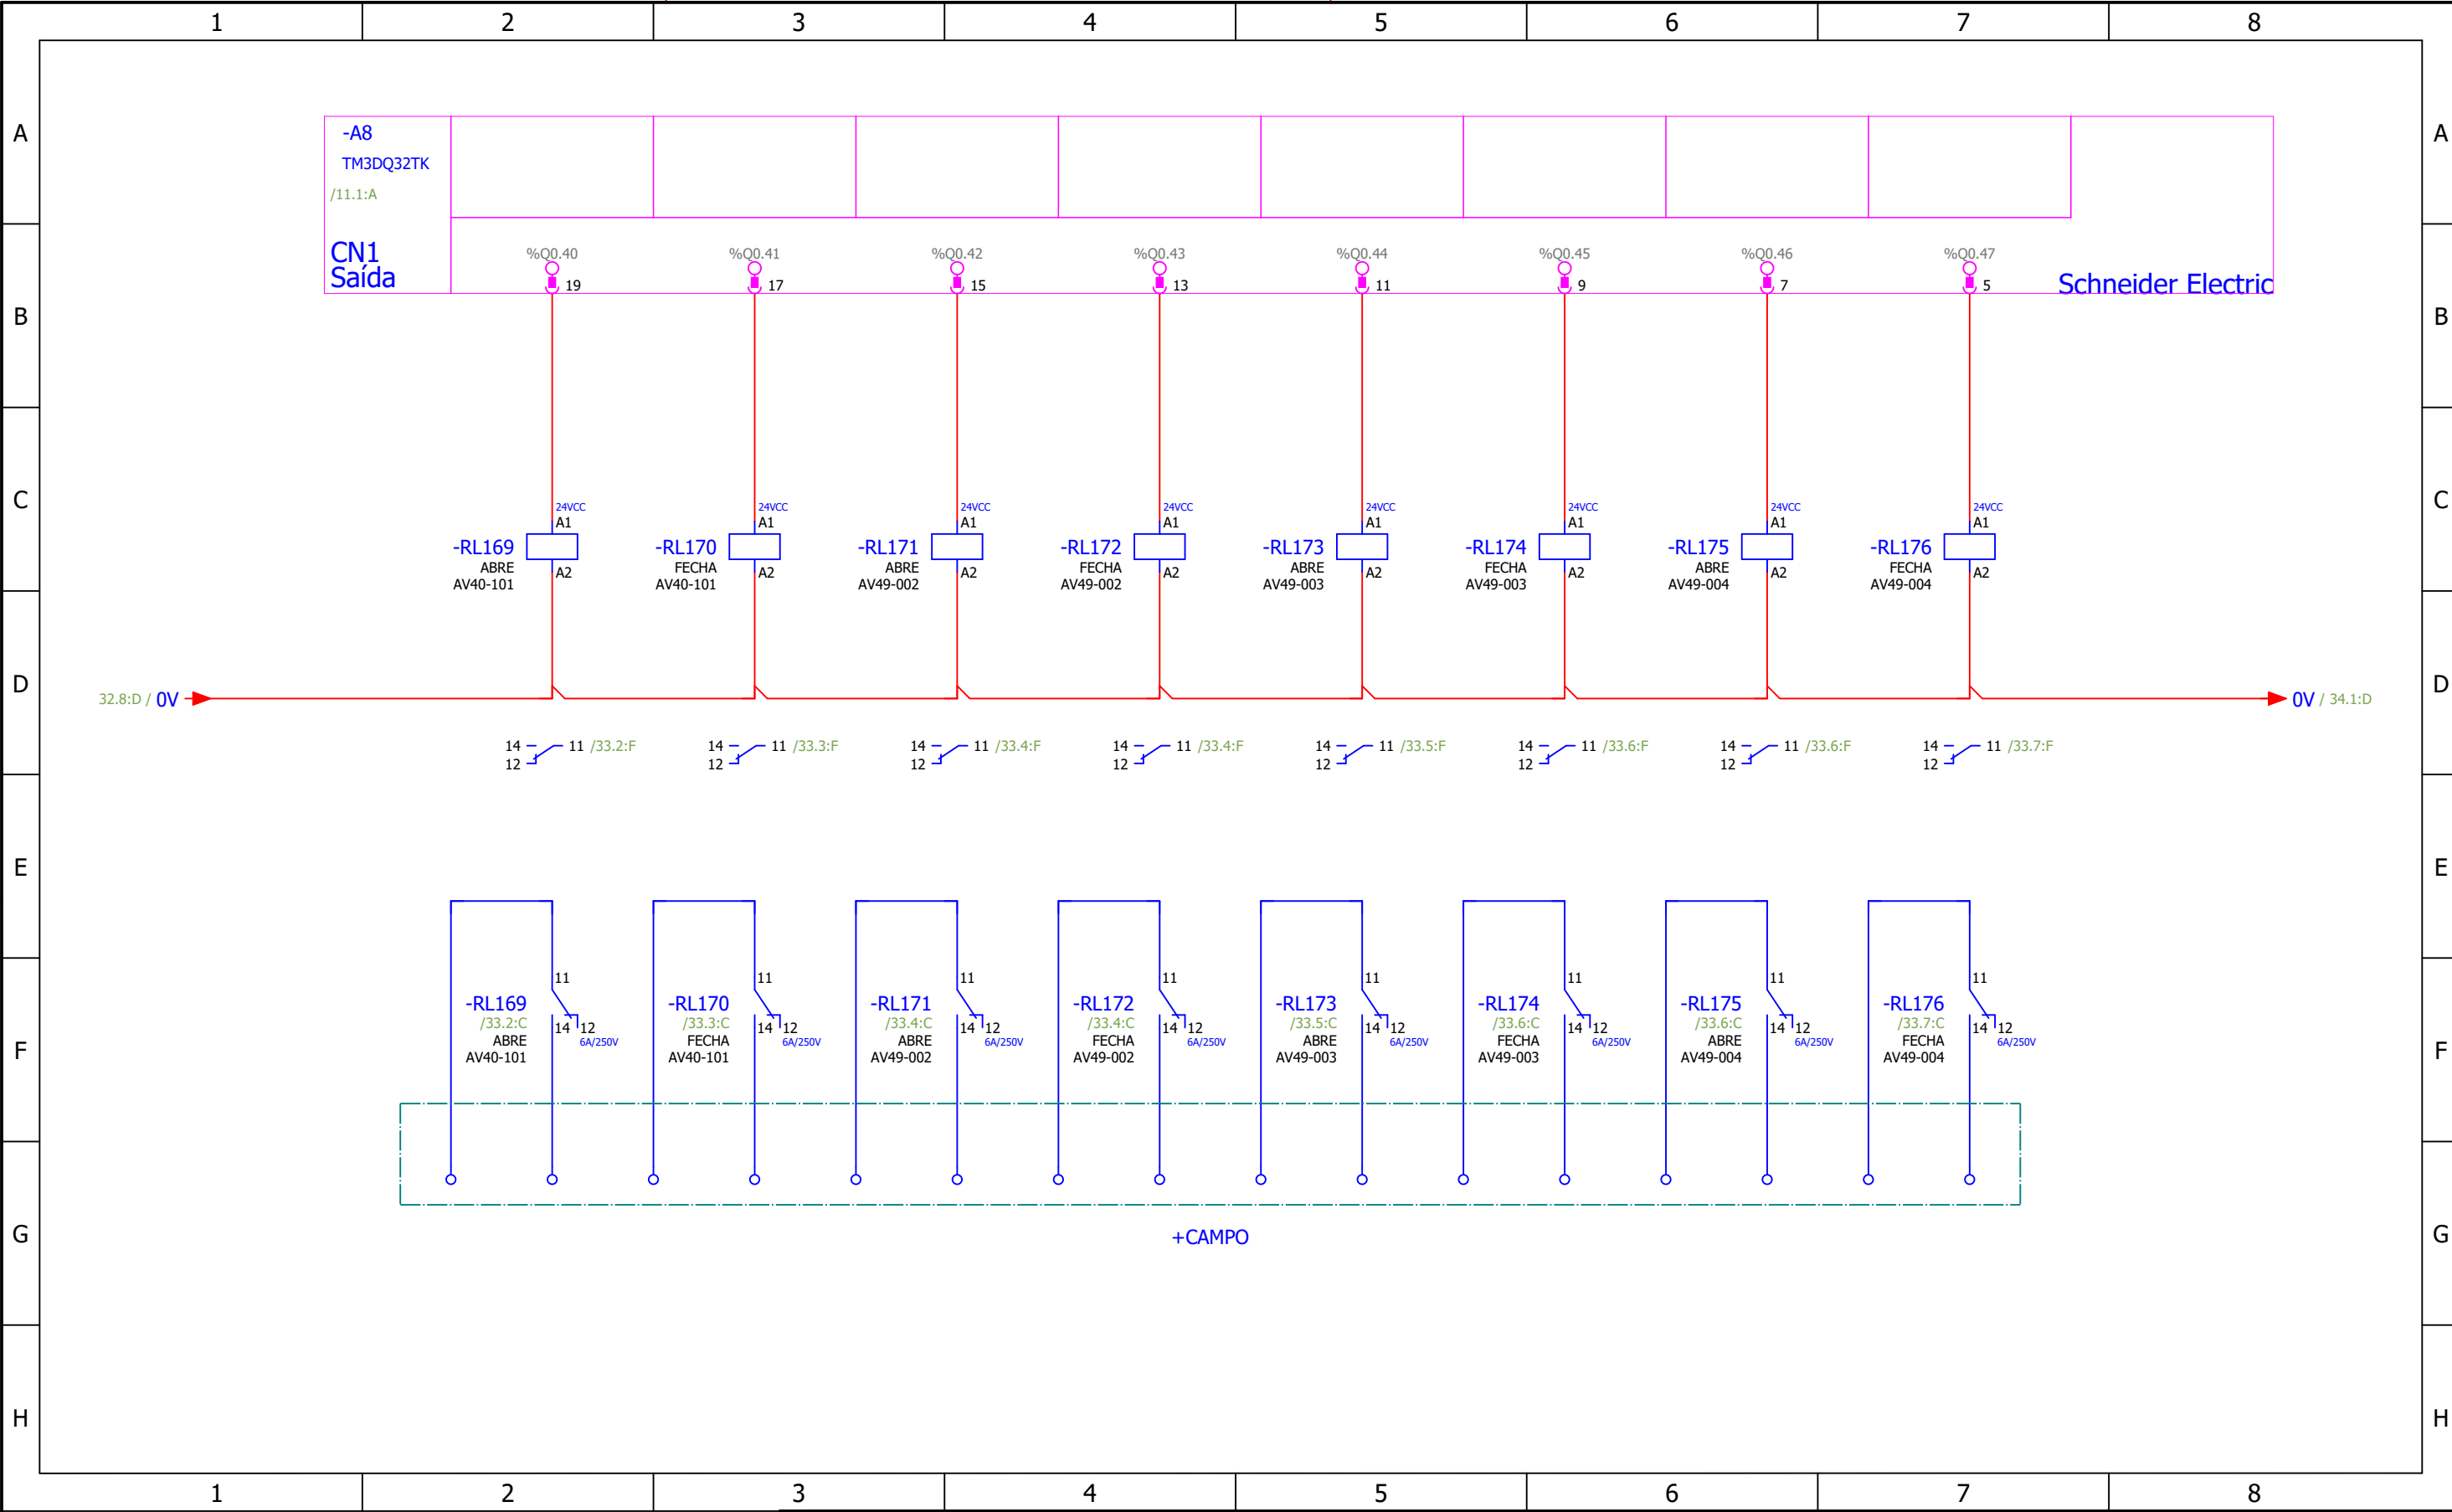


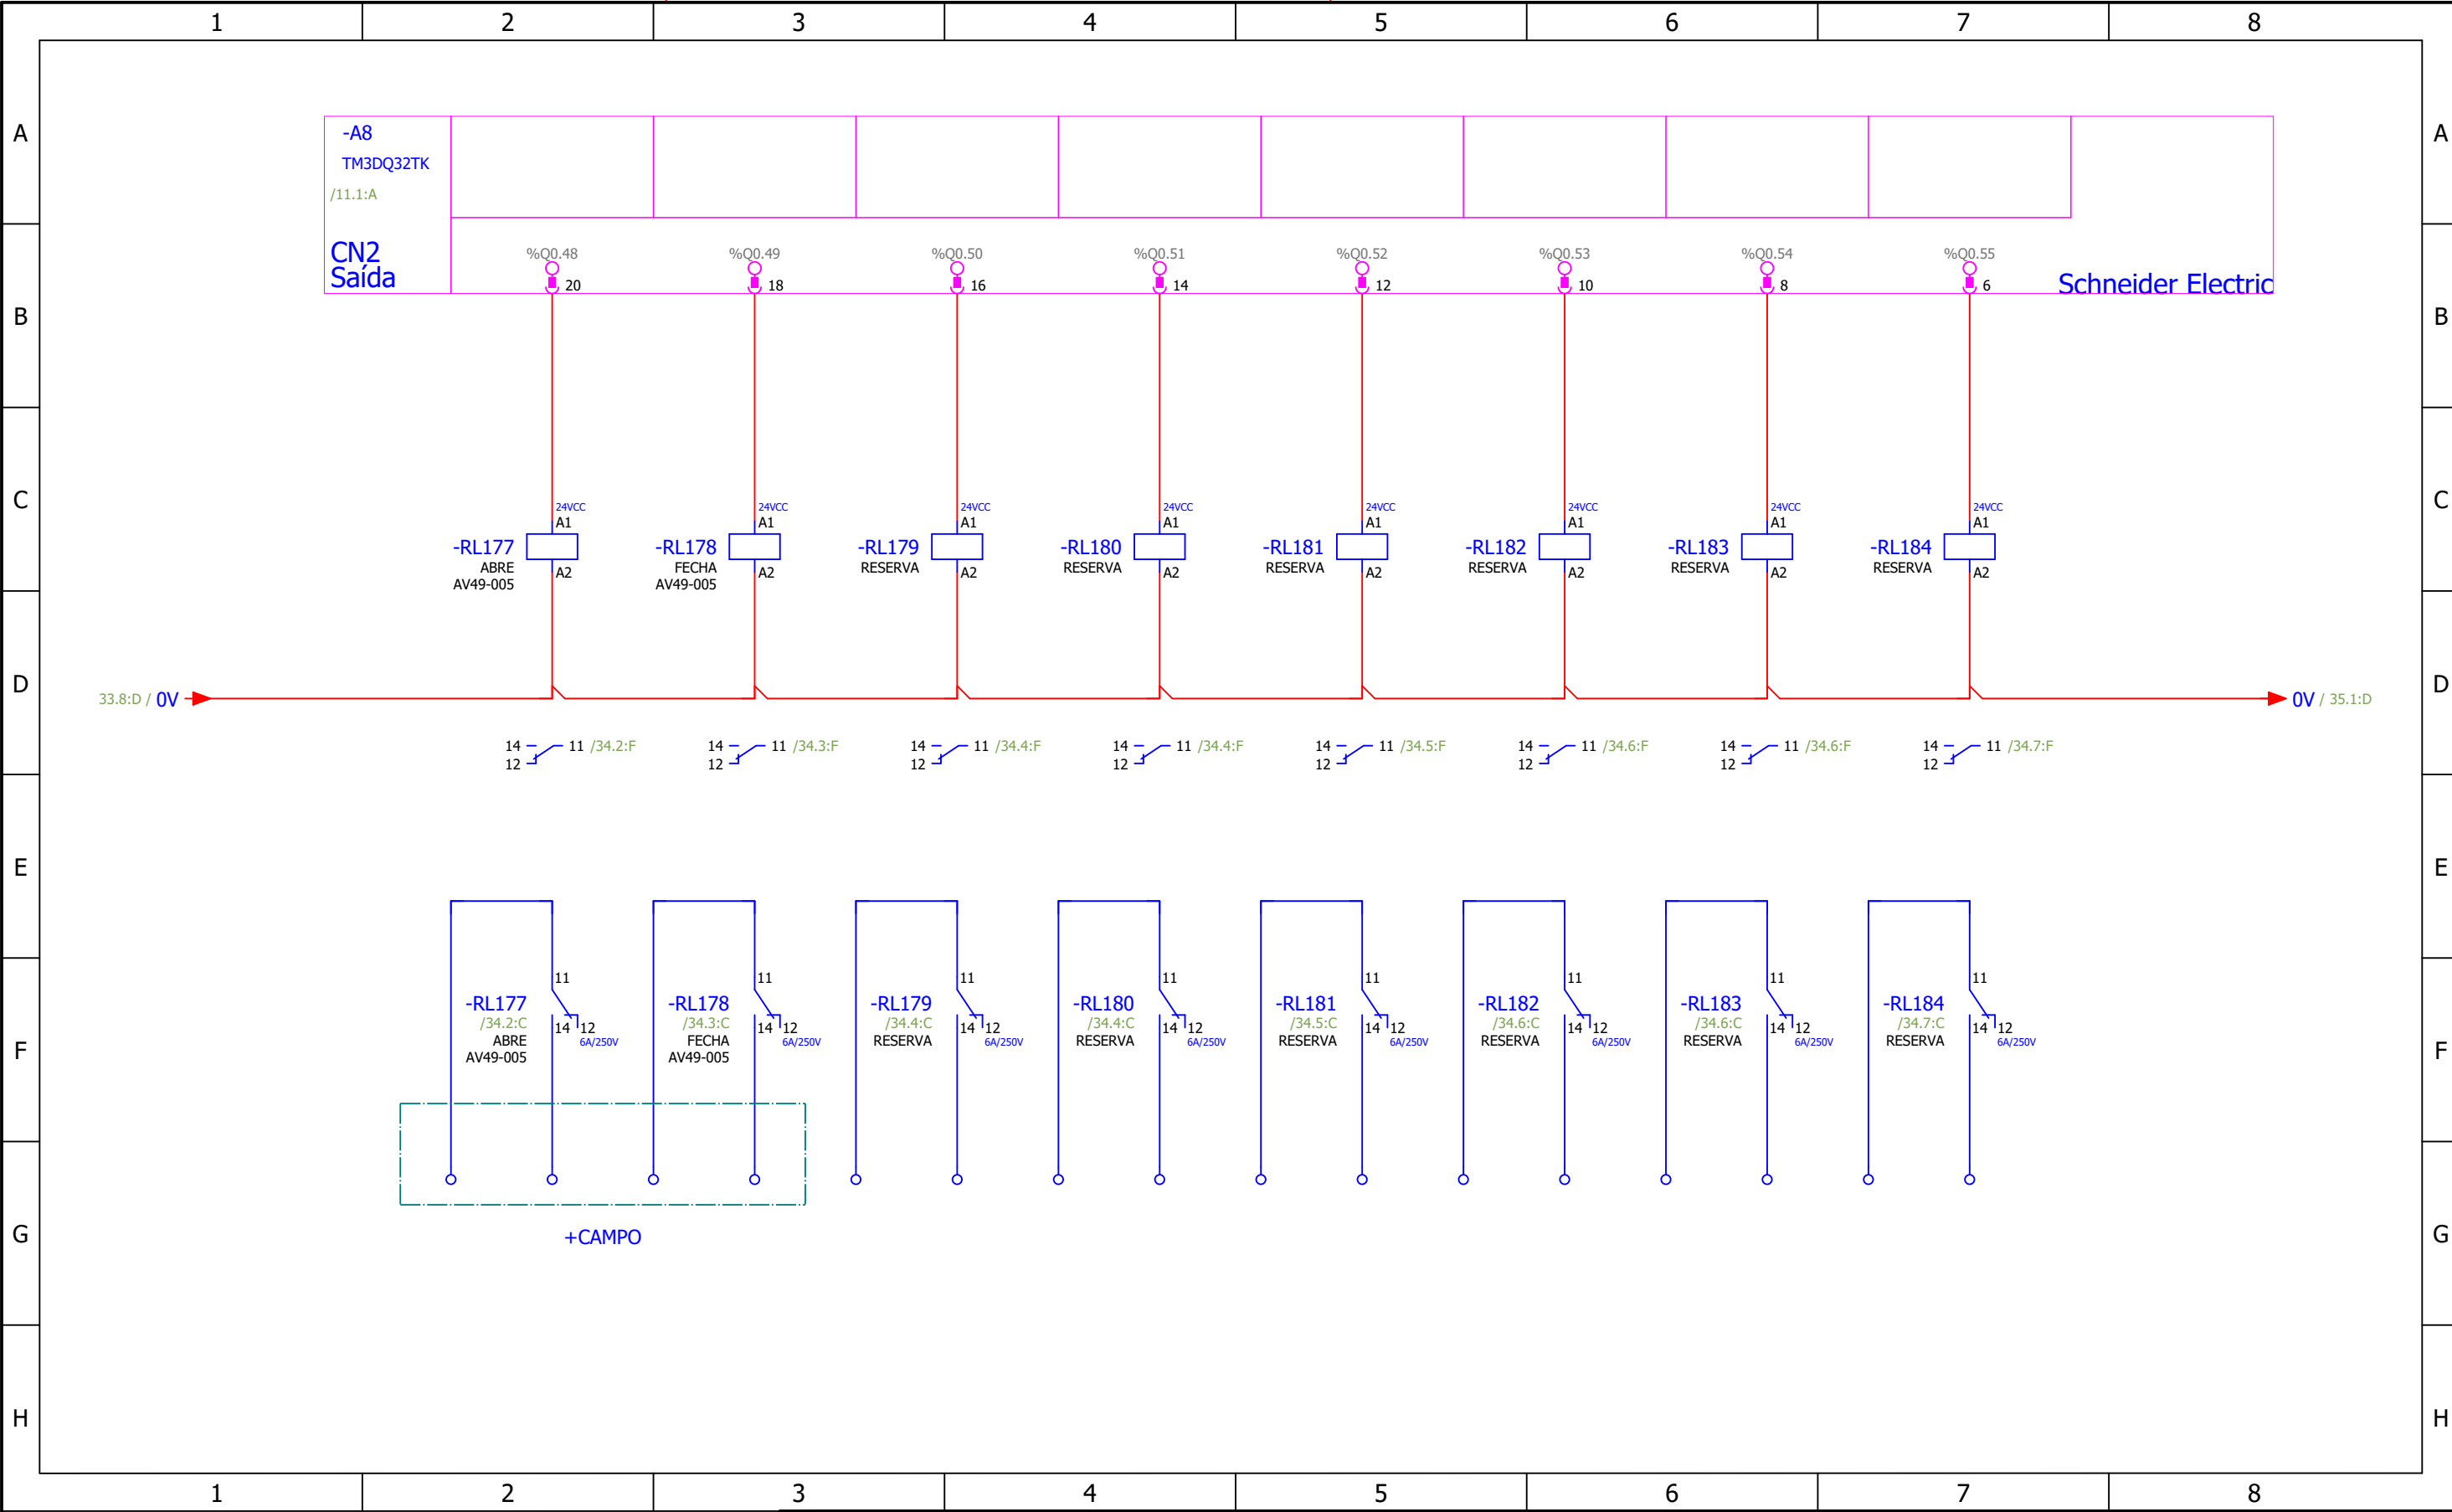


FOLHA: 34 / 58		LEGENDA:							TÍTULO: PCE NEREDA								
									SUB-TÍTULO: Saídas Digitais								
												REVISÃO:		EI			
DATA:		03/06/2025				RESP. TÊC.: JEAN CARLOS ESSER 076760-0/SC		APROVAÇÃO BRK AMBIENTAL:		APROVAÇÃO CLIENTE: BRK							
EXECUÇÃO:		Luiz Corrêa				CONTRATANTE: BRK AMBIENTAL		CONTRATO Nº: 230317		CÓDIGO DO PROJETO: HID-PA-DE-ETE-ELQ-005		ESCALA: 1:1		REVISÃO: EI			
VERIFICAÇÃO:		Luiz Corrêa															
APROVAÇÃO:		Rafael Decker															

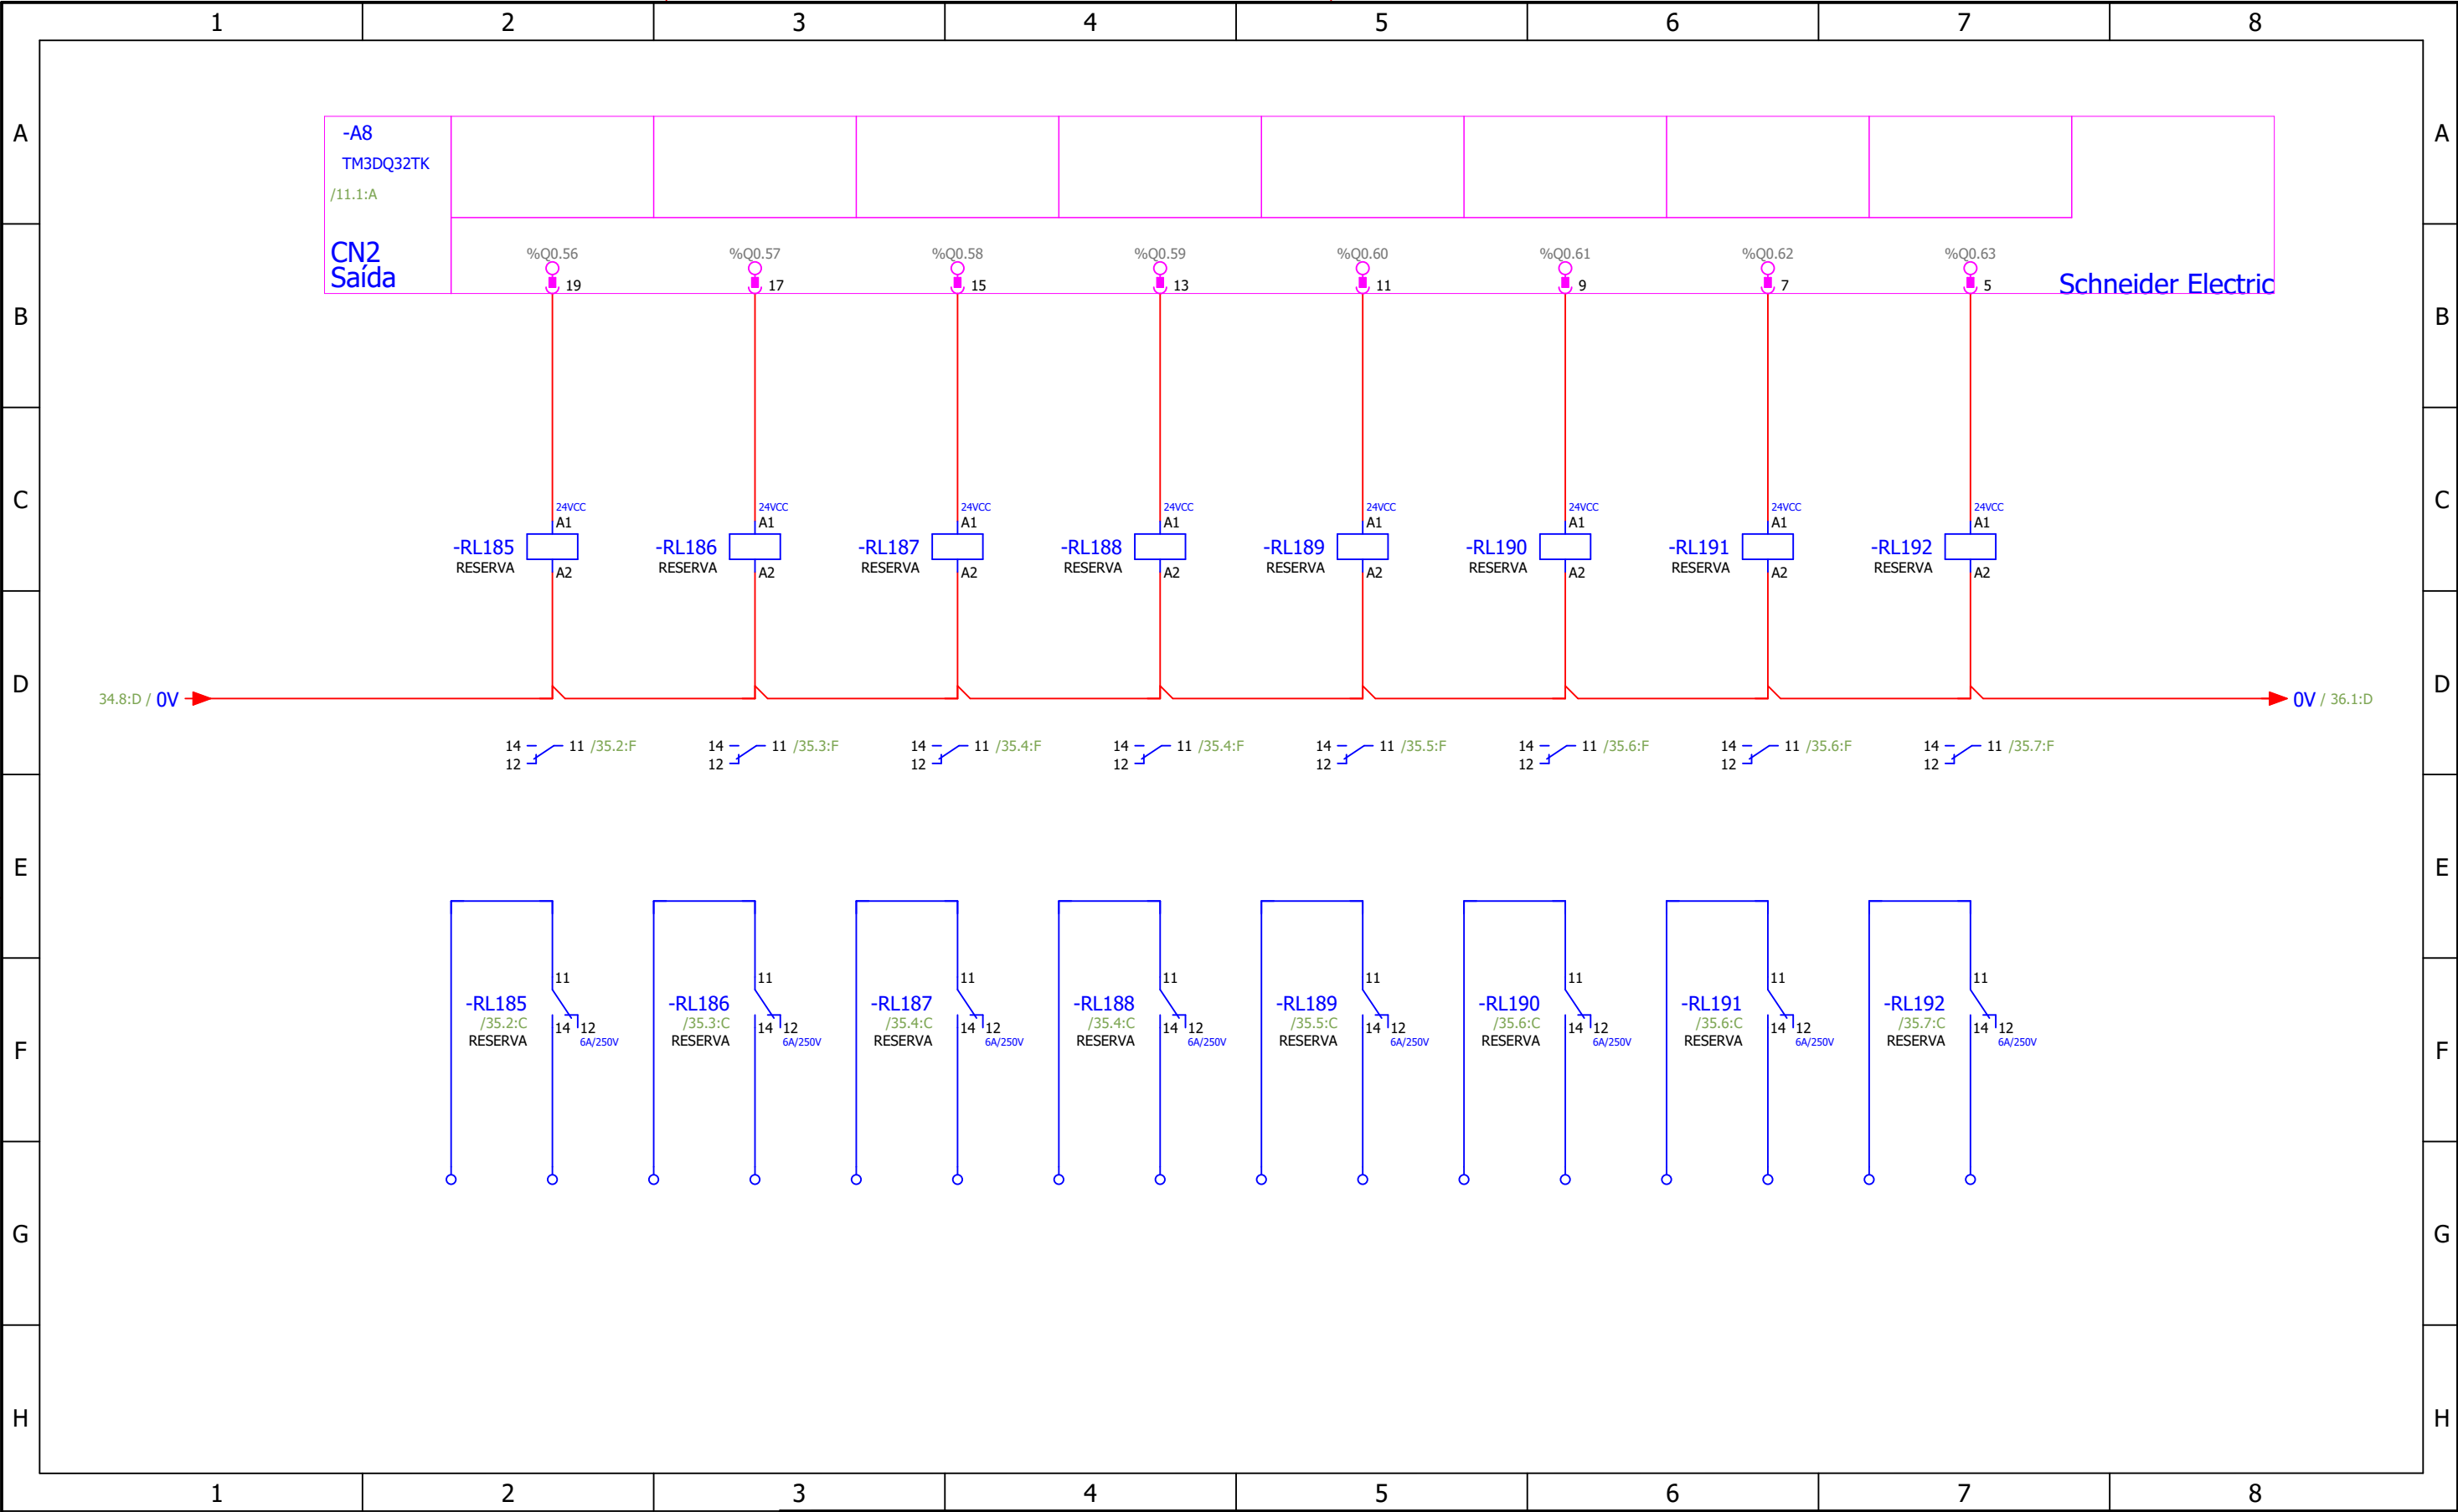


 
FOLHA: 35 / 58		LEGENDA:							TÍTULO: PCE NEREDA			
									SUB-TÍTULO: Saídas Digitais			
		REVISÃO:		EI						UNID. BRK: SUMARÉ	MUNIC./EST.: SUMARÉ-SP	BAIRRO/ÁREA:
		DATA:		03/06/2025						RESP. TÊC.: JEAN CARLOS ESSER	APROVAÇÃO BRK AMBIENTAL:	APROVAÇÃO CLIENTE:
		EXECUÇÃO:		Luiz Corrêa						CREA: 076760-0/SC		
		VERIFICAÇÃO:		Luiz Corrêa				CÓDIGO DO PROJETO: HID-PA-DE-ETE-ELQ-005		ESCALA: 1:1	REVISÃO: EI	
		APROVAÇÃO:		Rafael Decker				CONTRATANTE: BRK AMBIENTAL	CONTRATO Nº: 230317			

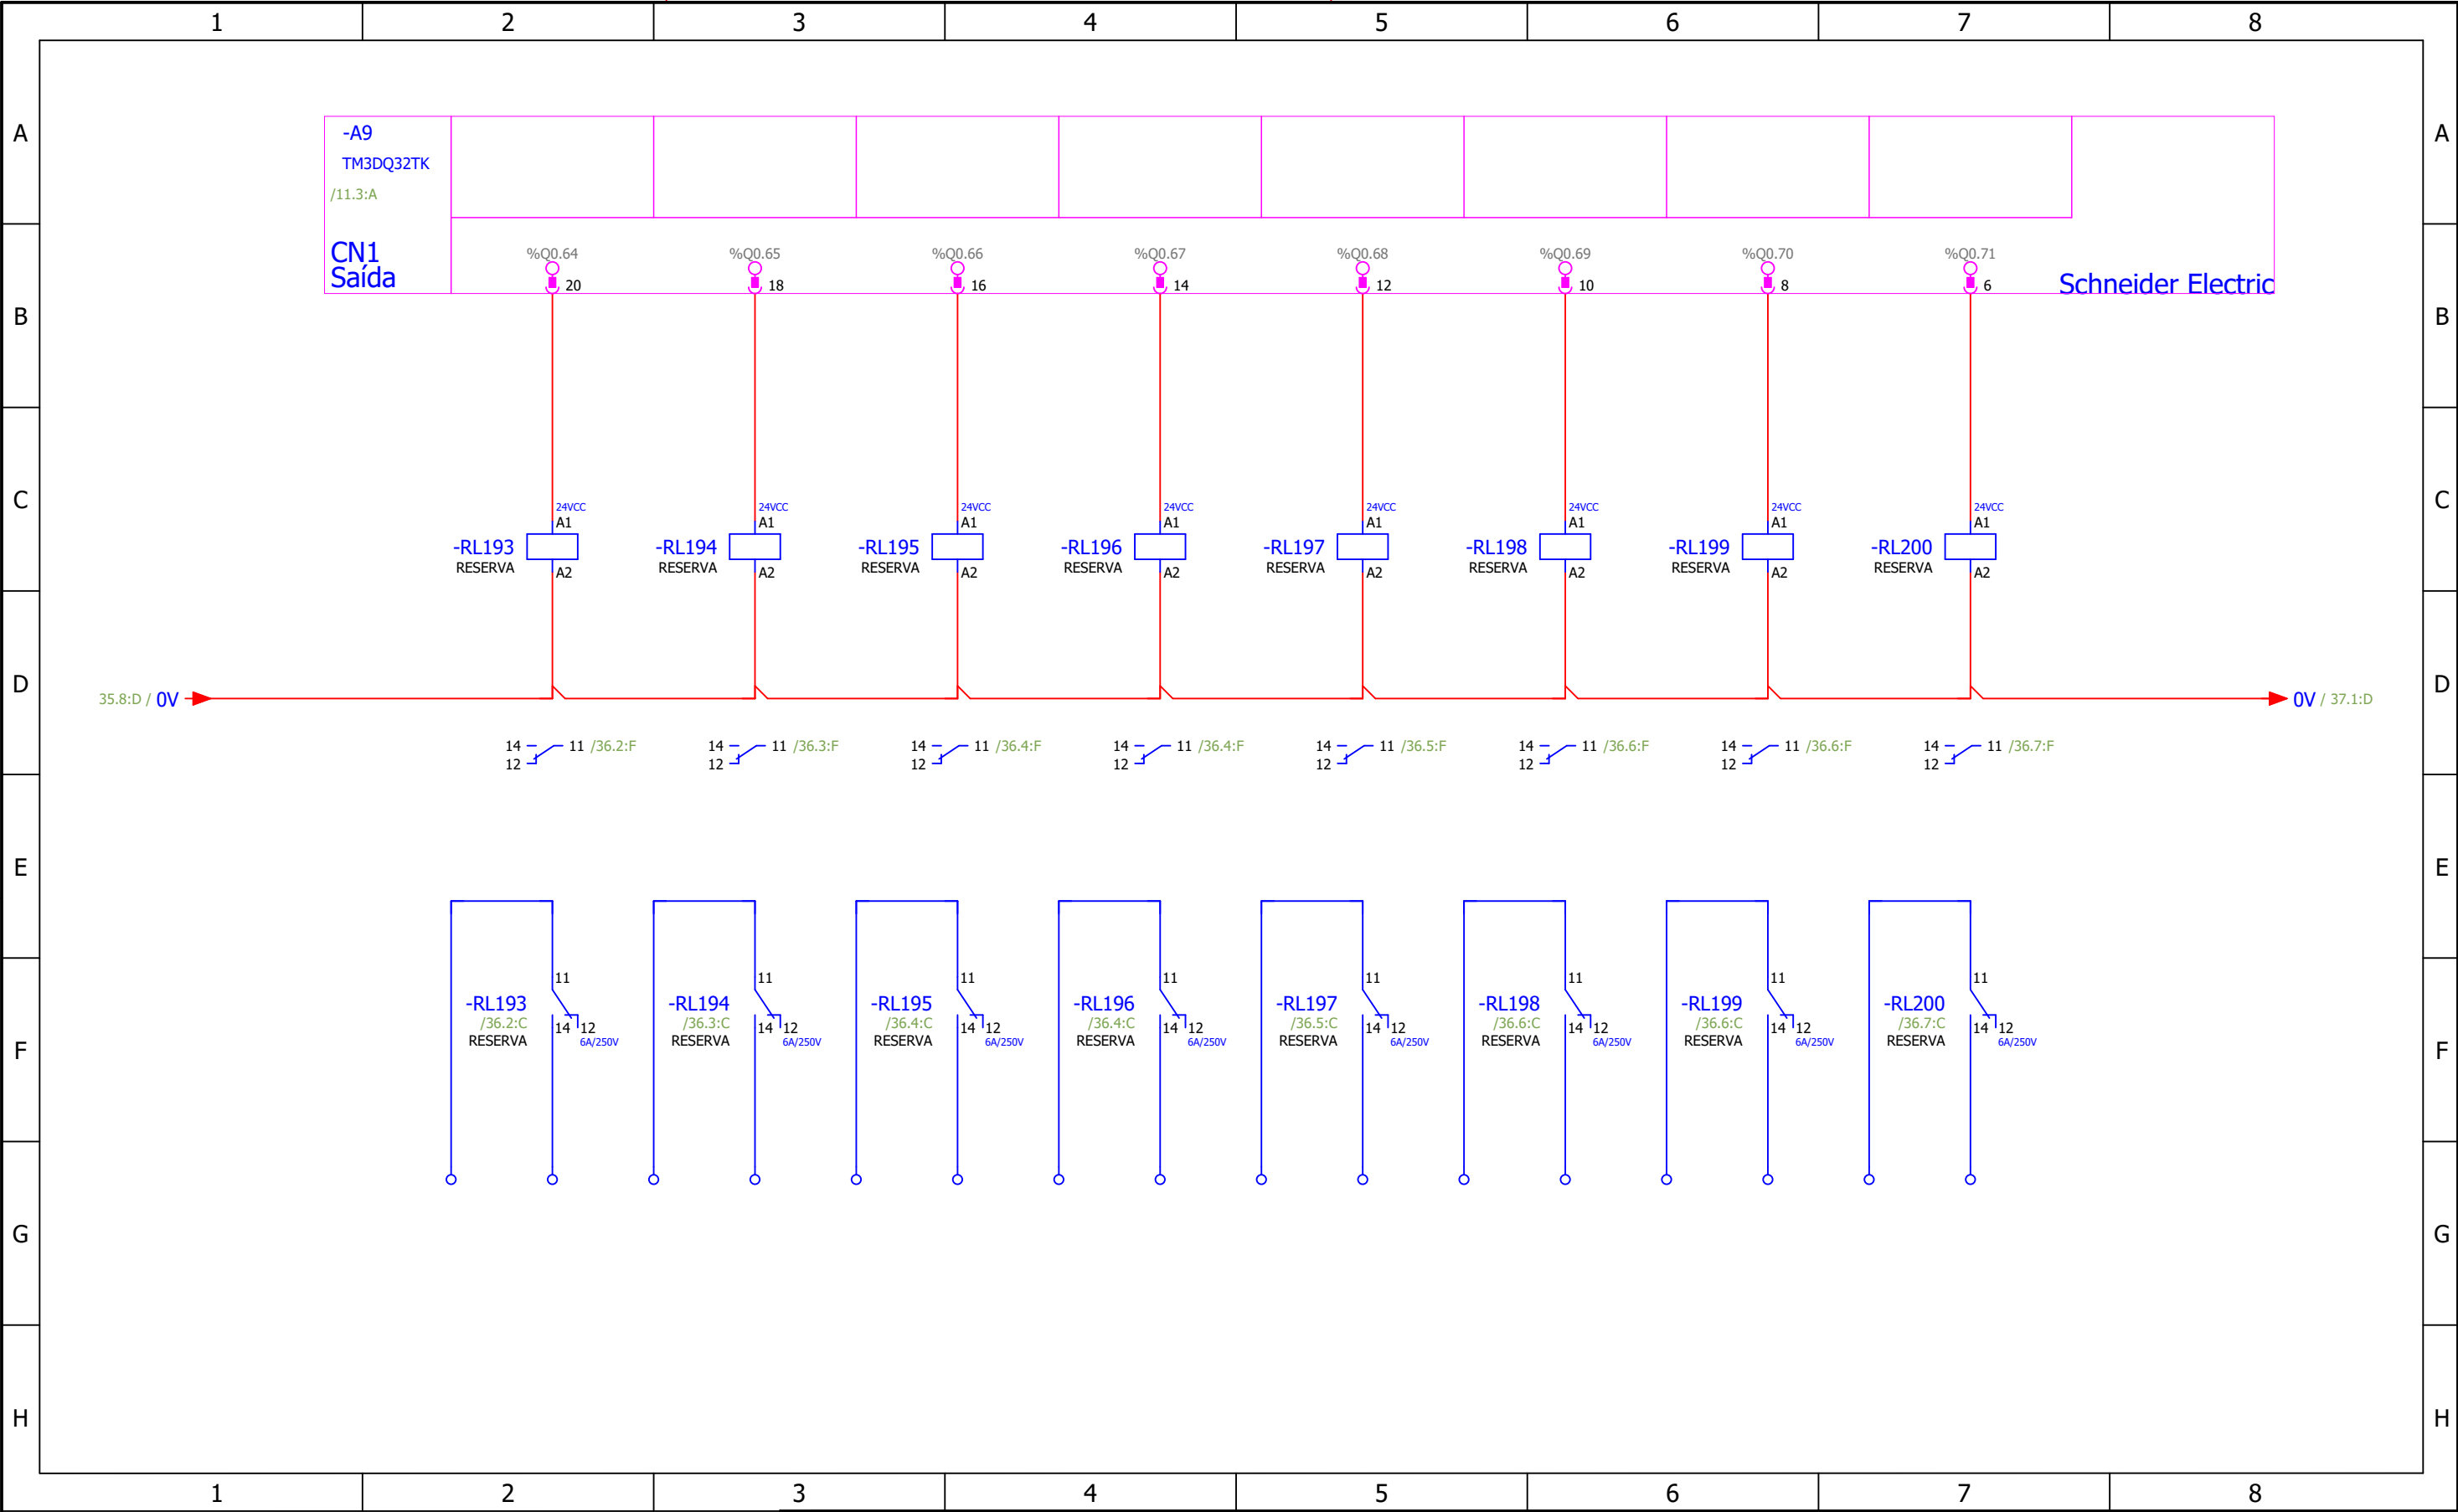



FOLHA: 36 / 58			LEGENDA:							TÍTULO: PCE NEREDA										
										SUB-TÍTULO:										
								Saídas Digitais												
								UNID. BRK: SUMARÉ		MUNIC./EST.: SUMARÉ-SP		BAIRRO/ÁREA:								
			DATA: 03/06/2025		EI								RESP. TÊC.: JEAN CARLOS ESSER 076760-0/SC		APROVAÇÃO BRK AMBIENTAL:		APROVAÇÃO CLIENTE: BRK			
EXECUÇÃO: Luiz Corrêa																				
VERIFICAÇÃO: Luiz Corrêa																				
APROVAÇÃO: Rafael Decker										CONTRATANTE: BRK AMBIENTAL		CONTRATO Nº: 230317		CÓDIGO DO PROJETO: HID-PA-DE-ETE-ELQ-005			ESCALA: 1:1		REVISÃO: EI	

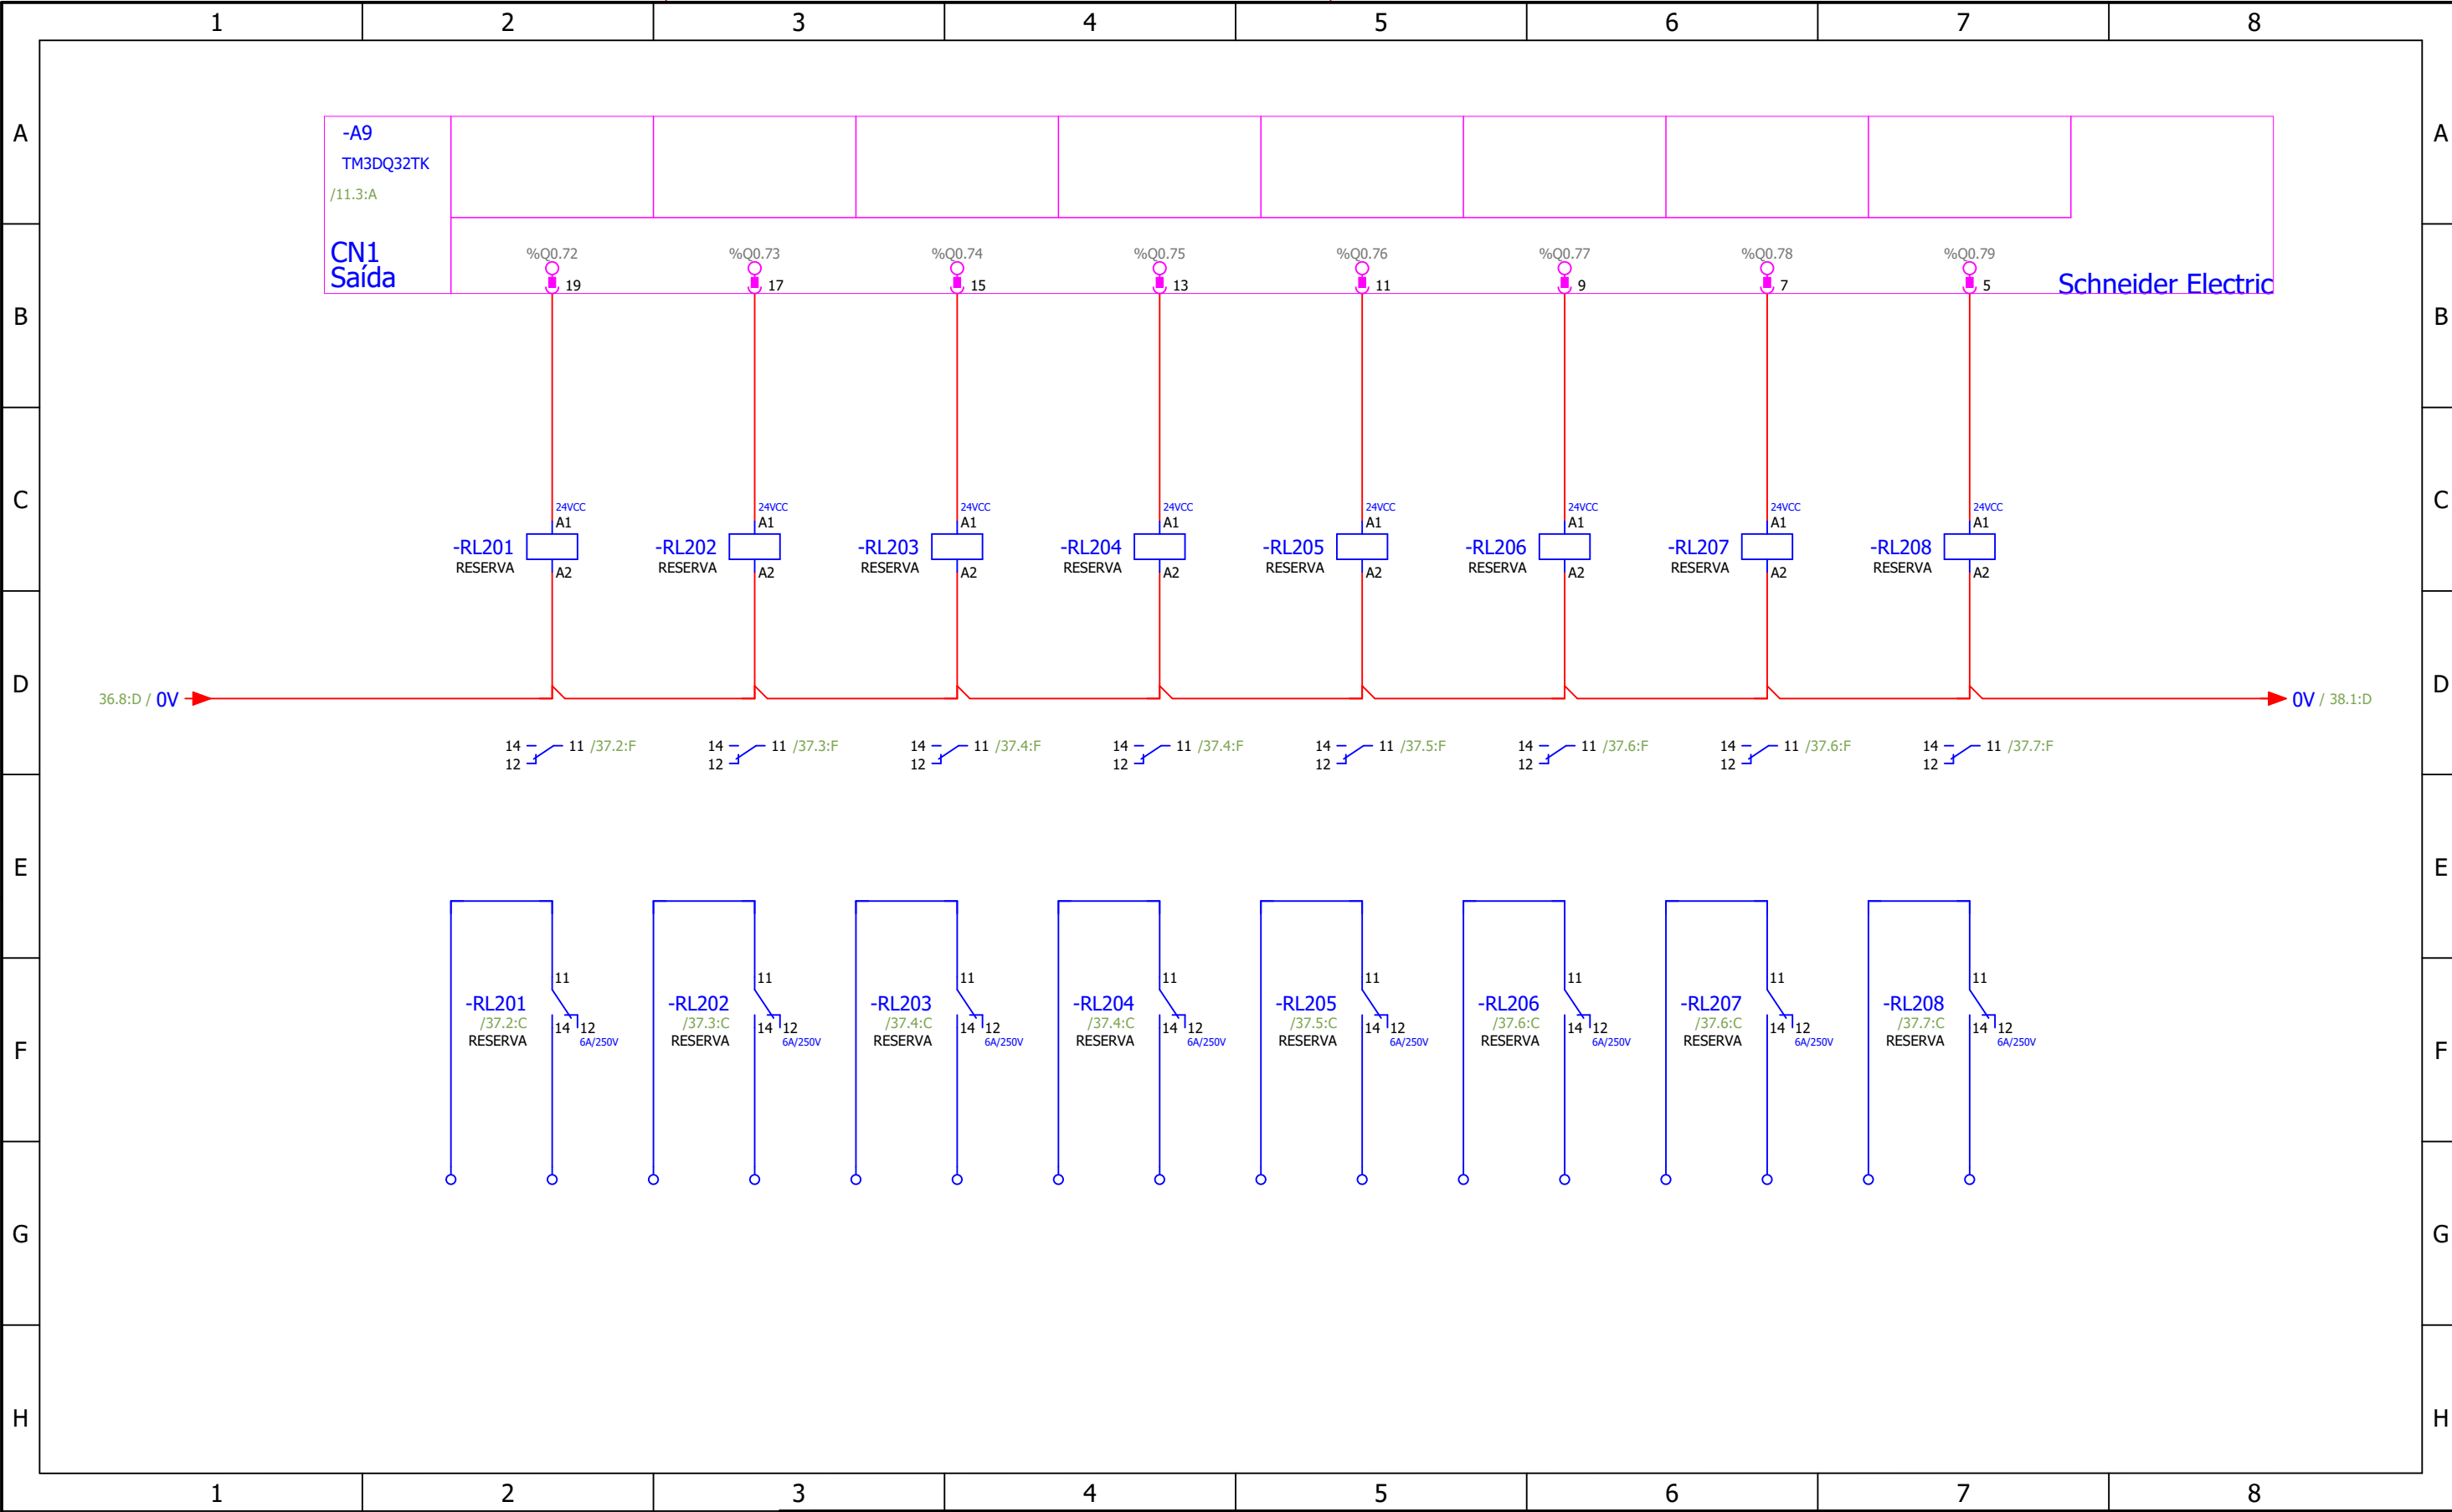

 
FOLHA: 37 / 58		LEGENDA:							TÍTULO: PCE NEREDA						
									SUB-TÍTULO: Saídas Digitais						
		REVISÃO:		EI						UNID. BRK: SUMARÉ		MUNIC./EST.: SUMARÉ-SP		BAIRRO/ÁREA:	
		DATA:		03/06/2025						RESP. TÊC.: JEAN CARLOS ESSER 076760-0/SC		APROVAÇÃO BRK AMBIENTAL:		APROVAÇÃO CLIENTE: BRK	
EXECUÇÃO:		Luiz Corrêa				CONTRATANTE: BRK AMBIENTAL				CONTRATO Nº: 230317		CÓDIGO DO PROJETO: HID-PA-DE-ETE-ELQ-005		ESCALA: 1:1	
		VERIFICAÇÃO:		Luiz Corrêa											
		APROVAÇÃO:		Rafael Decker											

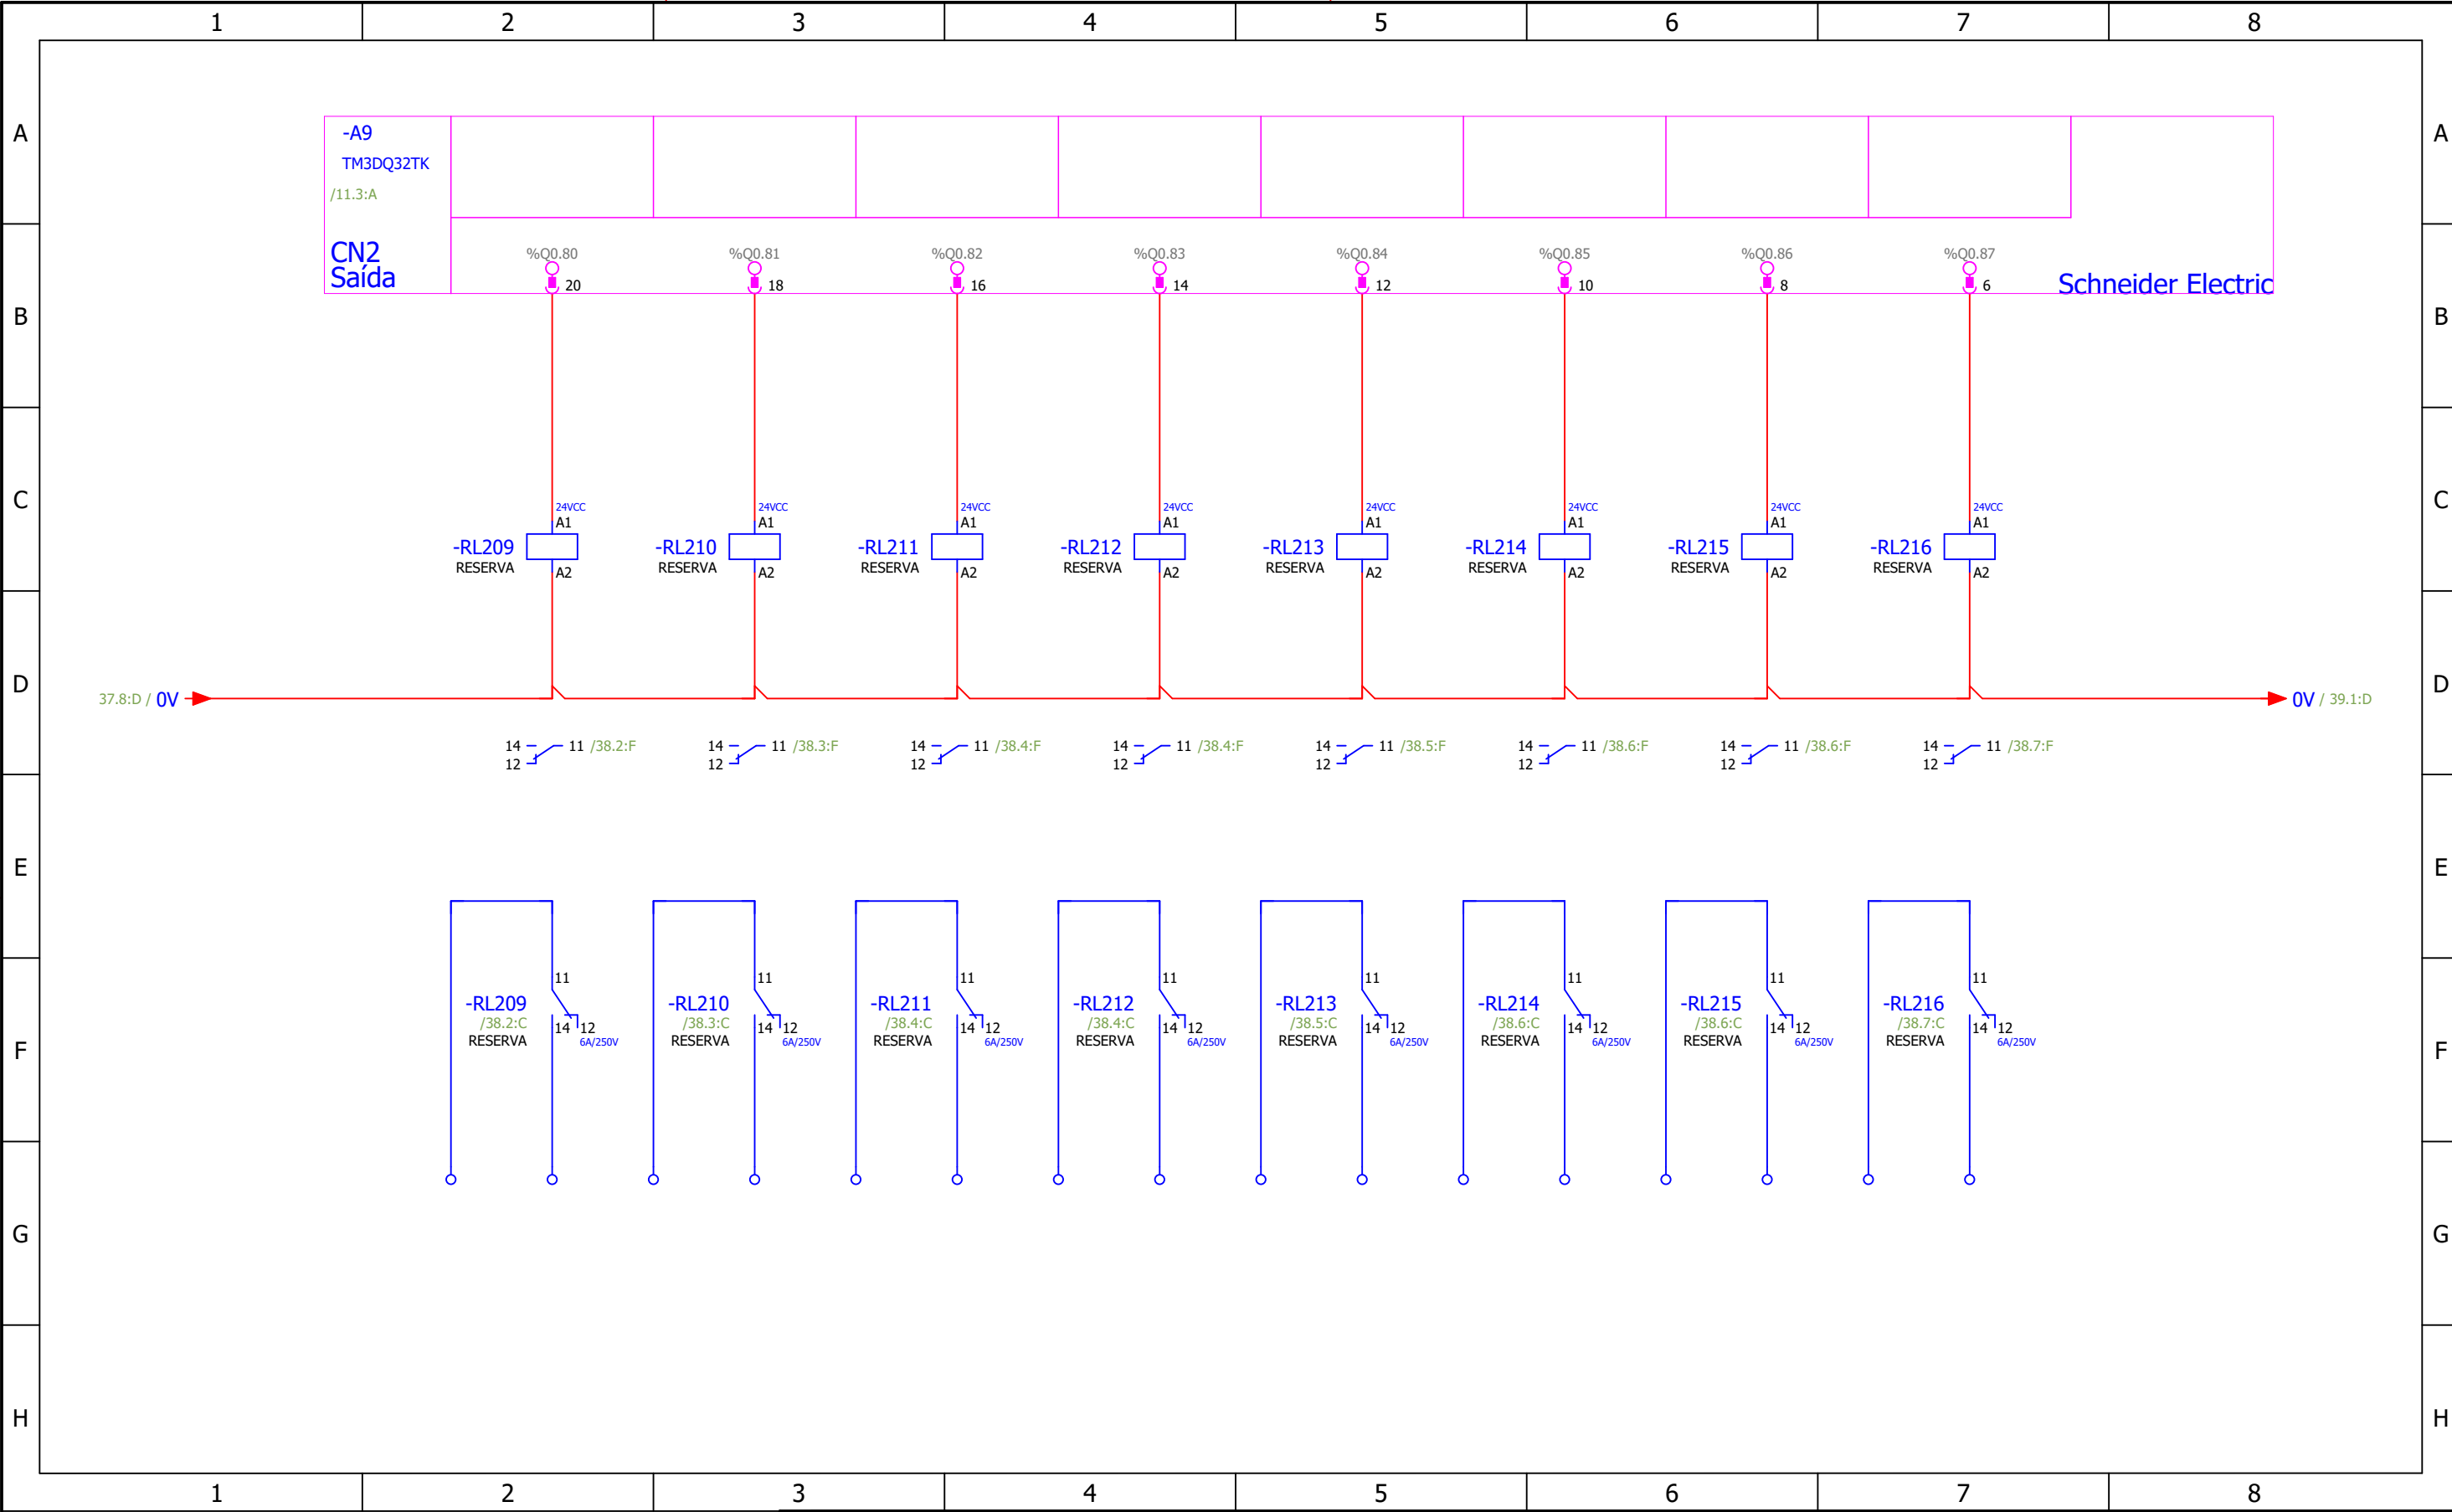

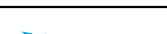
FOLHA: 38 / 58		LEGENDA:							TÍTULO: PCE NEREDA			
									SUB-TÍTULO: Saídas Digitais			
		REVISÃO:		EI						UNID. BRK: SUMARÉ	MUNIC./EST.: SUMARÉ-SP	BAIRRO/ÁREA:
		DATA:		03/06/2025						RESP. TÊC.: JEAN CARLOS ESSER 076760-0/SC	APROVAÇÃO BRK AMBIENTAL:	APROVAÇÃO CLIENTE: BRK
		EXECUÇÃO:		Luiz Corrêa						CREA:	CÓDIGO DO PROJETO: HID-PA-DE-ETE-ELQ-005	
VERIFICAÇÃO:		Luiz Corrêa				CONTRATANTE: BRK AMBIENTAL	CONTRATO Nº: 230317					
APROVAÇÃO:		Rafael Decker										

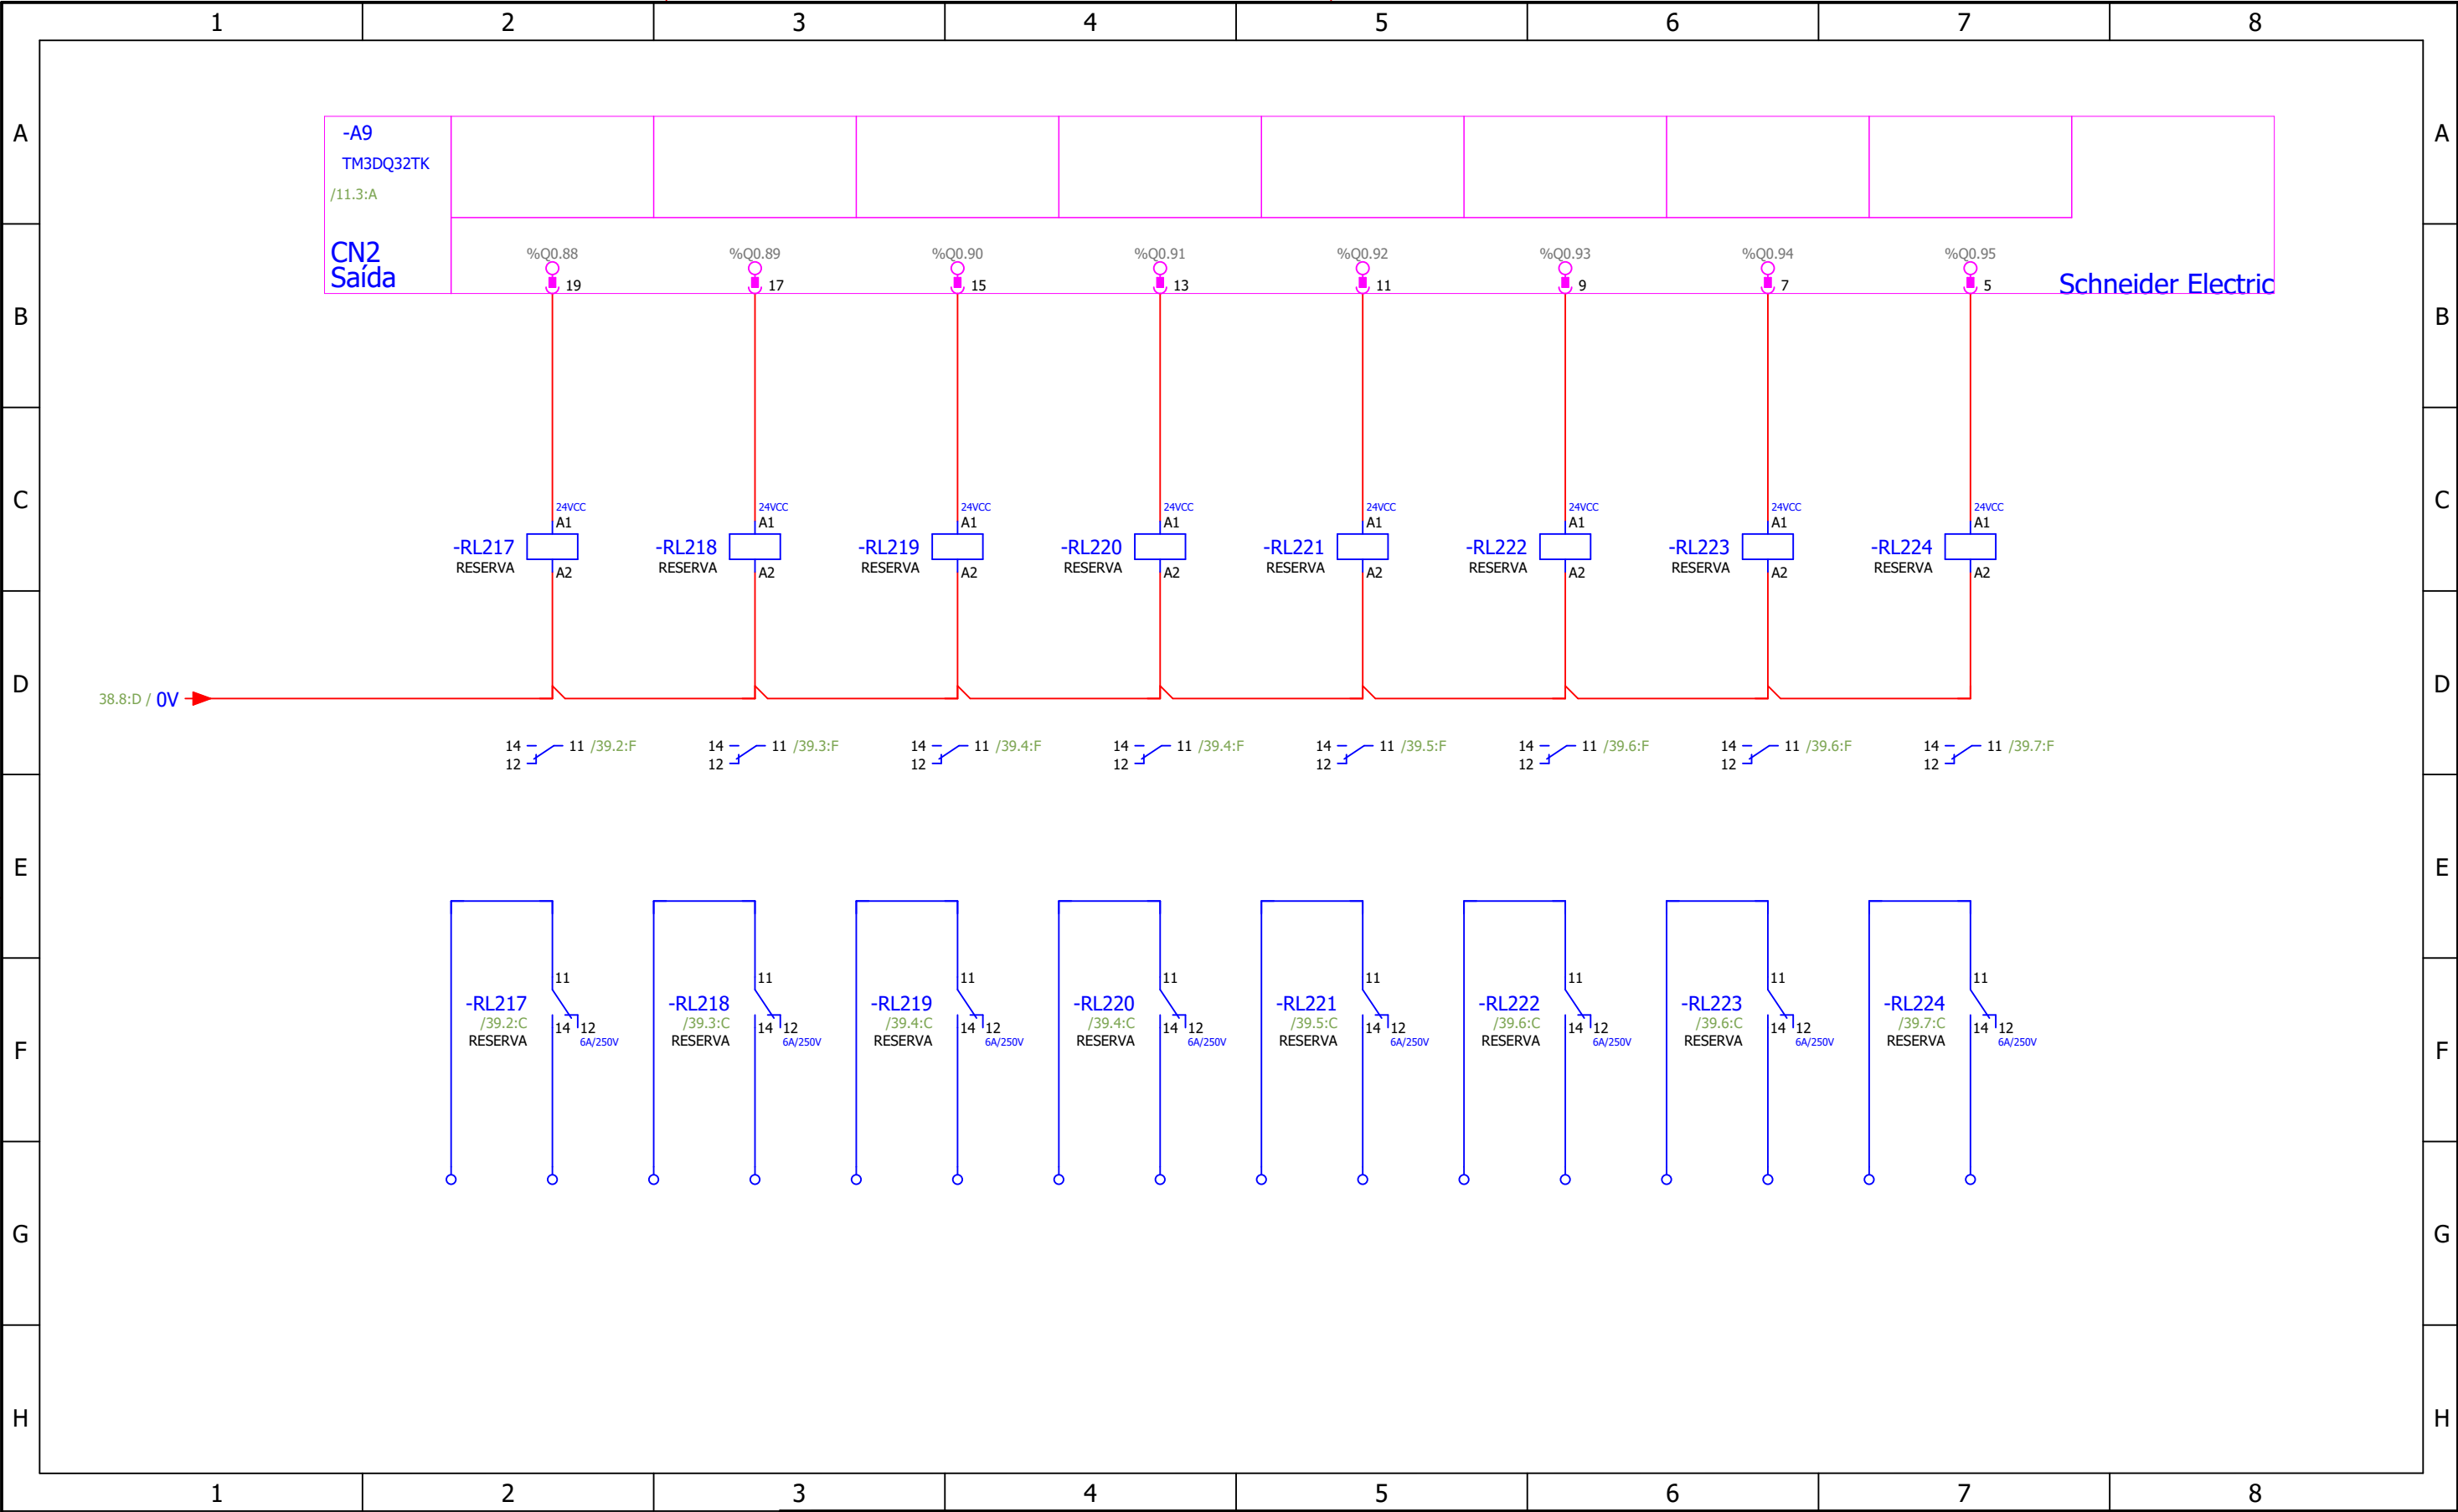

FOLHA: 39 / 58		LEGENDA:							TÍTULO: PCE NEREDA							
									SUB-TÍTULO: Saídas Digitais							
		REVISÃO:		EI						UNID. BRK: SUMARÉ		MUNIC./EST.: SUMARÉ-SP		BAIRRO/ÁREA:		
		DATA:		03/06/2025						RESP. TÊC.: JEAN CARLOS ESSER		APROVAÇÃO BRK AMBIENTAL:		APROVAÇÃO CLIENTE: BRK		
		EXECUÇÃO:		Luiz Corrêa						CREA: 076760-0/SC						
VERIFICAÇÃO:		Luiz Corrêa				CONTRATANTE: BRK AMBIENTAL		CONTRATO Nº: 230317		CÓDIGO DO PROJETO: HID-PA-DE-ETE-ELQ-005			ESCALA: 1:1		REVISÃO: EI	
APROVAÇÃO:		Rafael Decker														

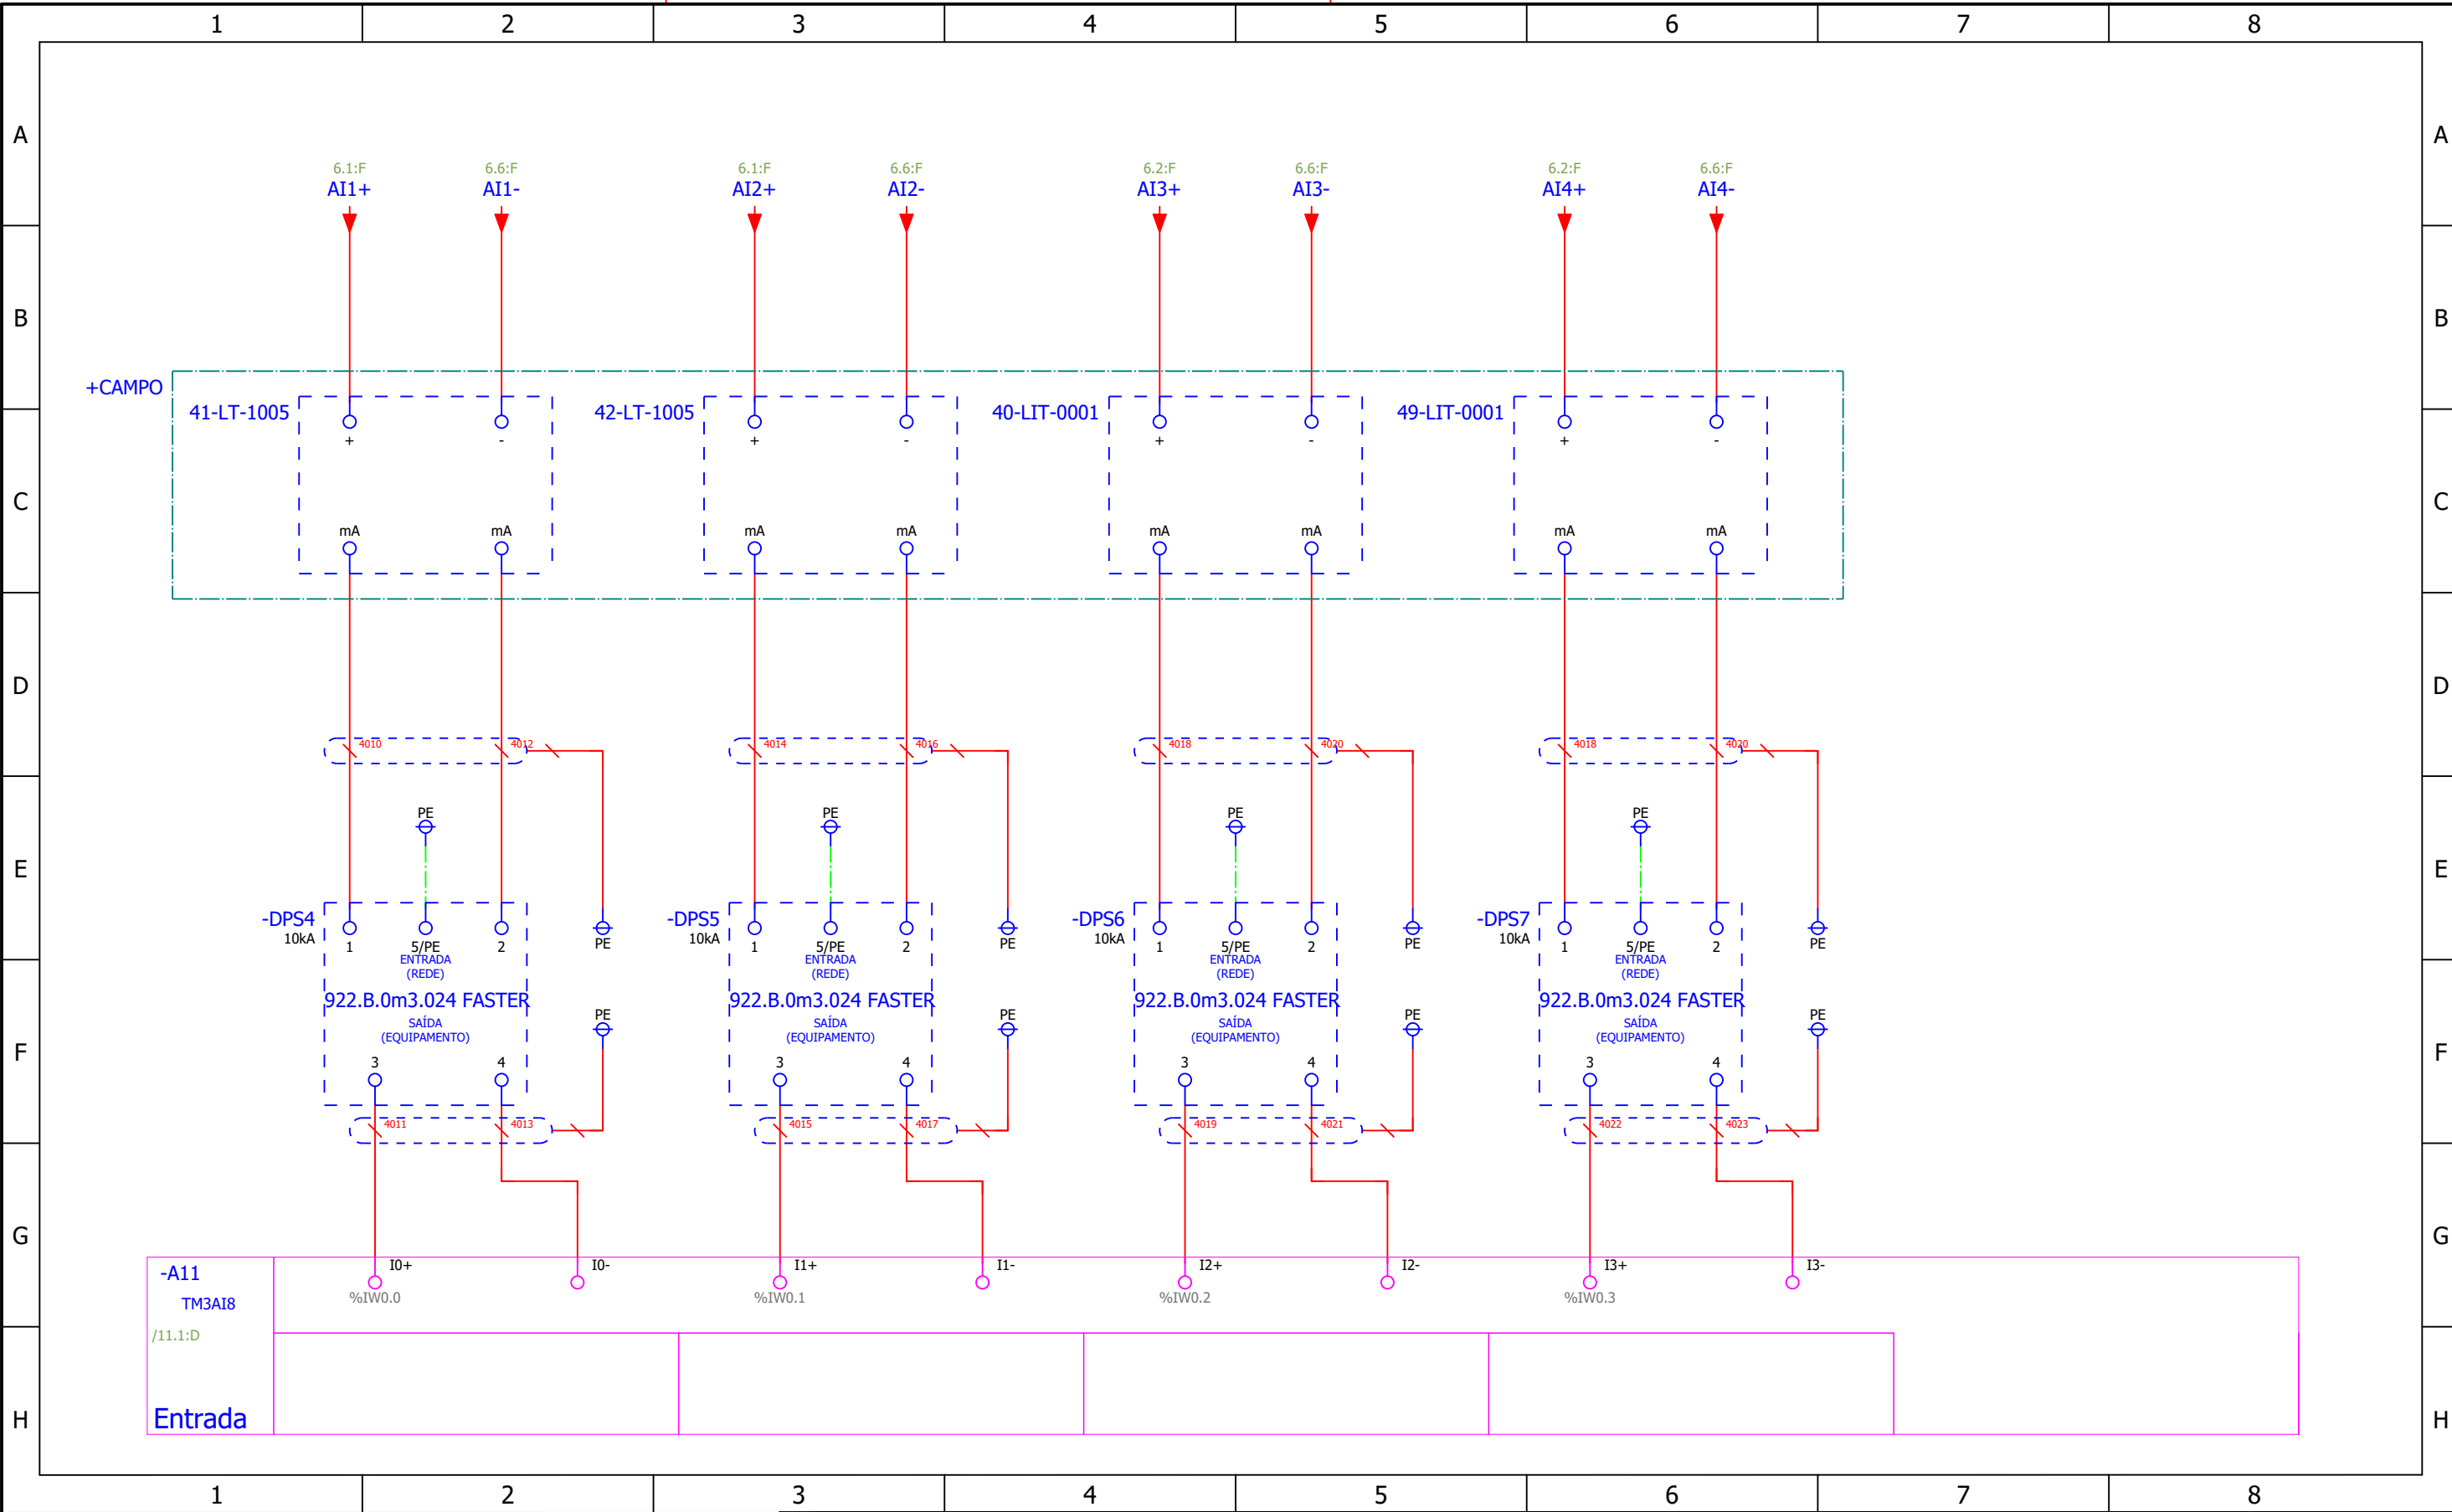

FOLHA: 40 / 58		LEGENDA:						TÍTULO: PCE NEREDA						
								SUB-TÍTULO: Entradas Analógicas						
		REVISÃO:	EI						UNID. BRK:	SUMARÉ	MUNIC./EST.:	SUMARÉ-SP	BAIRRO/ÁREA:	
		DATA:	03/06/2025						RESP. TÊC.:	JEAN CARLOS ESSER	APROVAÇÃO BRK AMBIENTAL:	APROVAÇÃO CLIENTE:		
		EXECUÇÃO:	Luiz Corrêa						CREA:	076760-0/SC		BRK		
VERIFICAÇÃO:	Luiz Corrêa				CÓDIGO DO PROJETO:				ESCALA:	REVISÃO:				
		APROVAÇÃO:	Rafael Decker				CONTRATANTE:	CONTRATO Nº:	HID-PA-DE-ETE-ELQ-005			1:1	EI	
							BRK AMBIENTAL	230317						

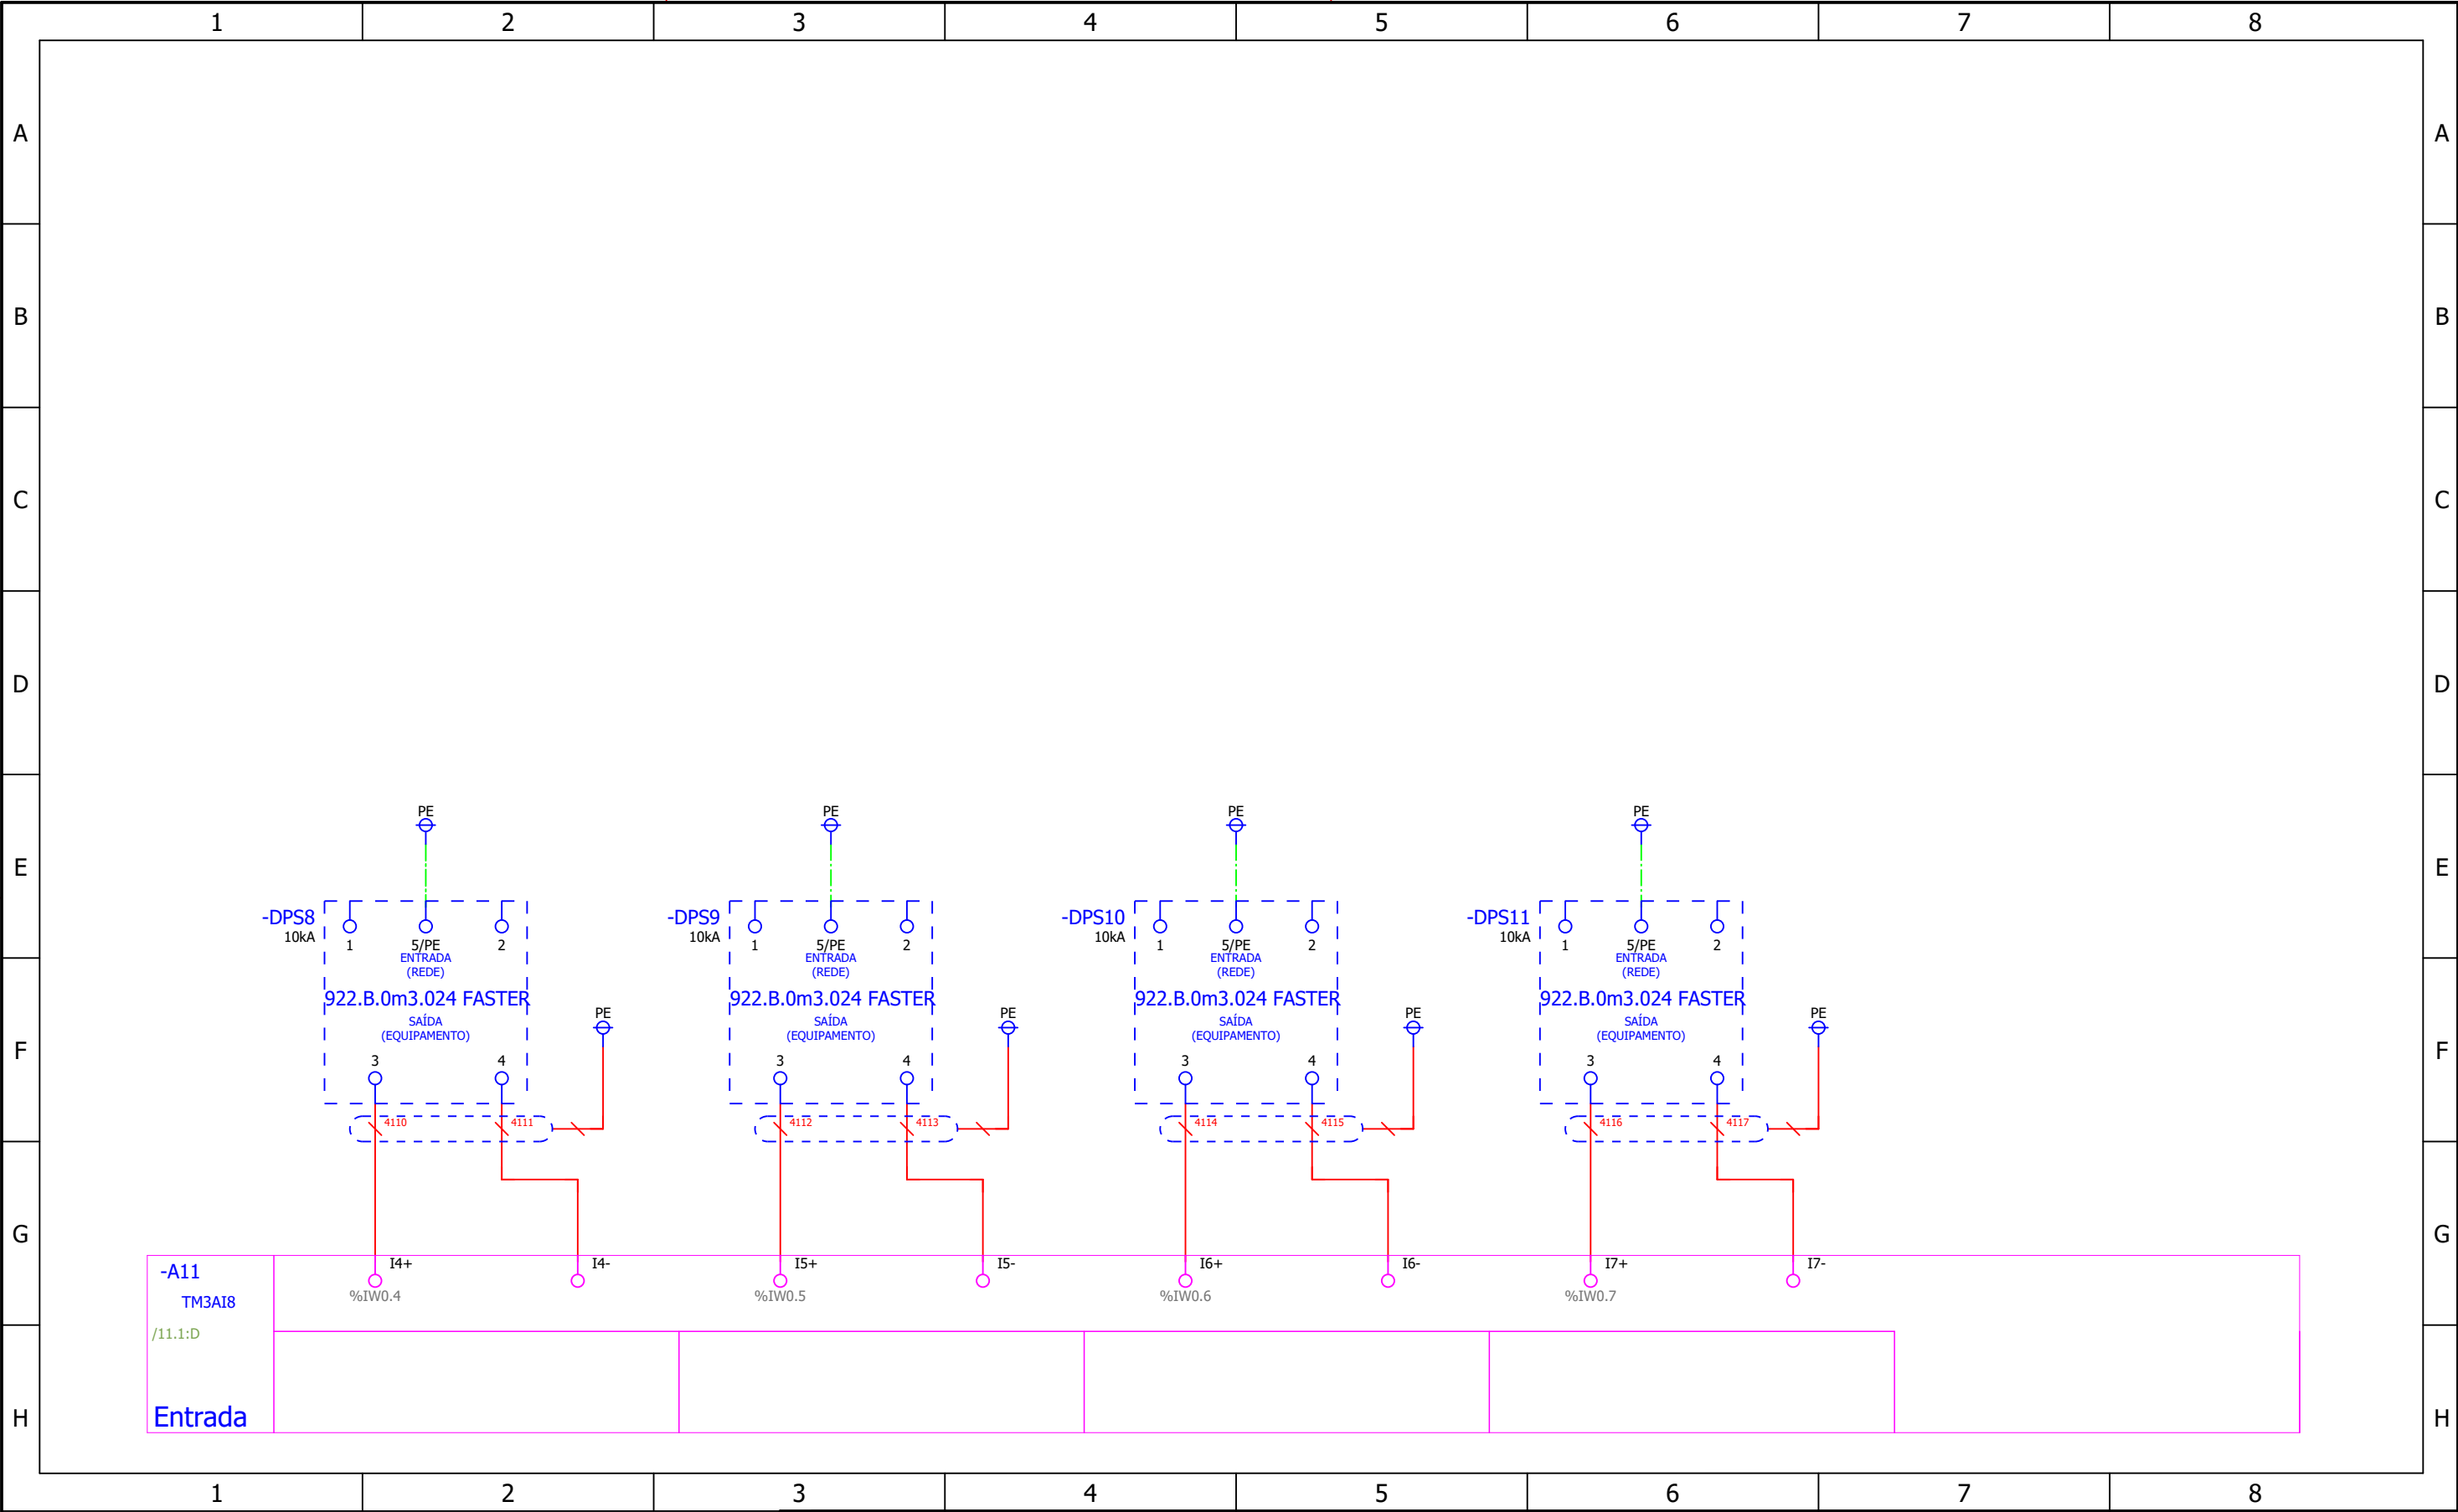

-A11
TM3AI8
/11.1:D
Entrada


LEGENDA:				
REVISÃO:	EI			
DATA:	03/06/2025			
EXECUÇÃO:	Luiz Corrêa			
VERIFICAÇÃO:	Luiz Corrêa			
APROVAÇÃO:	Rafael Decker			





CONTRATANTE: BRK AMBIENTAL
CONTRATO Nº: 230317

TÍTULO: PCE NEREDA		
SUB-TÍTULO: Entradas Analógicas		
UNID. BRK: SUMARÉ	MUNIC./EST.: SUMARÉ-SP	BAIRRO/ÁREA:
RESP. TÊC.: JEAN CARLOS ESSER	APROVAÇÃO BRK AMBIENTAL:	APROVAÇÃO CLIENTE: BRK
CREA: 076760-0/SC		
CÓDIGO DO PROJETO: HID-PA-DE-ETE-ELQ-005		ESCALA: 1:1
		REVISÃO: EI

FOLHA: 41 / 58

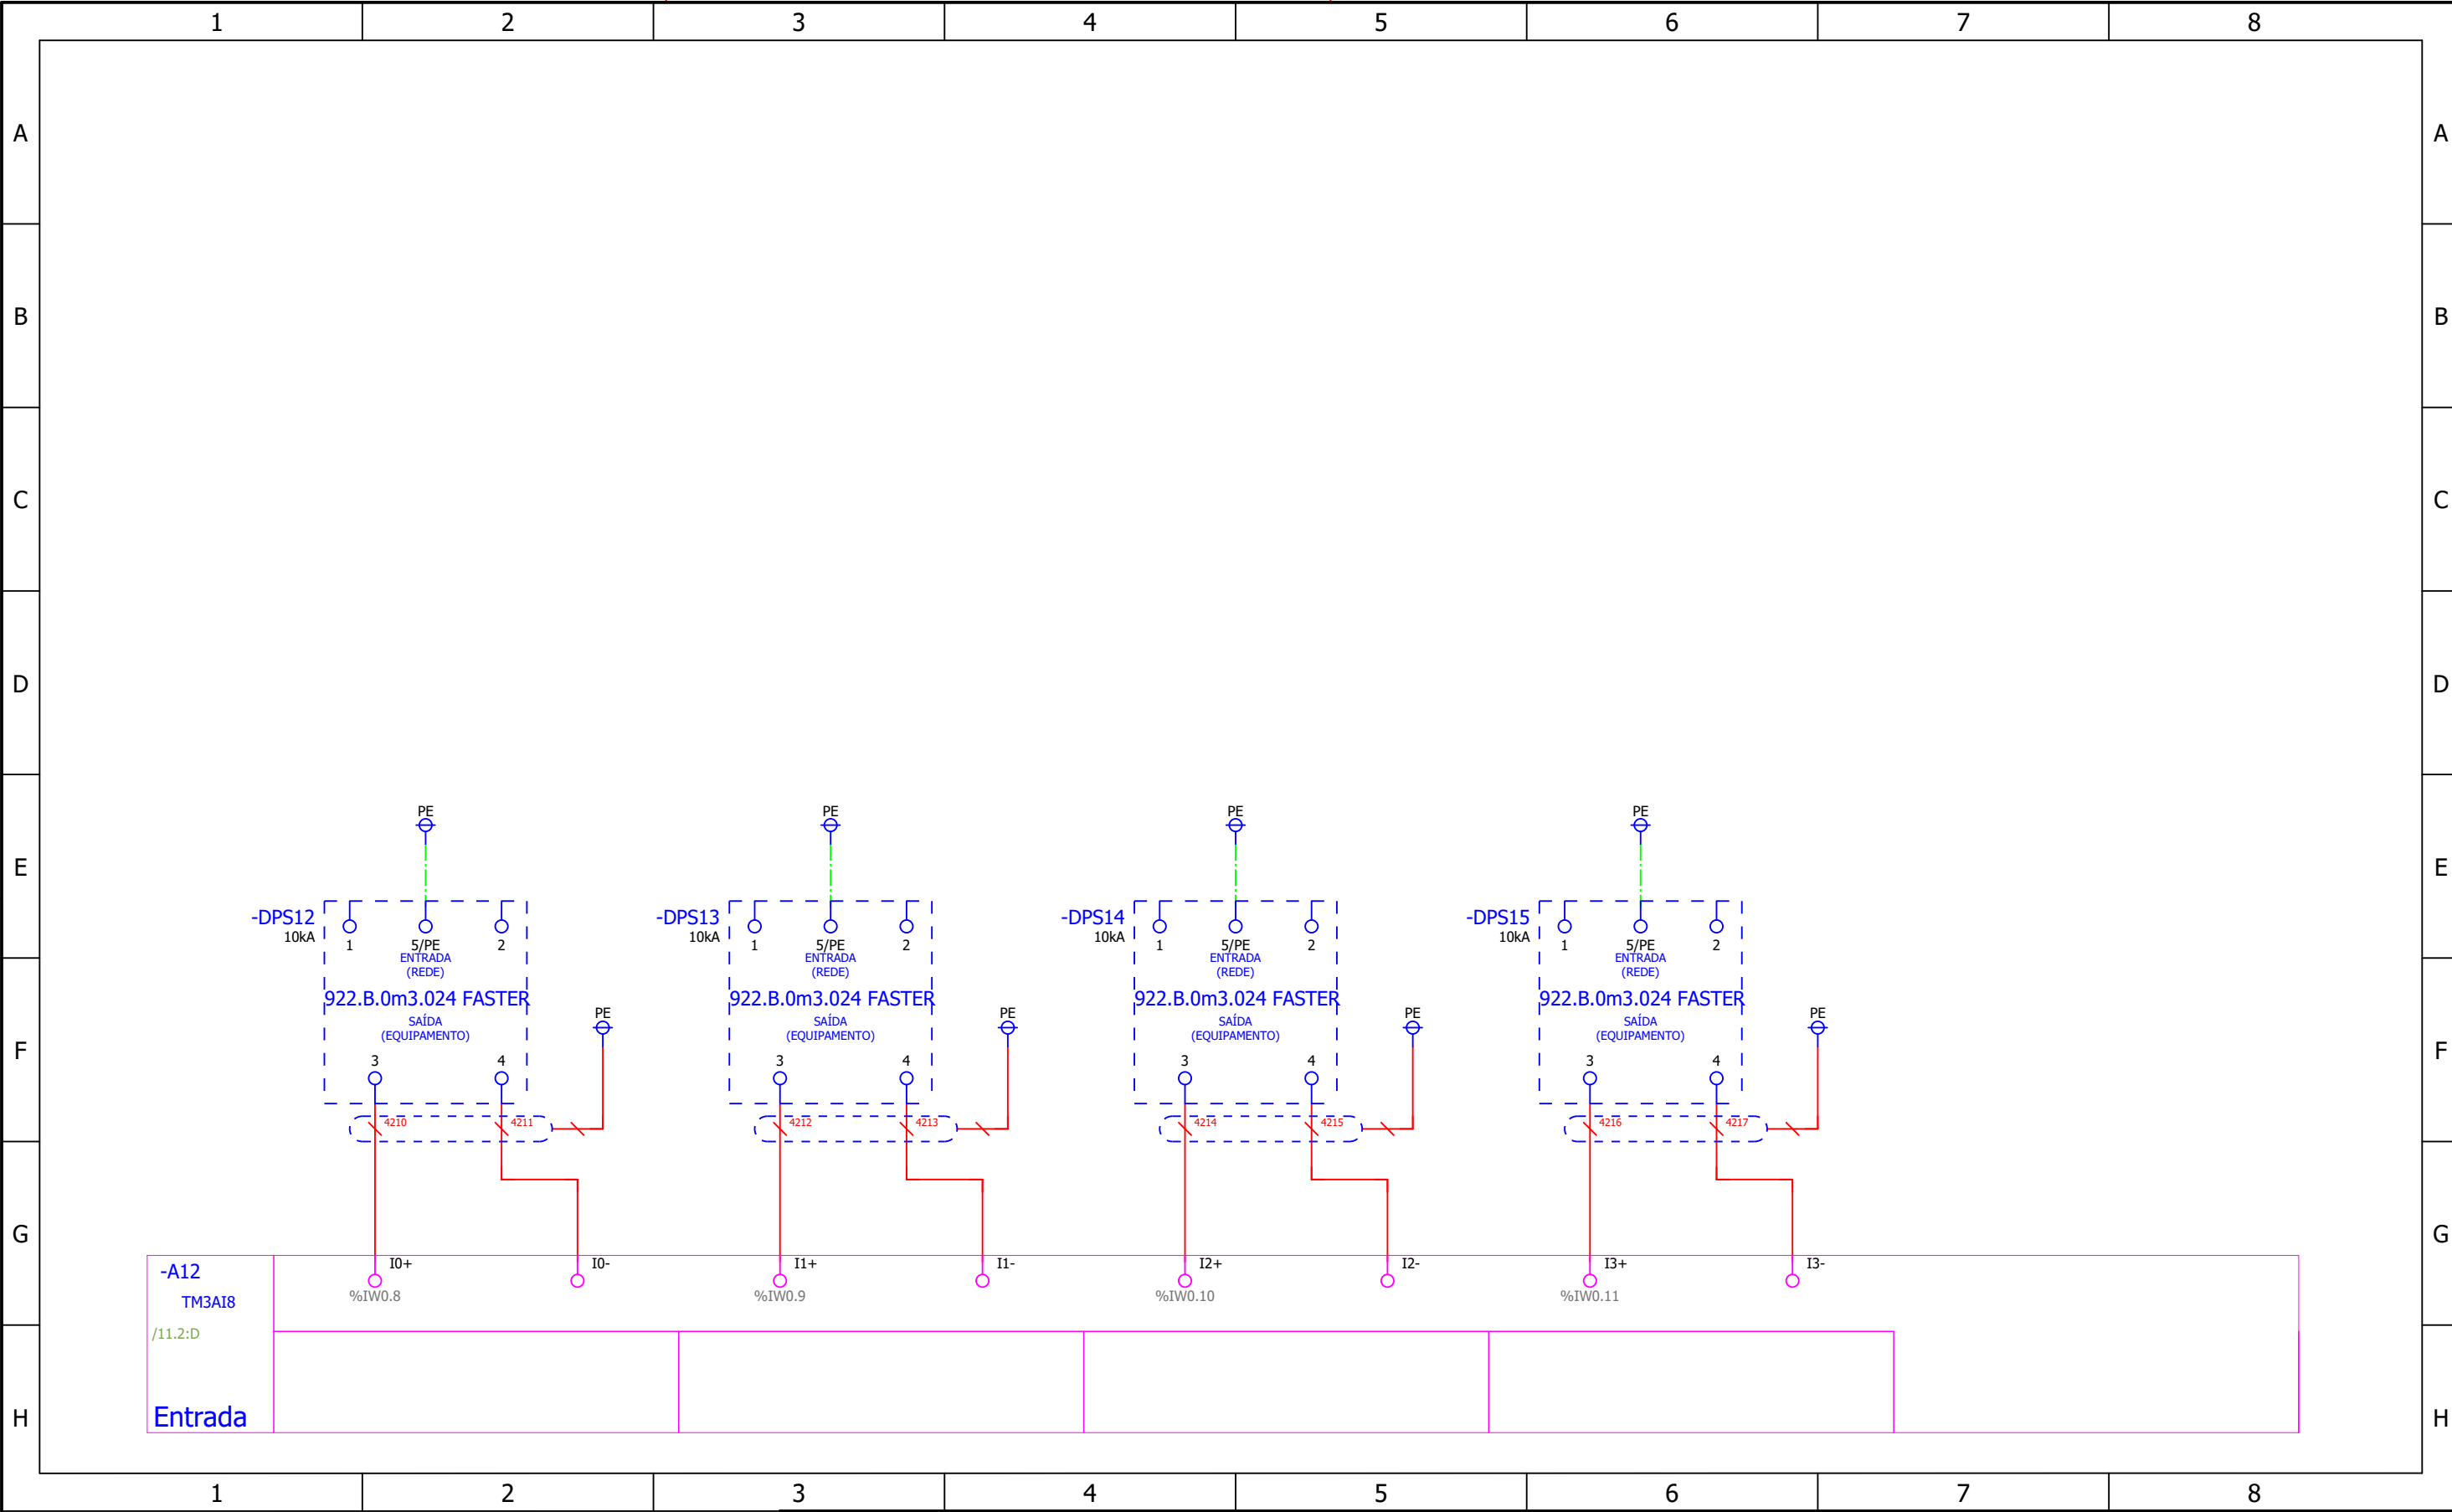

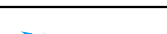FOLHA: 42 / 58		LEGENDA:							TÍTULO: PCE NEREDA							
									SUB-TÍTULO: Entradas Analógicas							
		REVISÃO:		EI							UNID. BRK: SUMARÉ		MUNIC./EST.: SUMARÉ-SP		BAIRRO/ÁREA:	
		DATA:		03/06/2025							RESP. TÊC.: JEAN CARLOS ESSER		APROVAÇÃO BRK AMBIENTAL:		APROVAÇÃO CLIENTE: BRK	
		EXECUÇÃO:		Luiz Corrêa							CREA: 076760-0/SC					
VERIFICAÇÃO:		Luiz Corrêa					CÓDIGO DO PROJETO: HID-PA-DE-ETE-ELQ-005				ESCALA: 1:1		REVISÃO: EI			
		APROVAÇÃO:		Rafael Decker					CONTRATANTE: BRK AMBIENTAL		CONTRATO Nº: 230317					

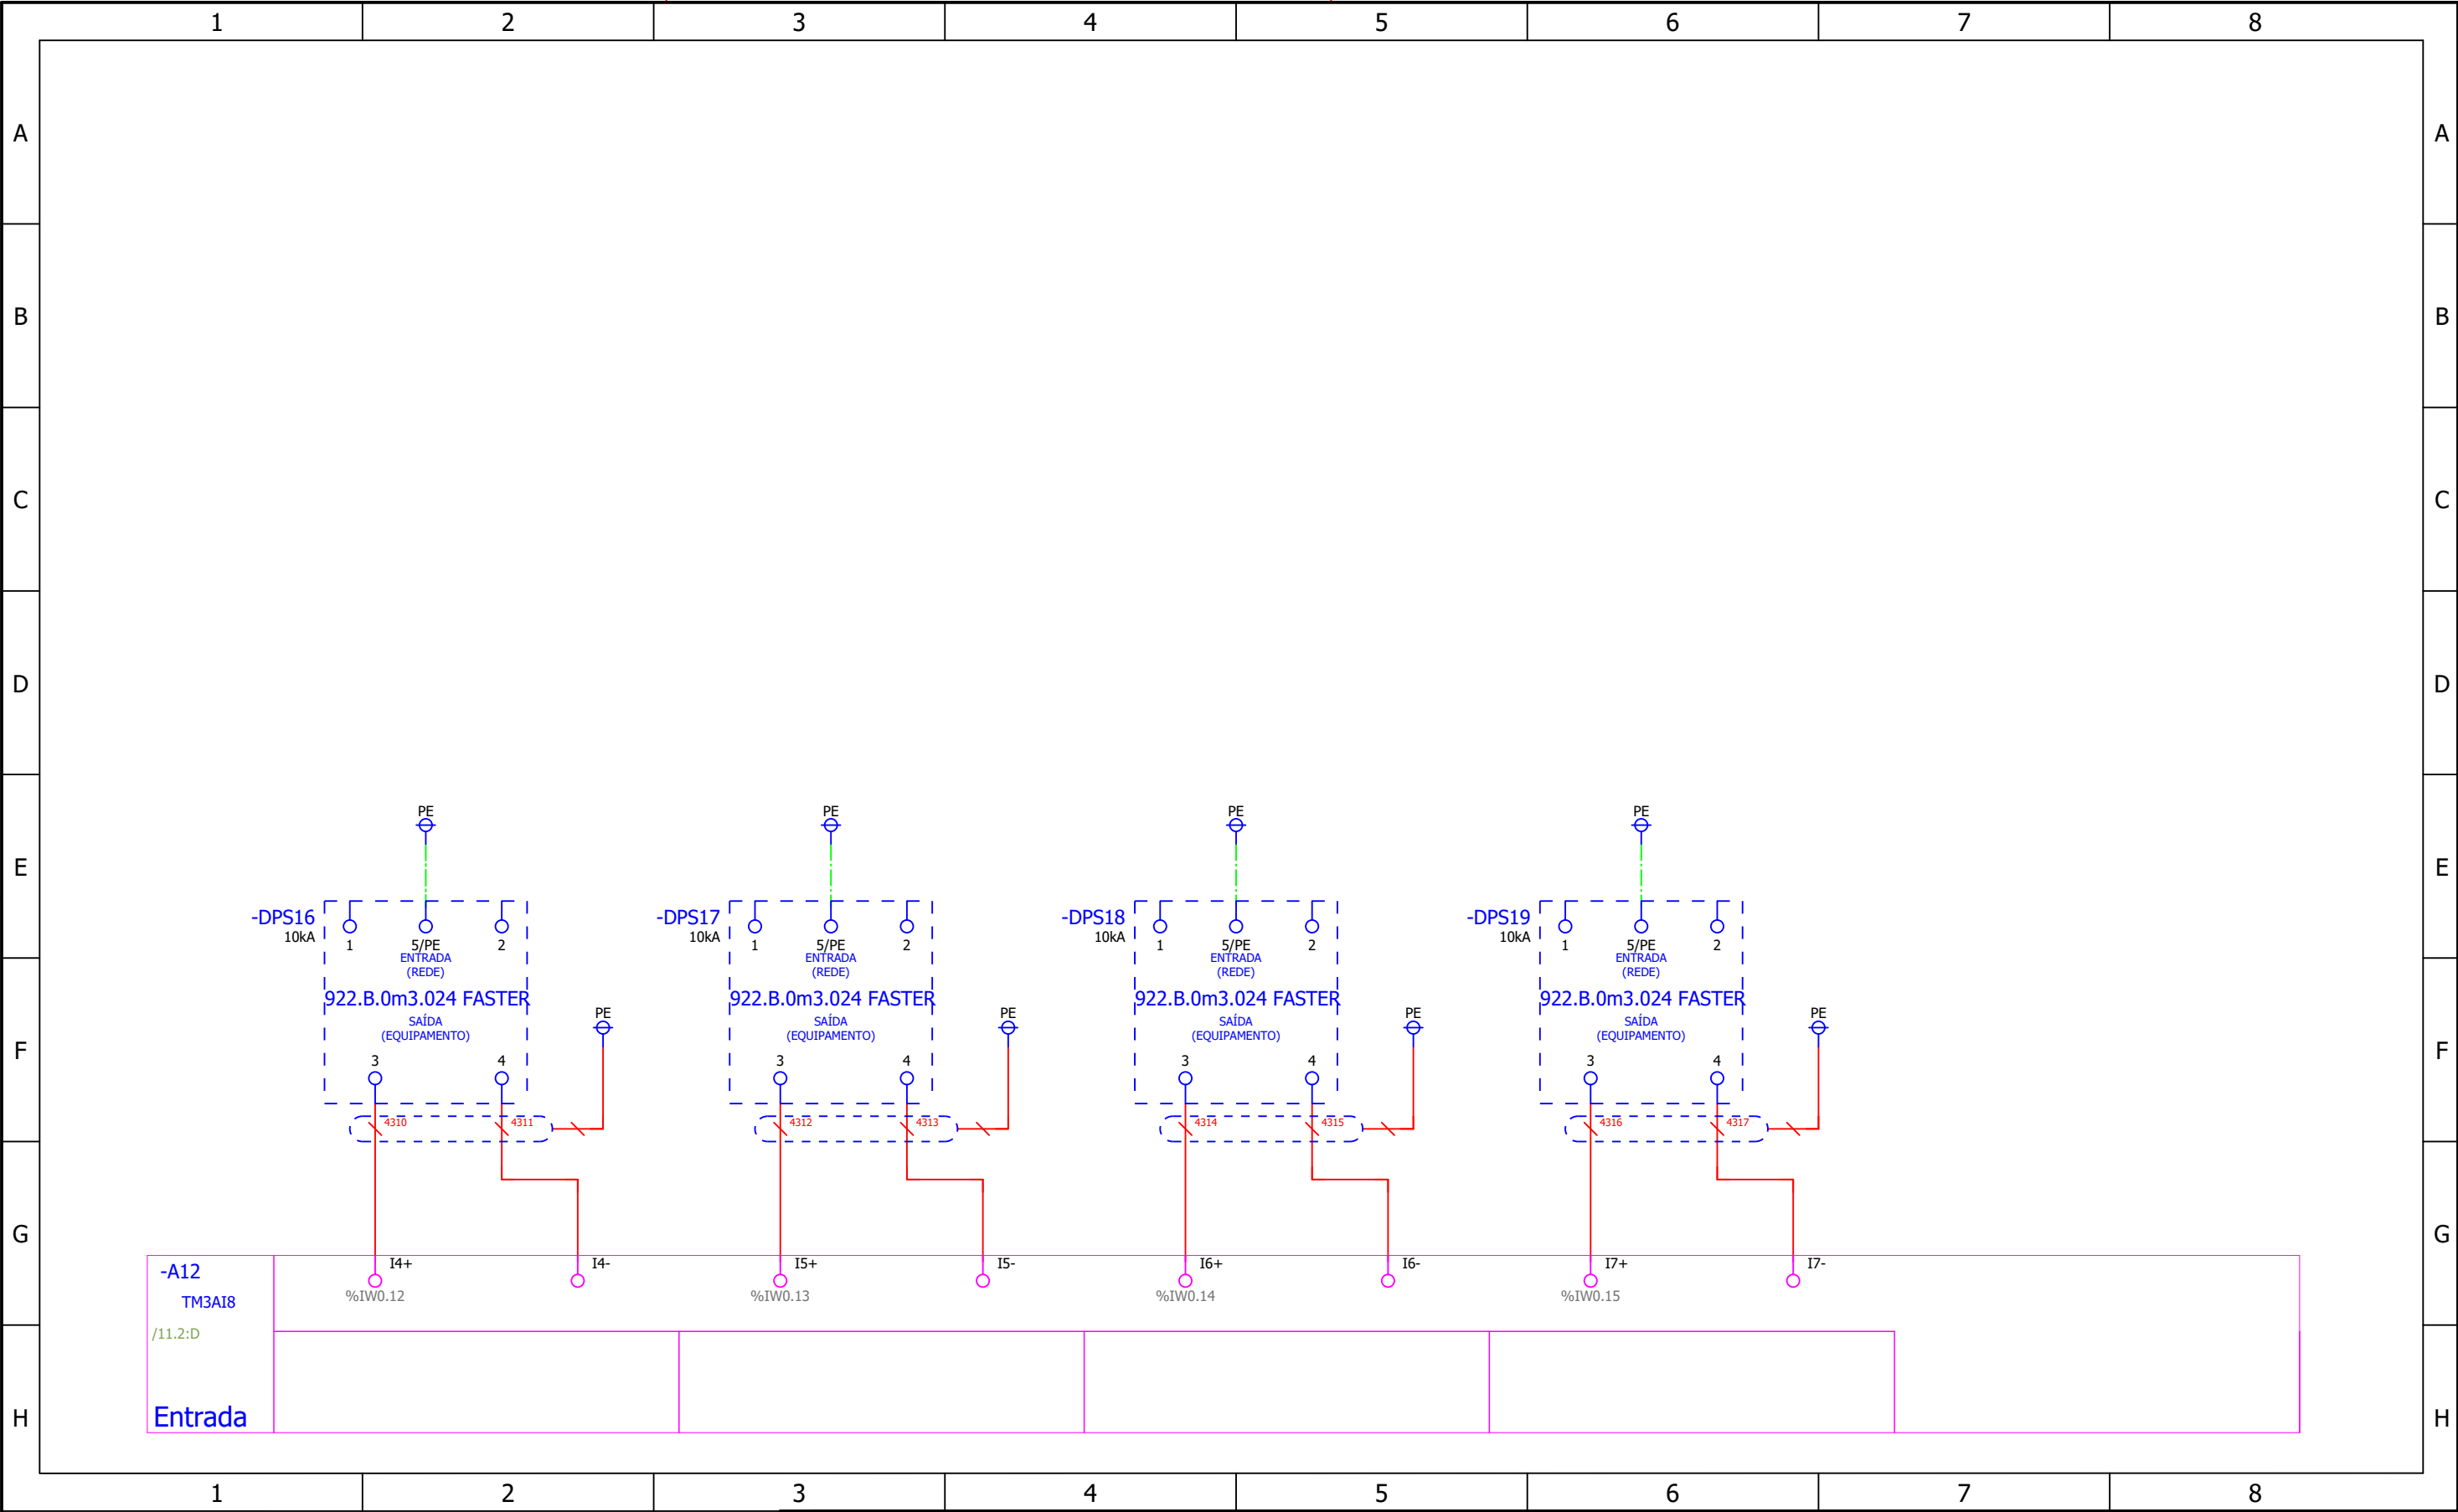

-A12
TM3AI8
/11.2:D
Entrada


LEGENDA:				
REVISÃO:	EI			
DATA:	03/06/2025			
EXECUÇÃO:	Luiz Corrêa			
VERIFICAÇÃO:	Luiz Corrêa			
APROVAÇÃO:	Rafael Decker			



CONTRATANTE:
BRK AMBIENTAL

CONTRATO Nº:
230317

TÍTULO: PCE NEREDA		
SUB-TÍTULO: Entradas Analógicas		
UNID. BRK: SUMARÉ	MUNIC./EST.: SUMARÉ-SP	BAIRRO/ÁREA:
RESP. TÉC.: JEAN CARLOS ESSER 076760-0/SC	APROVAÇÃO BRK AMBIENTAL:	APROVAÇÃO CLIENTE: BRK
CÓDIGO DO PROJETO: HID-PA-DE-ETE-ELQ-005		ESCALA: 1:1
FORMATO:		REVISÃO: EI

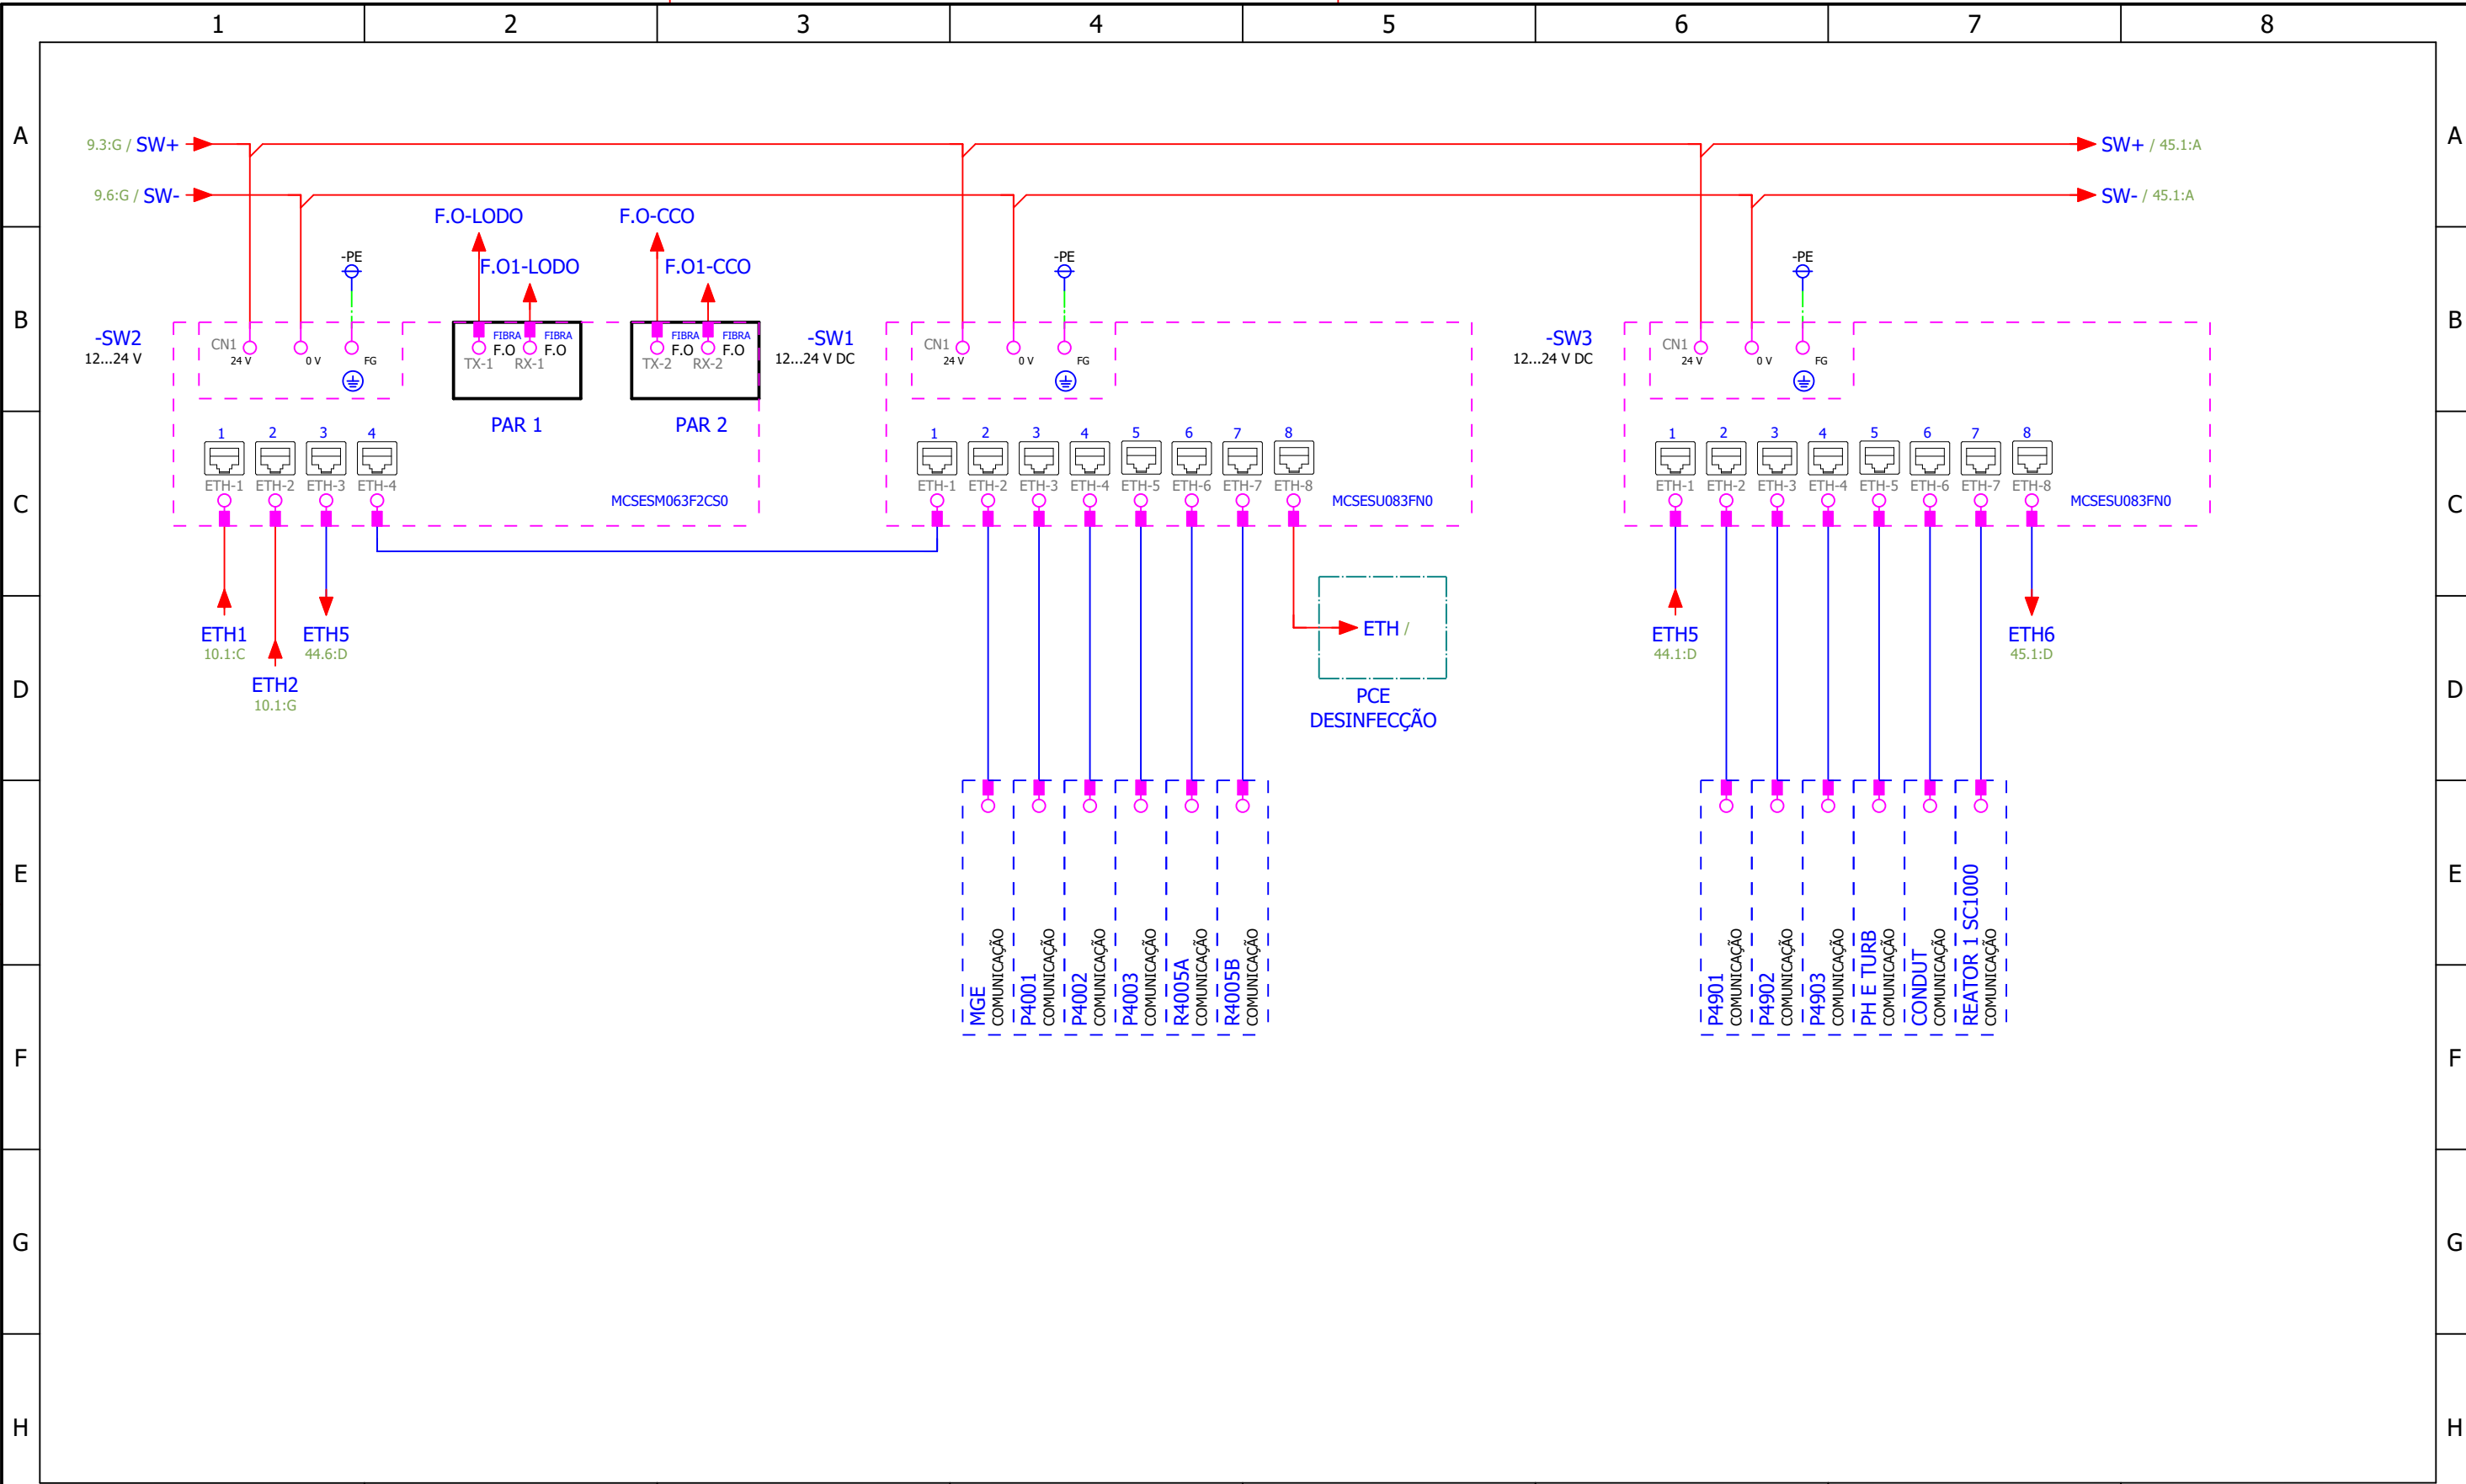

LEGENDA:				
REVISÃO:	EI			
DATA:	03/06/2025			
EXECUÇÃO:	Luiz Corrêa			
VERIFICAÇÃO:	Luiz Corrêa			
APROVAÇÃO:	Rafael Decker			


BRK




CONTRATANTE: BRK AMBIENTAL
CONTRATO Nº: 230317


TÍTULO:		
PCE NEREDA		
SUB-TÍTULO:		
Switch		
UNID. BRK:	MUNIC./EST.:	BAIRRO/ÁREA:
SUMARÉ	SUMARÉ-SP	
RESP. TÊC.: JEAN CARLOS ESSER	APROVAÇÃO BRK AMBIENTAL:	APROVAÇÃO CLIENTE:
CREA: 076760-0/SC		BRK
CÓDIGO DO PROJETO:	ESCALA:	REVISÃO:
HID-PA-DE-ETE-ELQ-005	1:1	EI


FOLHA: 44 / 58

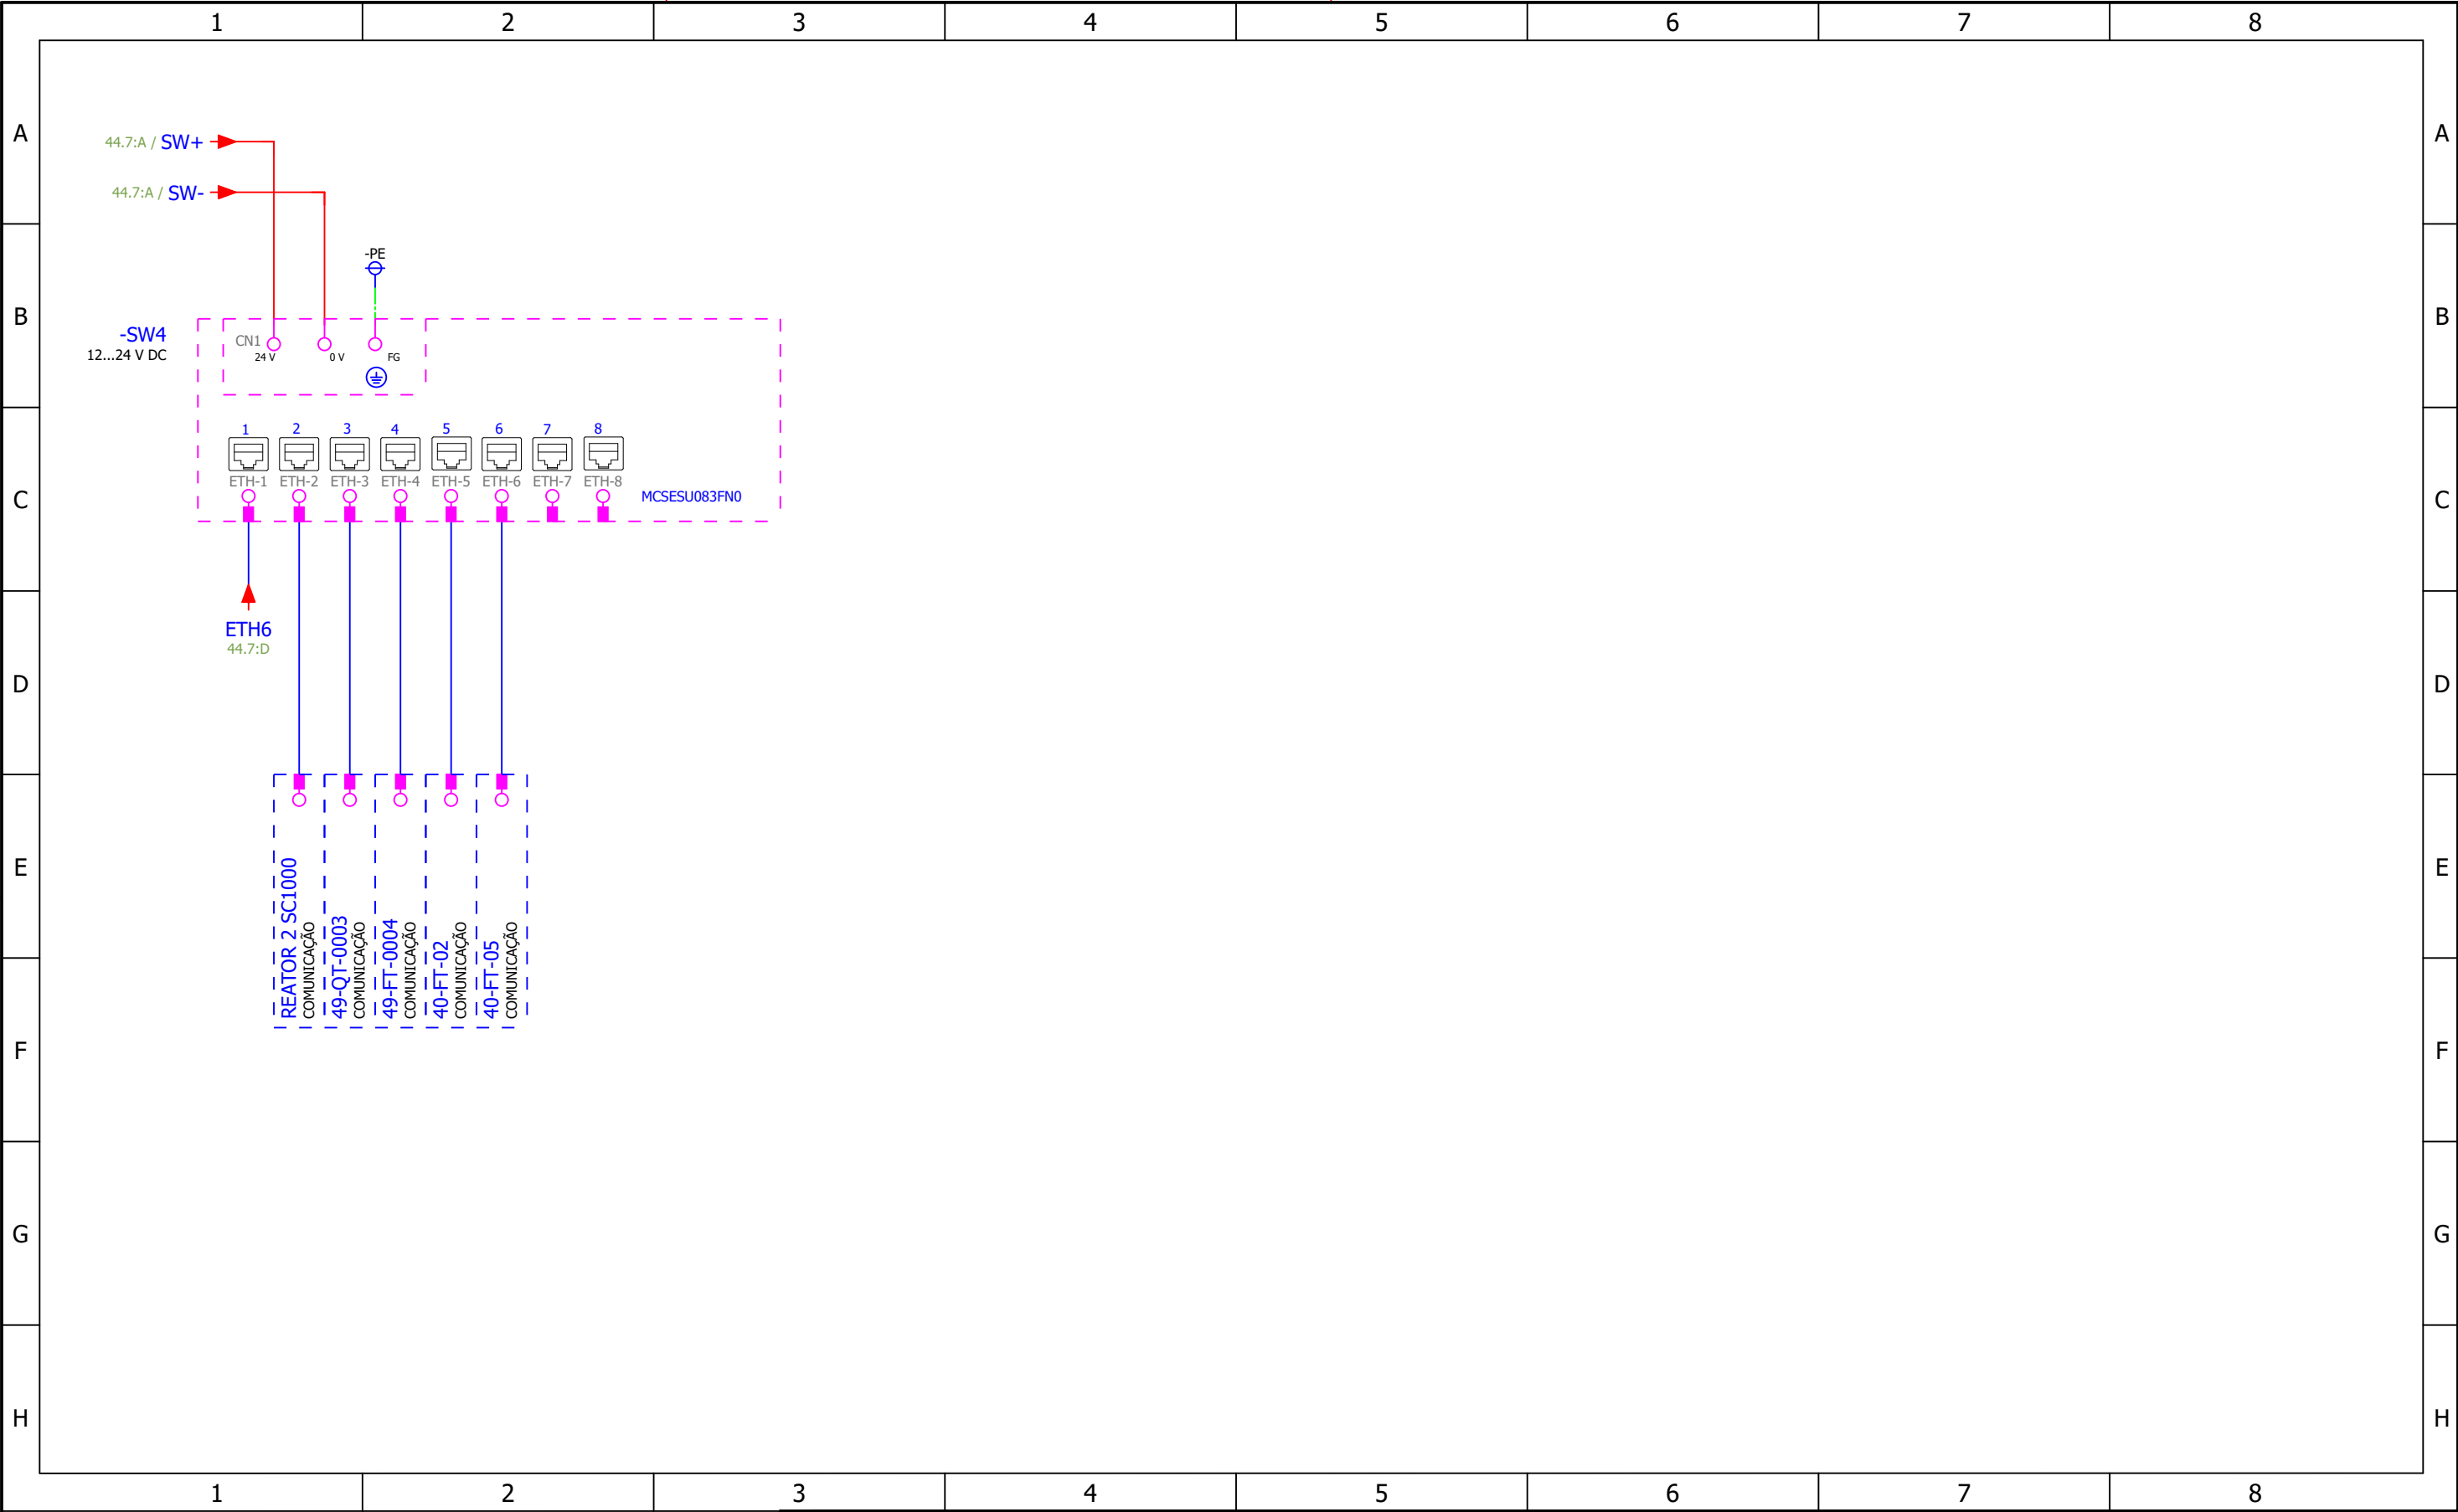



FOLHA: 45 / 58		LEGENDA:							TÍTULO: PCE NEREDA									
									SUB-TÍTULO: Switch									
		REVISÃO:		EI						UNID. BRK: SUMARÉ		MUNIC./EST.: SUMARÉ-SP		BAIRRO/ÁREA:				
		DATA:		03/06/2025						RESP. TÊC.: JEAN CARLOS ESSER		APROVAÇÃO BRK AMBIENTAL:		APROVAÇÃO CLIENTE: BRK				
		EXECUÇÃO:		Luiz Corrêa						CREA: 076760-0/SC								
		VERIFICAÇÃO:		Luiz Corrêa				CONTRATANTE: BRK AMBIENTAL		CONTRATO Nº: 230317		CÓDIGO DO PROJETO: HID-PA-DE-ETE-ELQ-005			ESCALA: 1:1		REVISÃO: EI	
		APROVAÇÃO:		Rafael Decker														

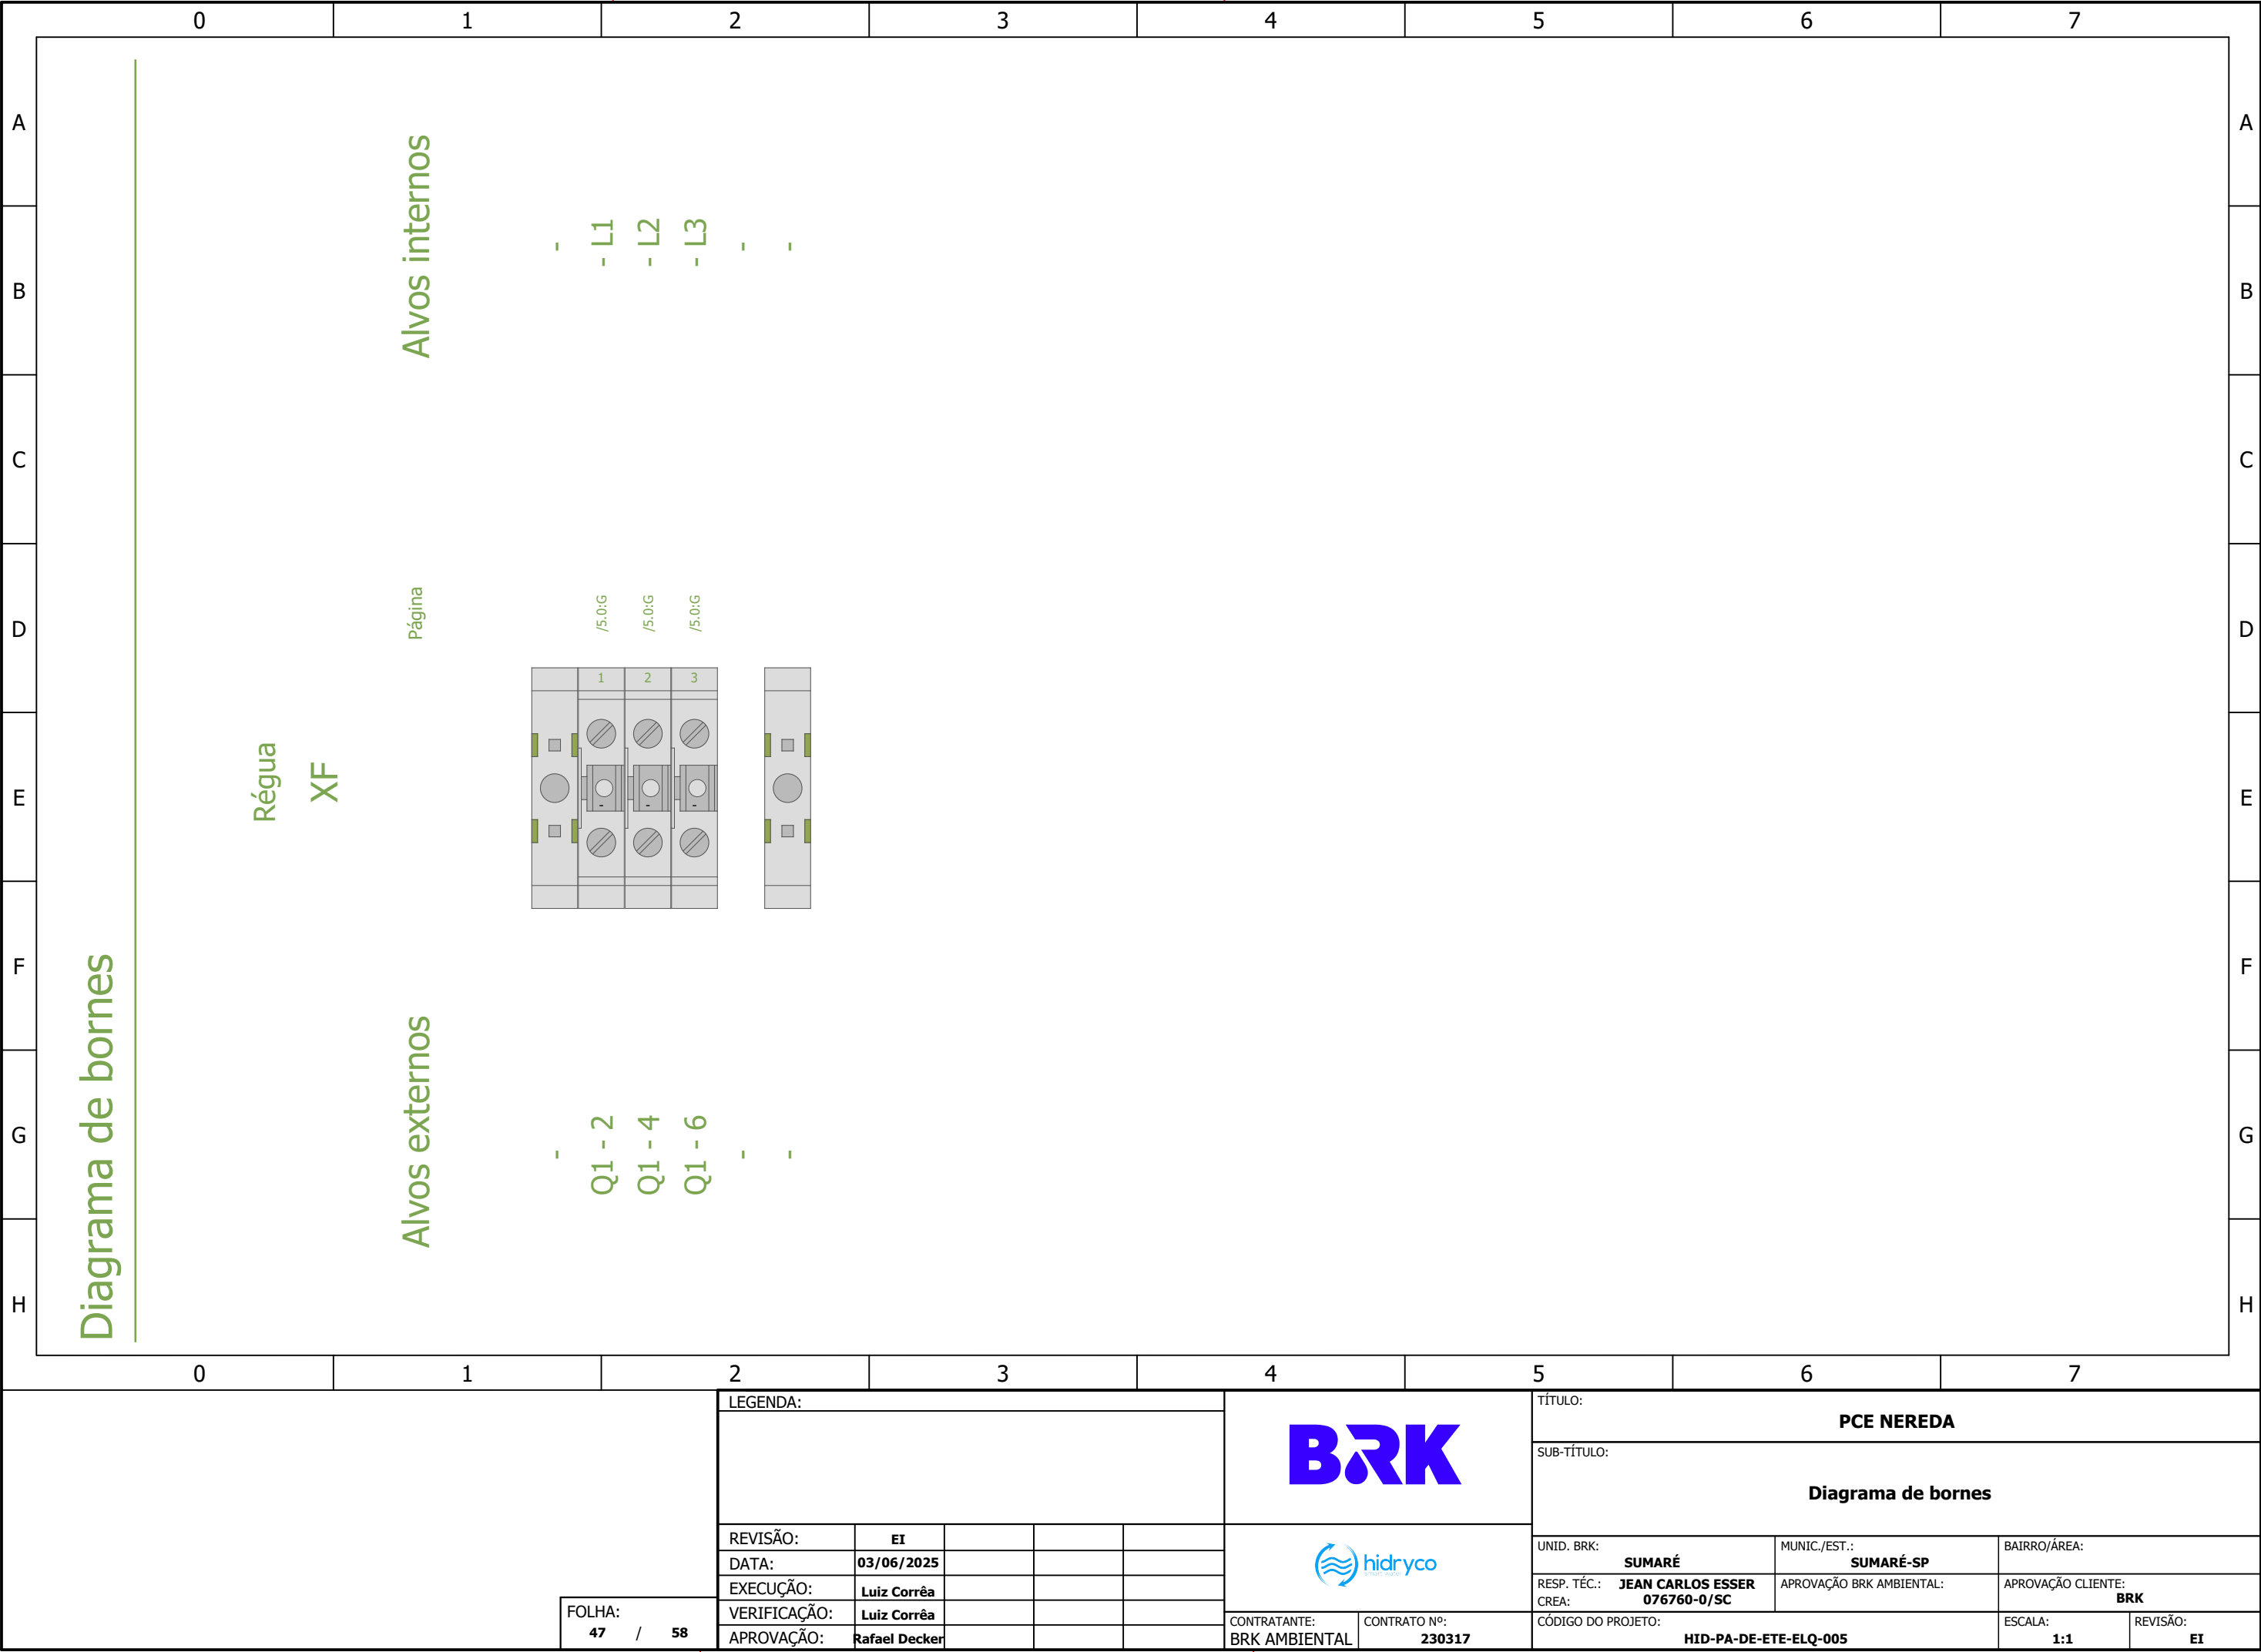

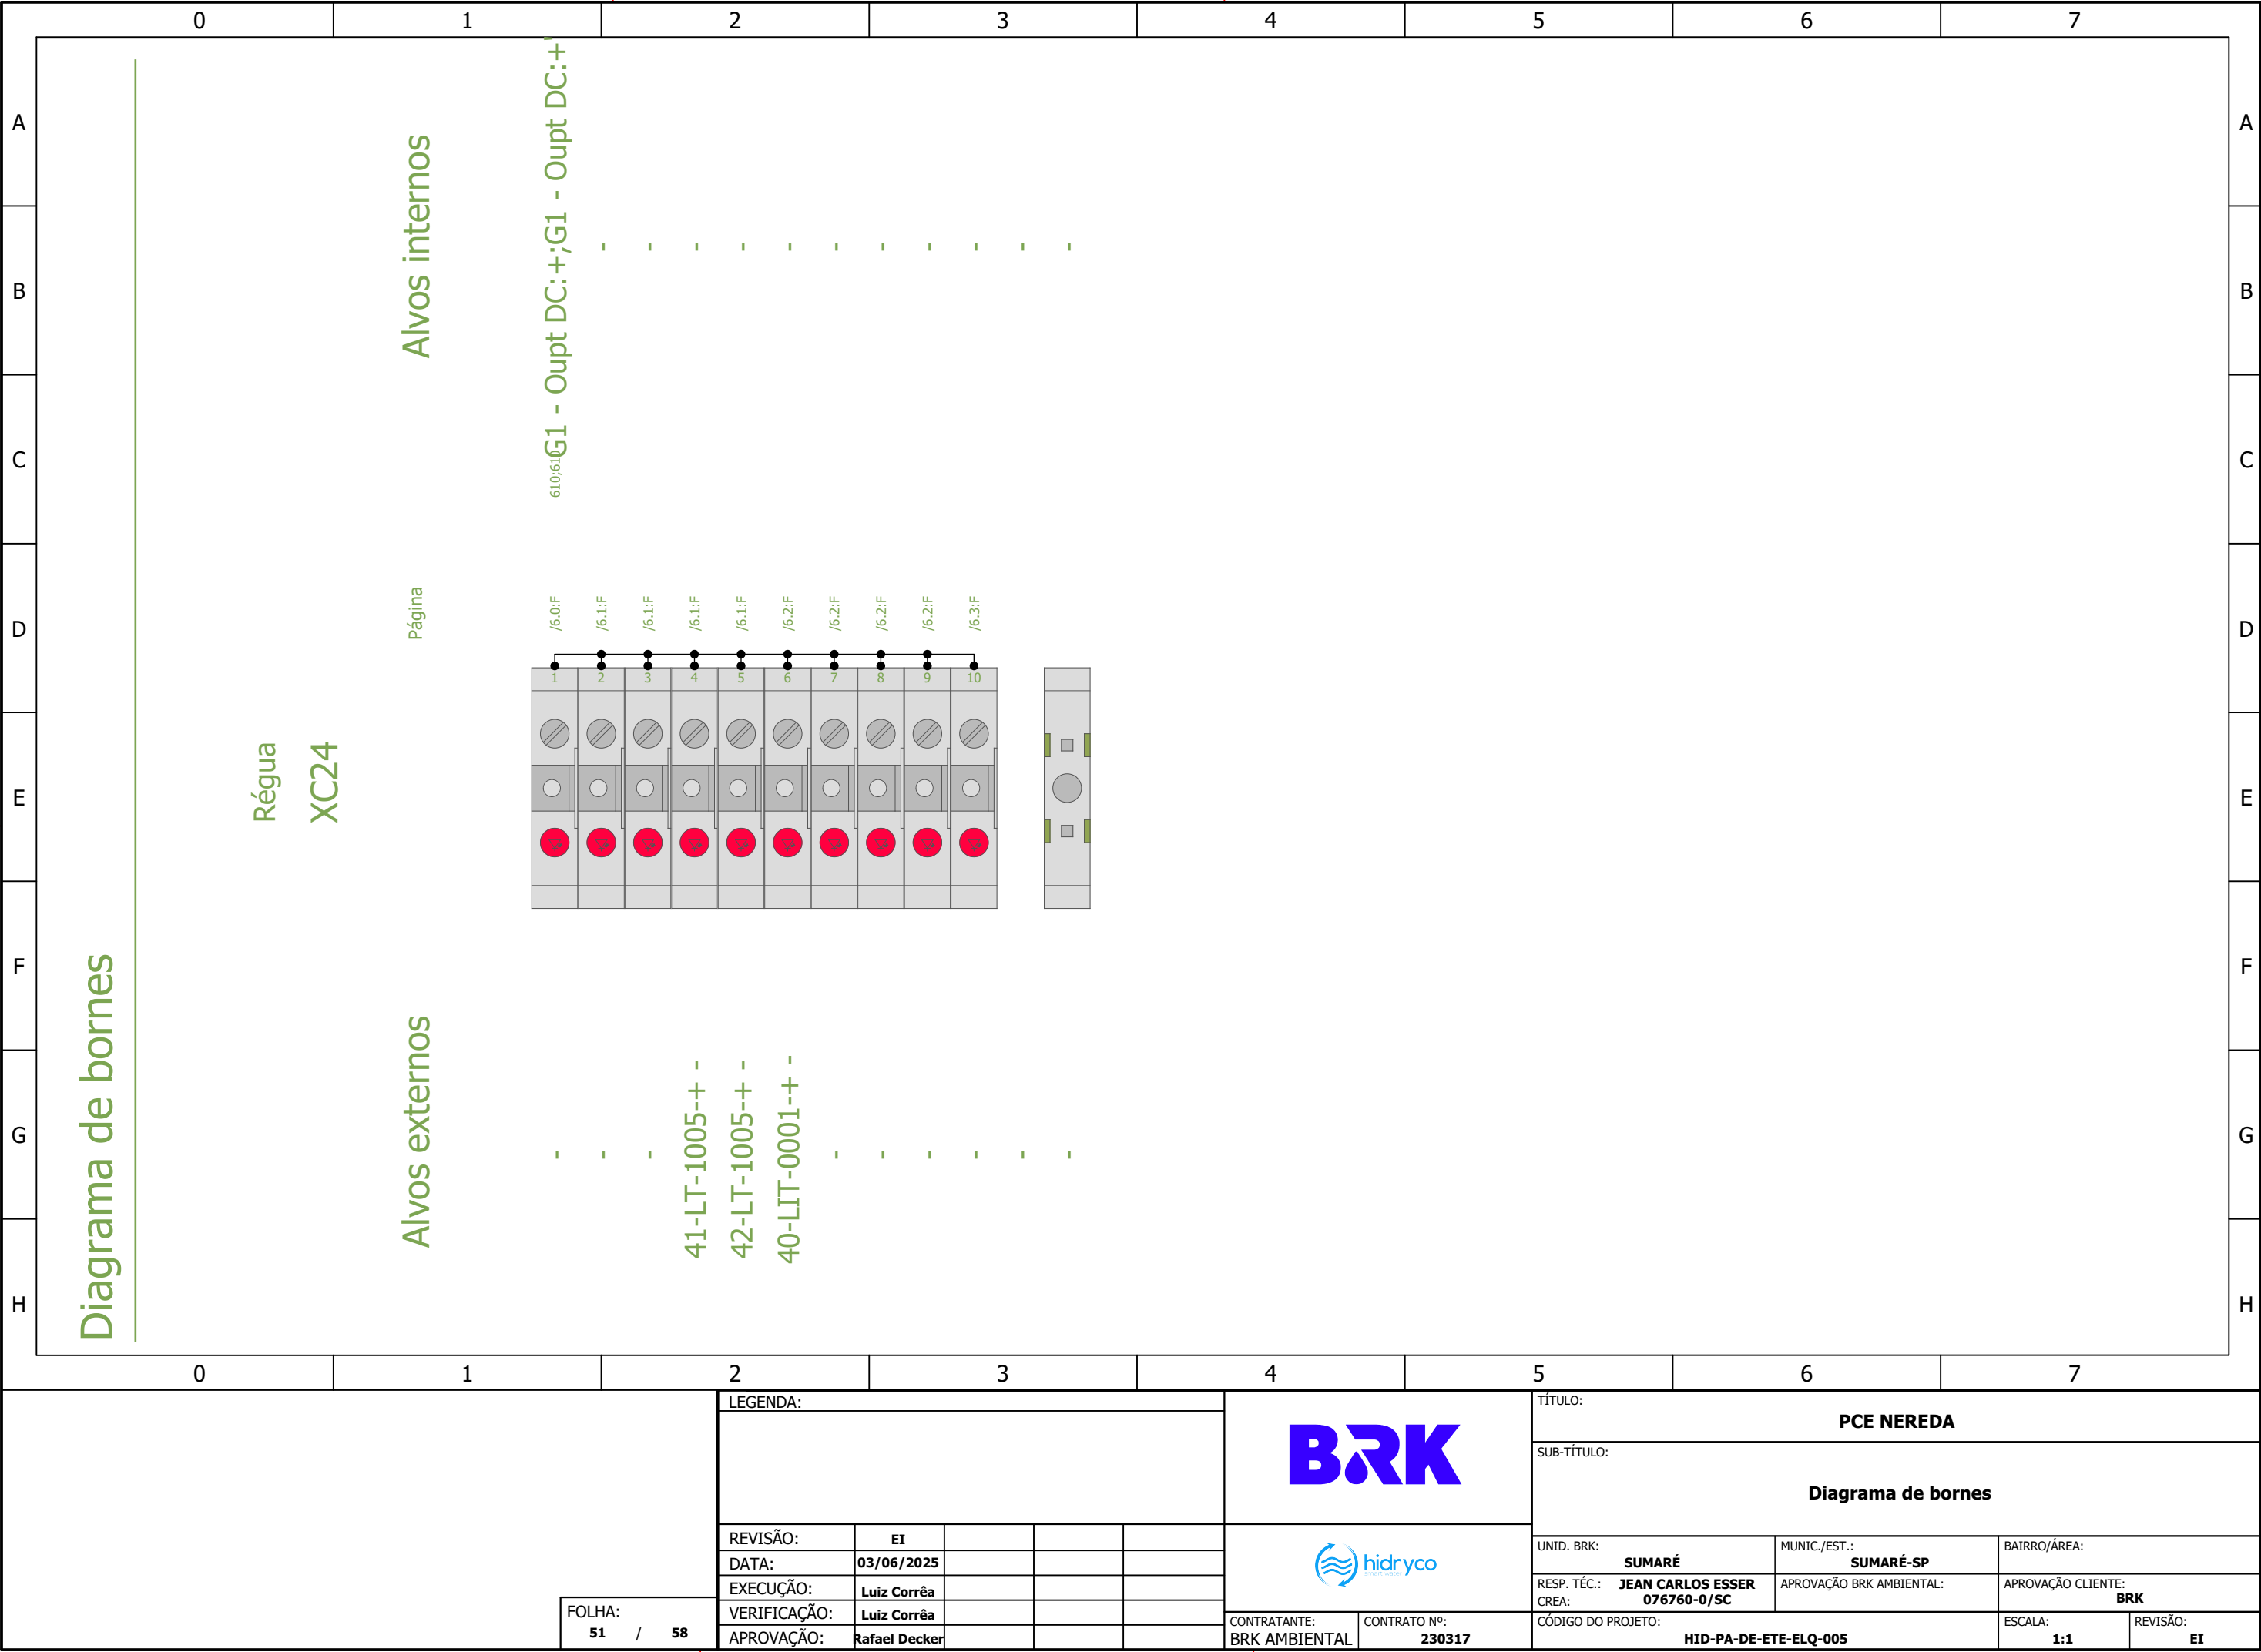

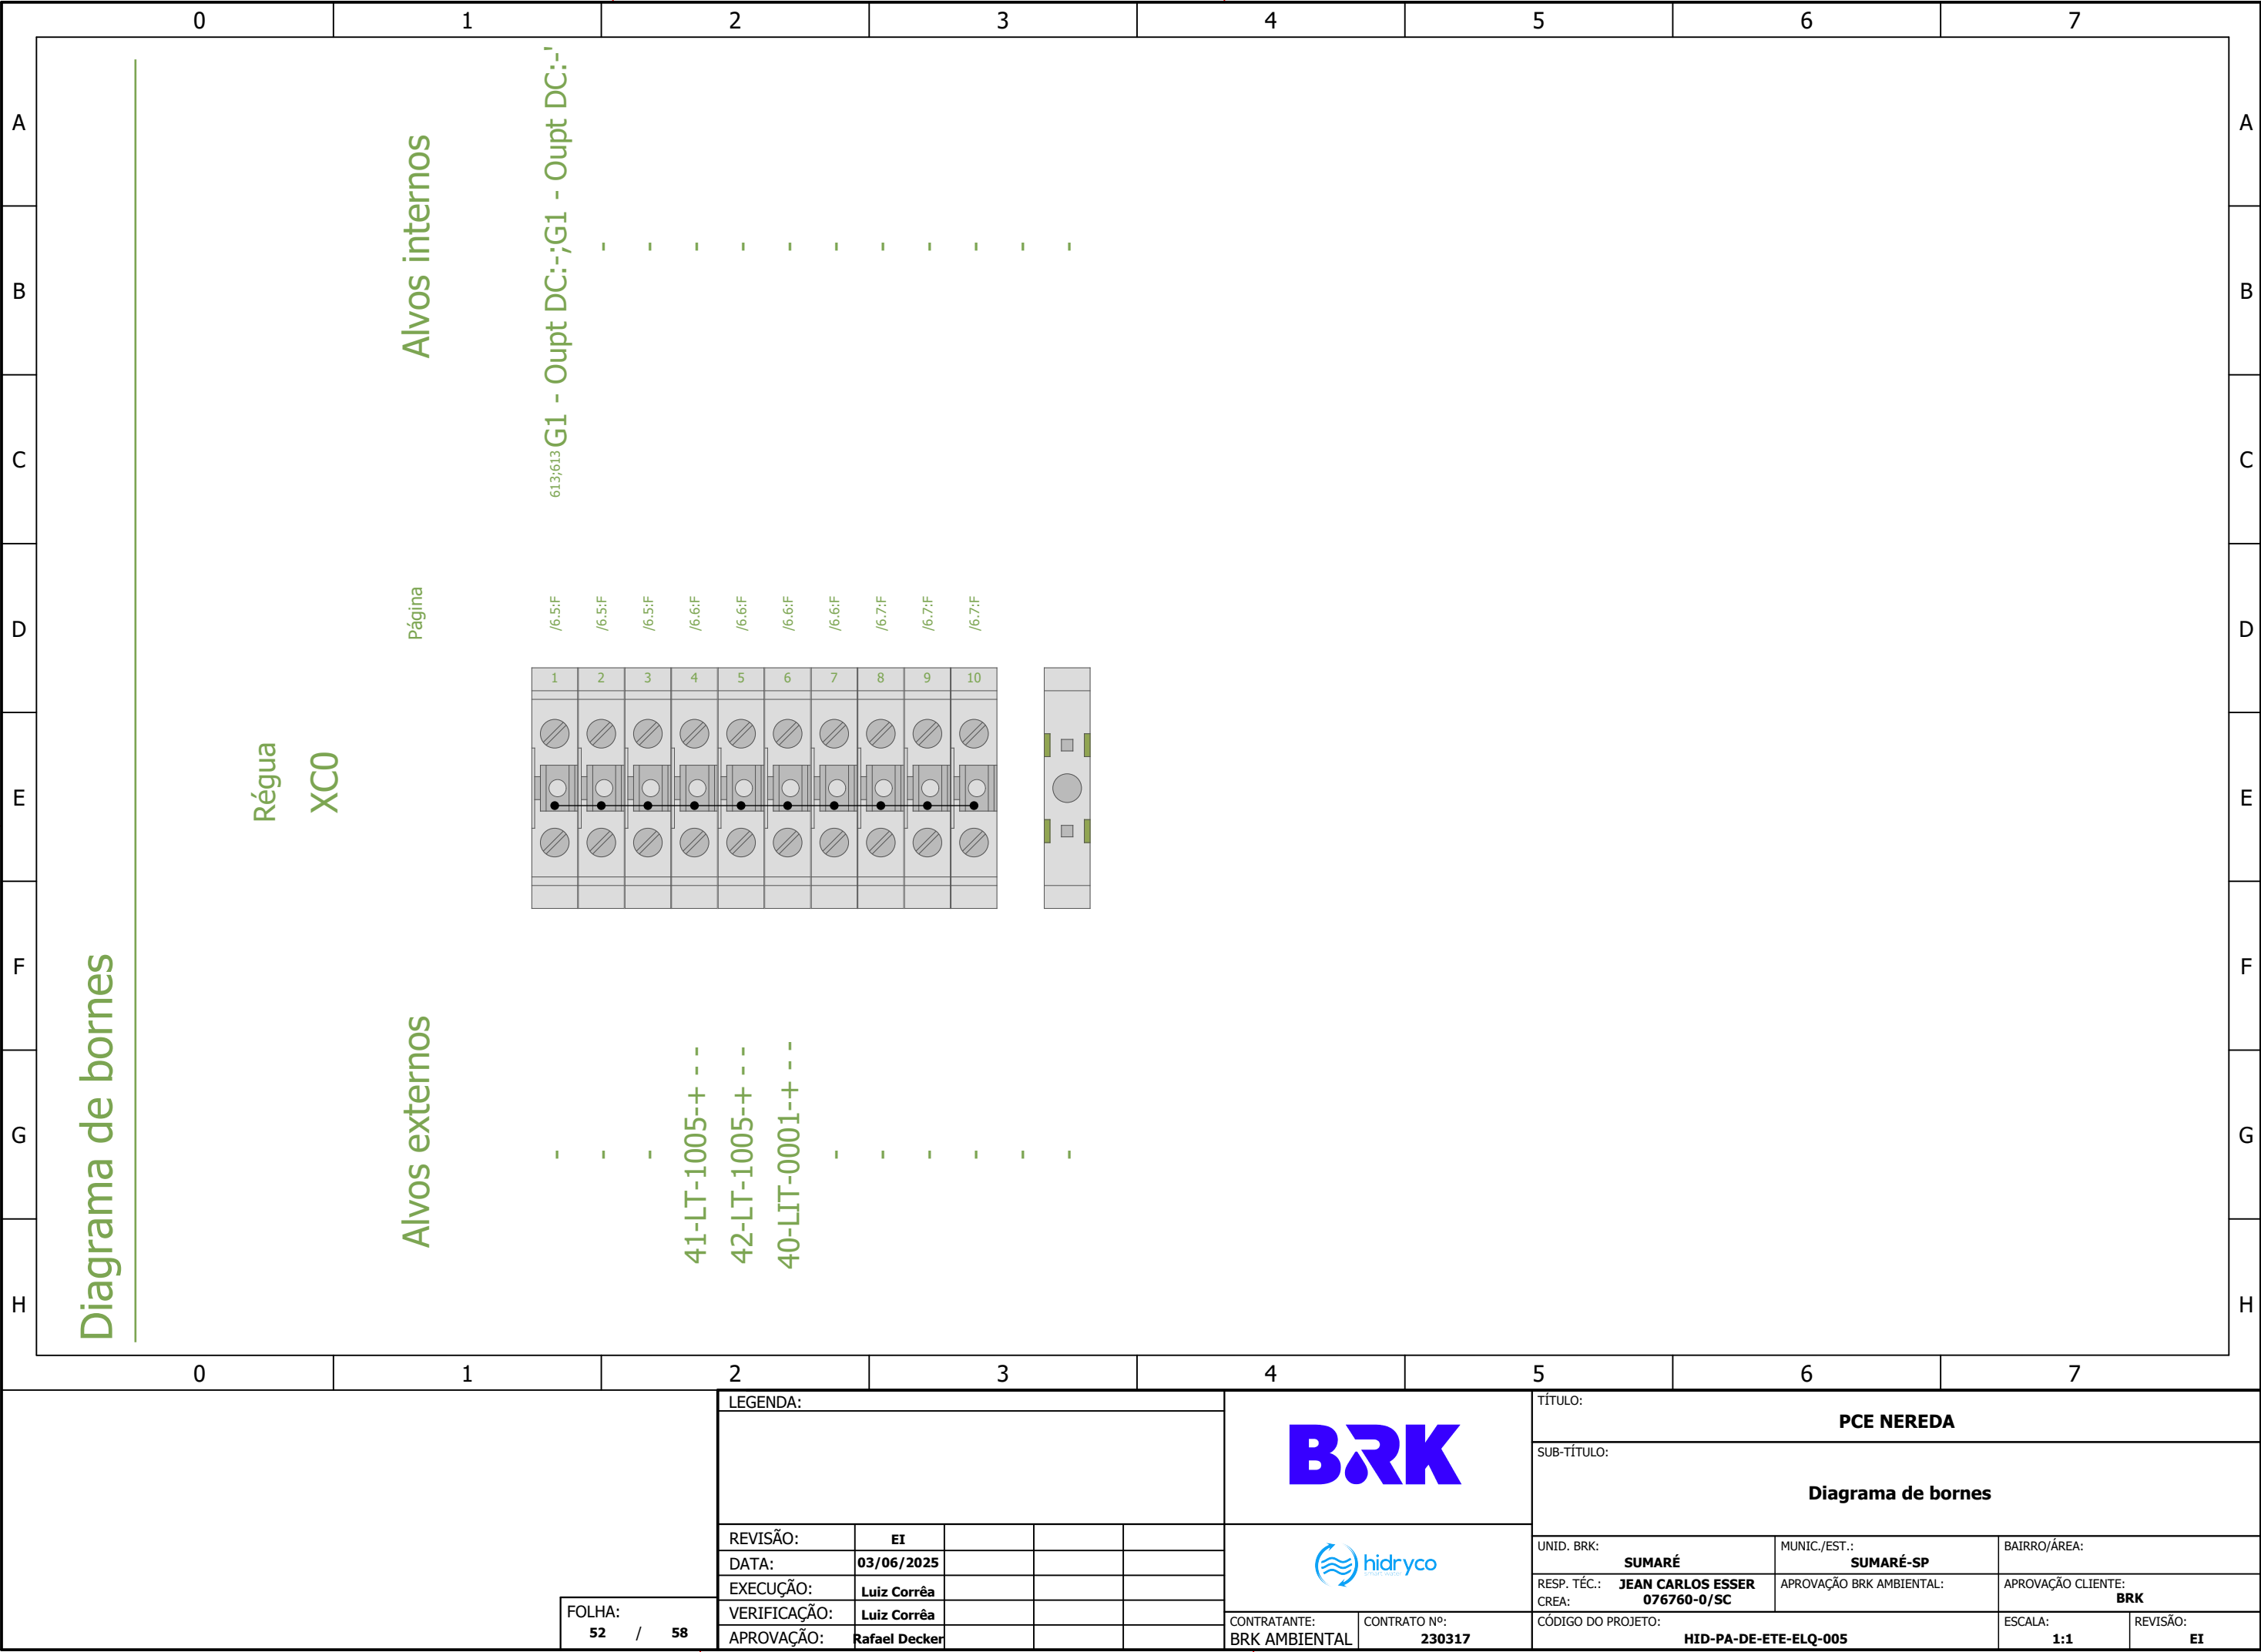

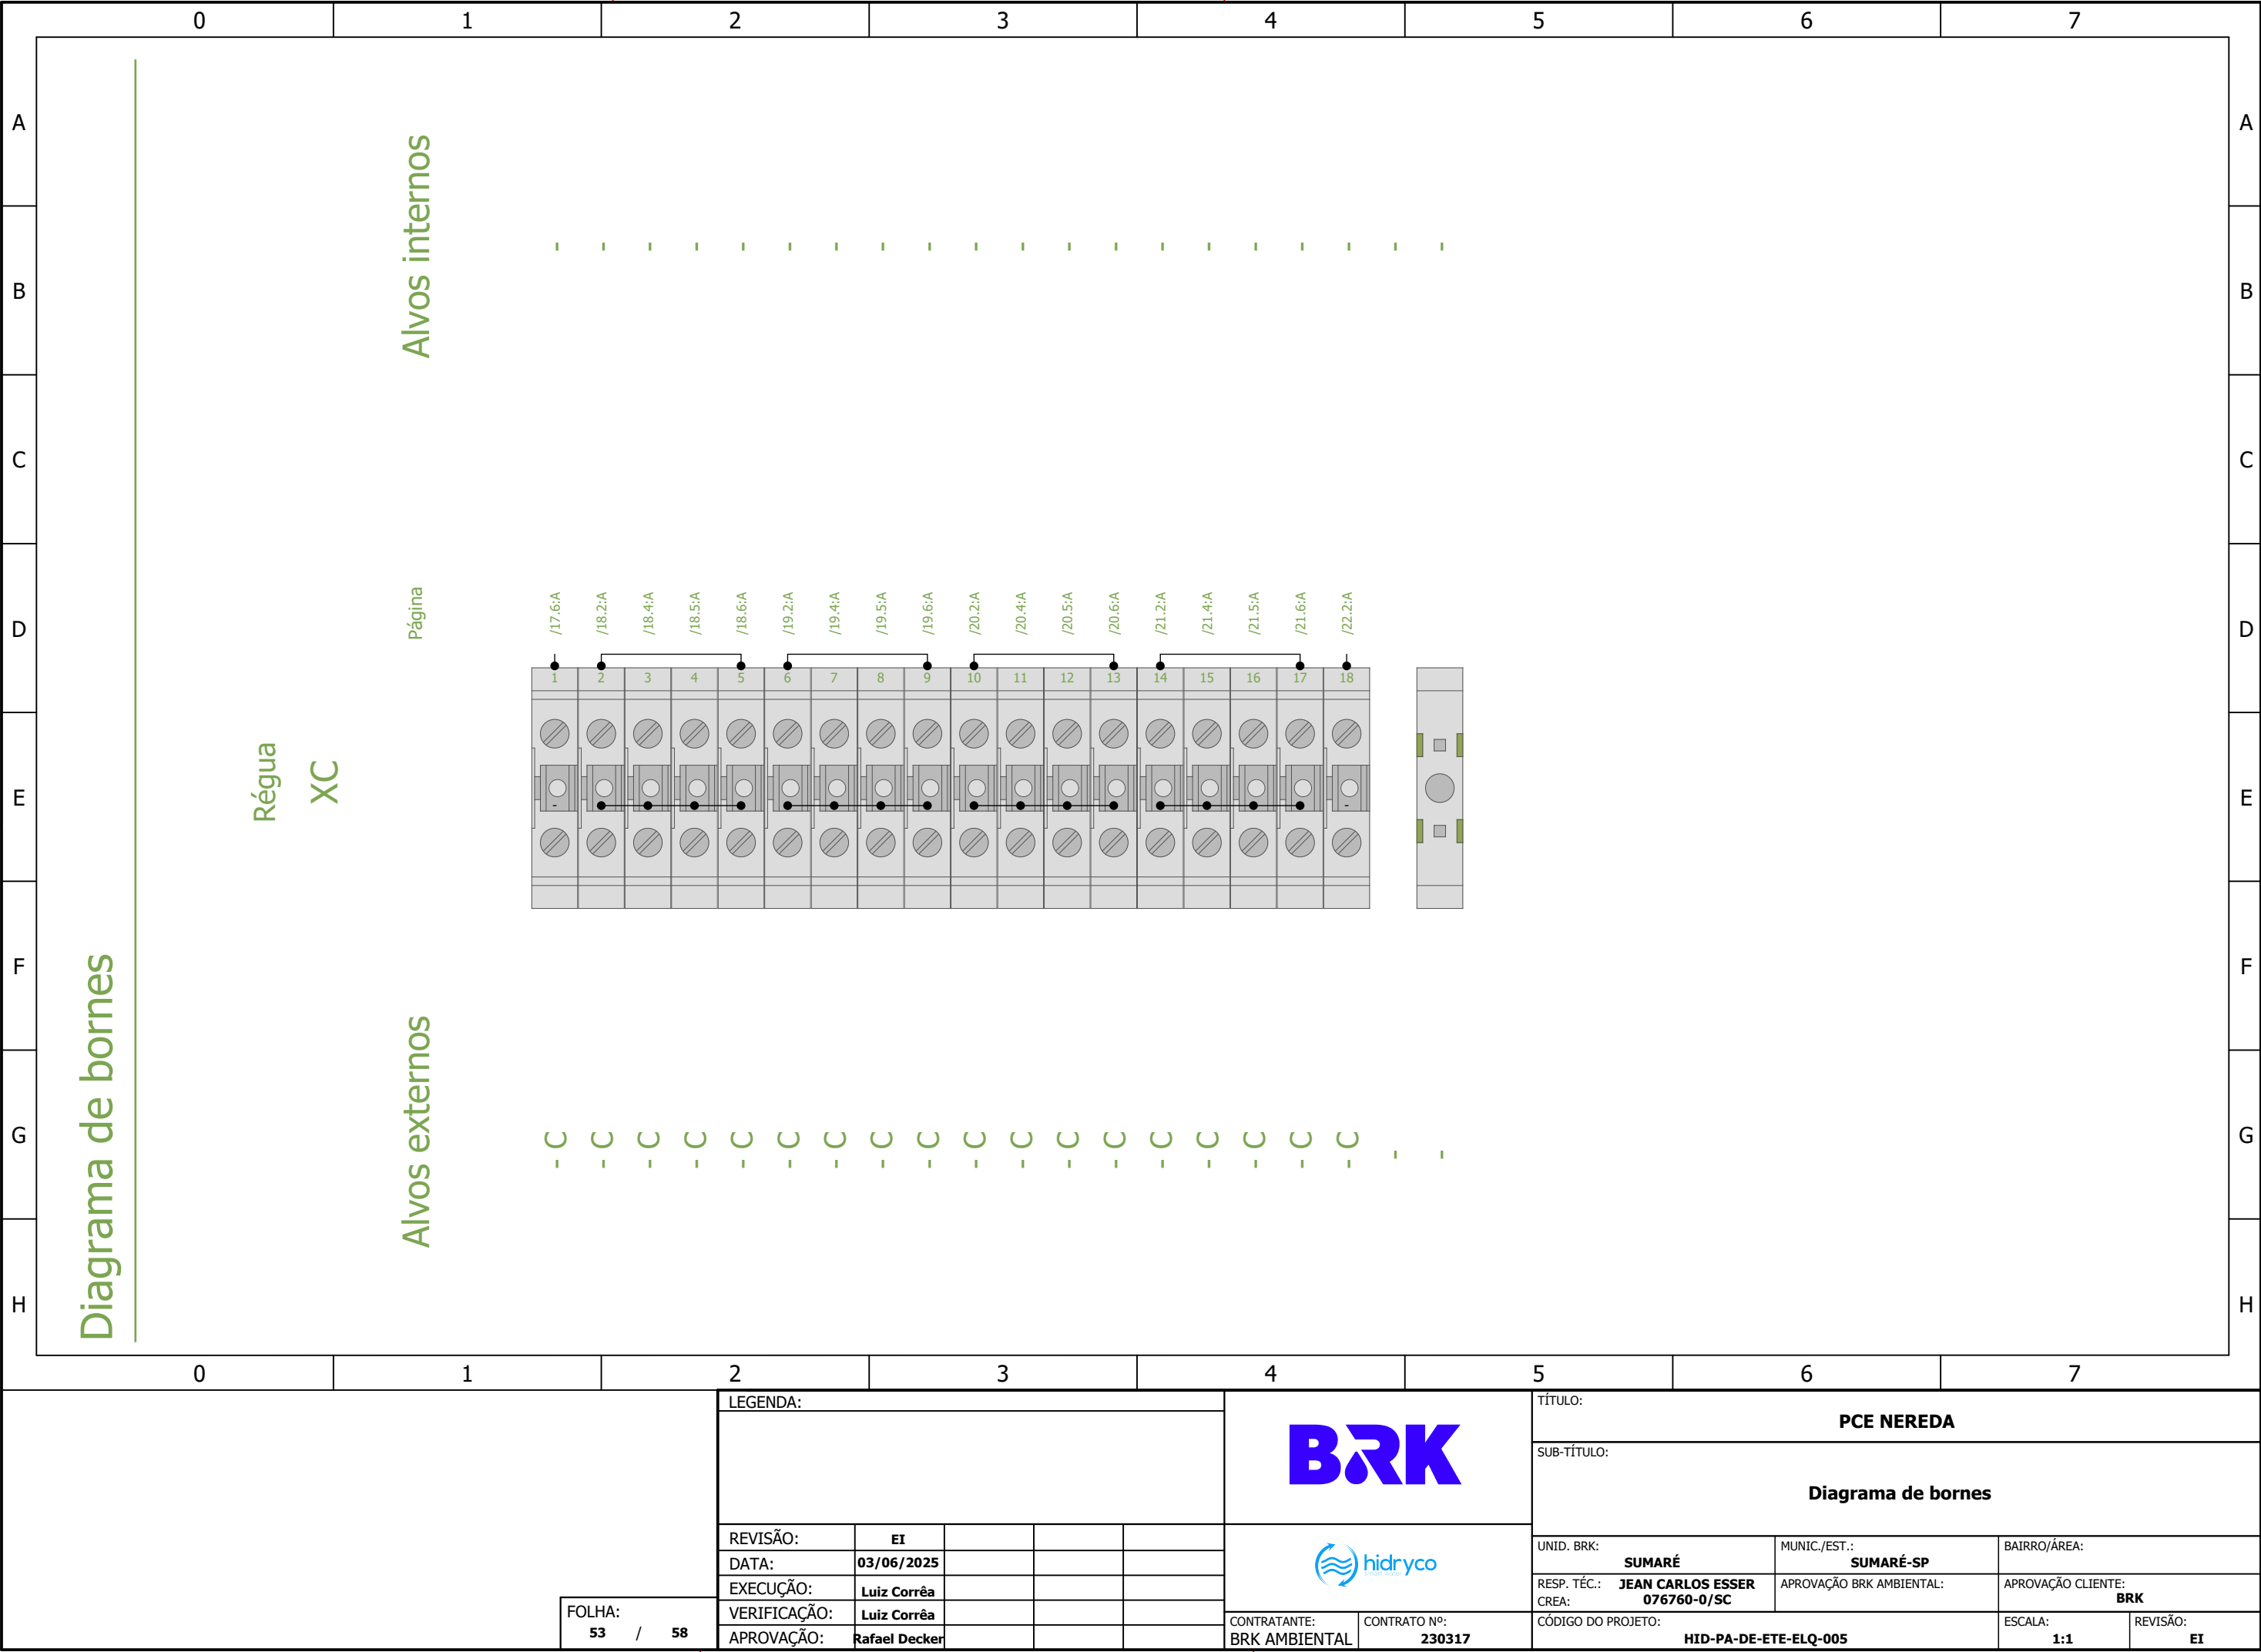

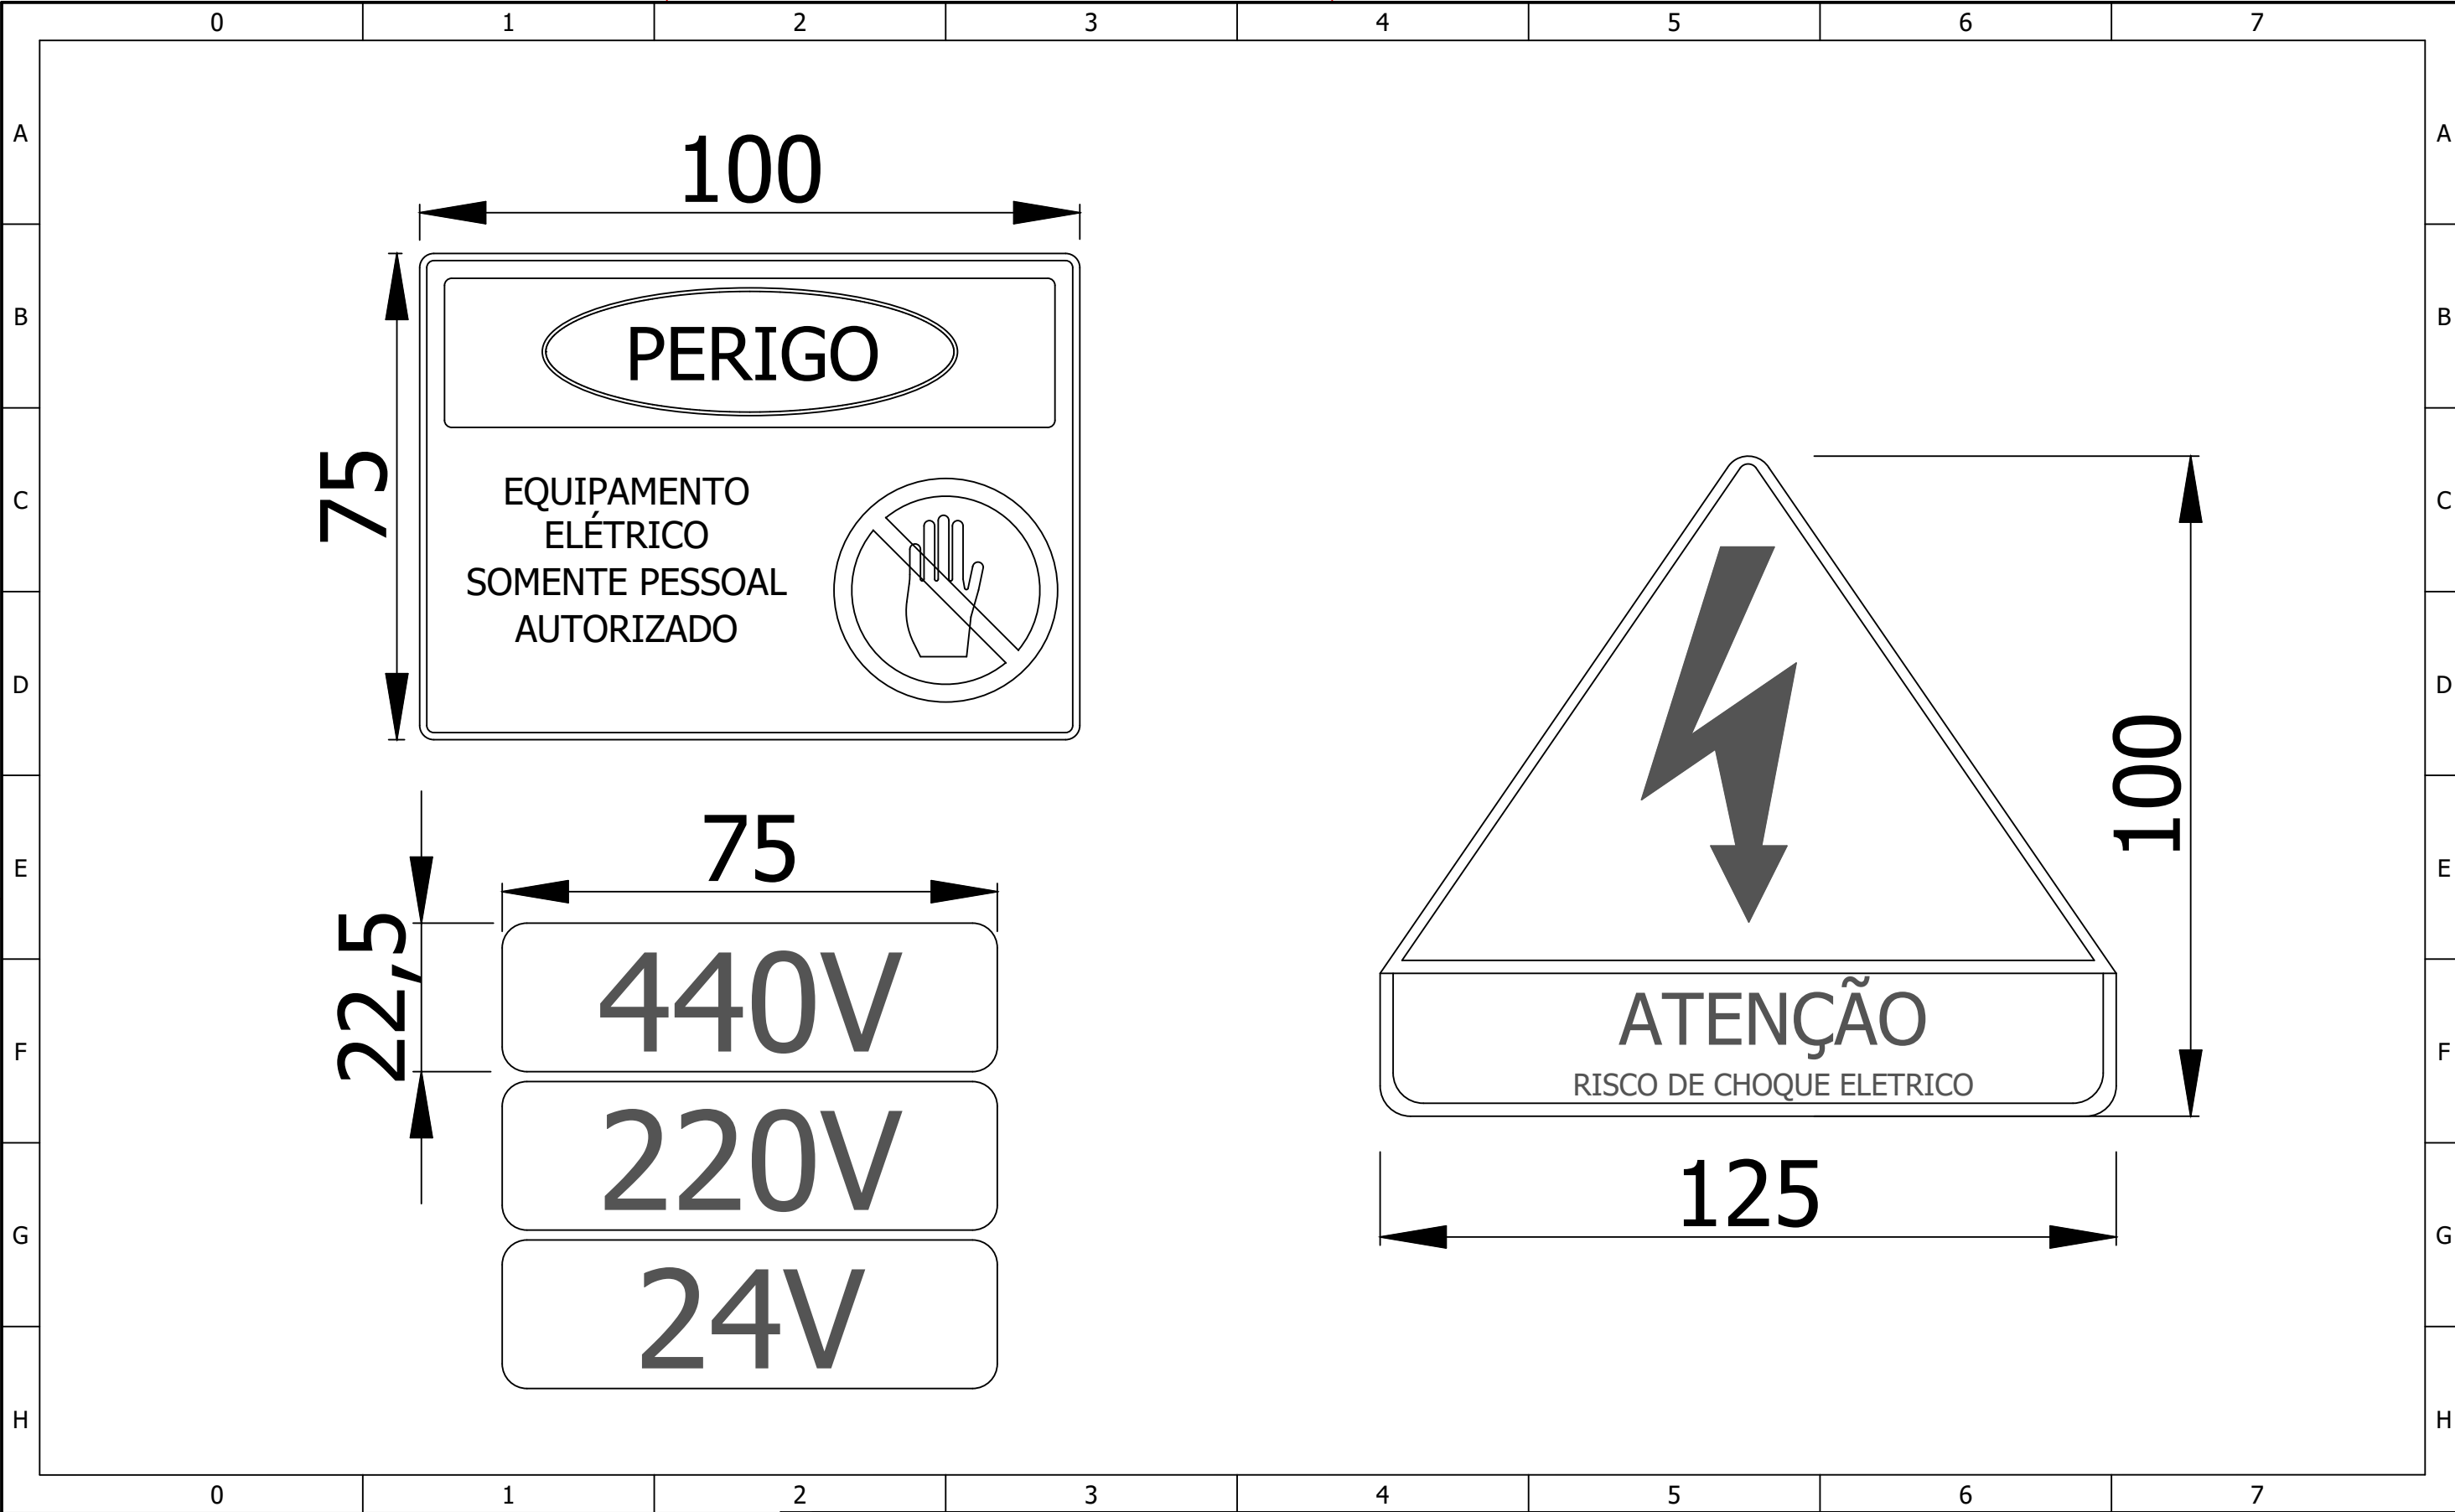

	FOLHA: 54 / 58	LEGENDA:						TÍTULO: PCE NEREDA			
								SUB-TÍTULO: Placas de aviso			
		REVISÃO:	EI					UNID. BRK: SUMARÉ	MUNIC./EST.: SUMARÉ-SP	BAIRRO/ÁREA:	
		DATA:	03/06/2025					RESP. TÉC.: JEAN CARLOS ESSER CREA: 076760-0/SC	APROVAÇÃO BRK AMBIENTAL:	APROVAÇÃO CLIENTE: BRK	
		EXECUÇÃO:	Luiz Corrêa				CÓDIGO DO PROJETO: HID-PA-DE-ETE-ELQ-005			ESCALA: 1:1	REVISÃO: EI
		VERIFICAÇÃO:	Luiz Corrêa				CONTRATANTE: BRK AMBIENTAL	CONTRATO Nº: 230317			
APROVAÇÃO:	Rafael Decker										

0		1		2		3		4		5		6		7					
Lista de Materiais Totalizada																			
Local de montagem		Item	Descrição			Qtde	Unidade	Código Fabricante/Fornecedor			Tag								
		1	PORTA DOCUMENTO PLASTICO A4			1	PÇ	NSYDPA4											
		2	Painel armário 2200+100X1200X600mm - MUNSELL N6,5 - PLACA DE MONTAGEM GALVANIZADA			1	PÇ												
C1	3	Controlador Lógico / Lógica Modicon M262, TM262L ..., 5ns / inst			1	Peça	TM262L10MESE8T			A1									
C1	4	Remota para Entradas e Saídas Distribuídas - Ethernet			2	PÇ	TM3BCEIP			A2;A10									
C1	5	Expansão TM3 32ED			4	PÇ	TM3DI32K			A3...A6									
C1	6	Cabo 20 vias Conectorizado HE10 5 mts			14	Peça	TWDFCW50K			A3...A9									
C1	7	Expansão TM3 32SD			3	PÇ	TM3DQ32TK			A7...A9									
C1	8	Módulo de Expansão 8 entradas analógicas, Conexão parafuso			2	PÇ	TM3AI8			A11;A12									
C1	9	Chave Fim de Curso 1 NF			1	PÇ	MG-2603			B1									
C1	10	Plug 2P+T - Macho 10A			1	PÇ	Plug 2P+T - Macho 10A			CON1									
C1	11	DPS 1P 45KA 275V			3	PÇ	EZ9L33145			DPS1...DPS3									
C1	12	Protetor de Surto Analógico - Máx 300mA - 24V - 10kA			16	PÇ	922.B.0m3.024 FASTER			DPS4...DPS19									
C1	13	Poste 5,15mm			11	PÇ	3022276			DPS11;DPS19;X0;X24;XC;XC0;XC24;XF;XF1									
C1	14	Ventilador 172X150X51 mm - RT-172 - 54101-E			2	PÇ	54101-E			EX1;EX2									
C1	15	Veneziana Com Filtro 291x291mm			2	PÇ	NSYCAG291LPF			EX1;EX2									
C1	16	Fonte de alimentação 100..240VCA / 24VCC 20A			1	PÇ	2910105			G1									
0		1		2		3		4		5		6		7					
FOLHA: 55 / 58				LEGENDA:							TÍTULO: PCE NEREDA								
											SUB-TÍTULO: Lista de peças totalizadas								
				REVISÃO:		EI						UNID. BRK:		SUMARÉ	MUNIC./EST.:	SUMARÉ-SP	BAIRRO/ÁREA:		
				DATA:		03/06/2025						RESP. TÉC.:		JEAN CARLOS ESSER		APROVAÇÃO BRK AMBIENTAL:		APROVAÇÃO CLIENTE:	
				EXECUÇÃO:		Luiz Corrêa						CREA:		076760-0/SC				BRK	
VERIFICAÇÃO:		Luiz Corrêa				CONTRATANTE:		BRK AMBIENTAL		CONTRATO Nº:		230317		CÓDIGO DO PROJETO:					
APROVAÇÃO:		Rafael Decker								HID-PA-DE-ETE-ELQ-005		ESCALA:		1:1	REVISÃO:	EI			
FORMATO: HID-PA-DE-ETE-ELQ-005.DWG																			

0		1		2		3		4		5		6		7								
Lista de Materiais Totalizada																						
A	Local de montagem	Item	Descrição				Qtde	Unidade	Código Fabricante/Fornecedor			Tag										
B	C1	17	FONTE 24 Vcc 10A - 100-240 Vca				1	PCE	ABLS1A24100			G2										
	C1	18	IHM touch 15", 2COM, 2Ethernet, USB, 24VDC				1	Peça	HMIST6700			IHM1										
	C1	19	Led Tubular T5 30cm 6w				1	PÇ	Led Tubular T5 30cm 6w			LP1										
C	C1	20	NOBREAK 230Vca 1000VA 230Vca				1	Peça	SRV1KI-BR			NB1										
	C1	21	Pente Monofásico 3pólos				1	PÇ	Pente Mono - 3P			PI1										
D	C1	22	DJ DIN 3P 10A C 10KA				1	PÇ	A9F74310			Q1										
	C1	23	CONTATO AUXILIAR ACTI9 IOF 1NA/NF PARA DISJUNTOR IC60 24VAC to 415VAC, 24-130 VDC				1	PÇ	A9A26904			Q1										
	C1	24	DJ DIN 2P 06A C 6KA				20	PÇ	EZ9F56206			Q2...Q21										
E	C1	25	DJ DIN 1P 06A C 6KA				1	PÇ	EZ9F33106			Q22										
	C1	26	RELÉ INTERFACE SLIM 6A 1NAF 24Vcc				224	PÇ	RSL1PVBUB			RL1...RL224										
F	C1	27	Switch não gerenciado Modicon - 8 portas para cobre				3	Peça	MCSESU083FN0			SW1;SW3;SW4										
	C1	28	Switch gerenciado Ethernet TCP / IP - 4 RJ45 + 2 FO				1	Peça	MCSESM063F2CS0			SW2										
	C1	29	Termonstato Ventilação NO				1	PÇ	NSYCCOTH0			TERM1										
G	C1	30	TOMADA 2P+T 10A PARA TRILHO				1	PÇ	CSW10A			TM1										
	C1	31	TOMADA 2P+T 20A PARA TRILHO				1	PÇ	CSW20A			TM2										
H	C1	32	Cabo PVC 2,5mm² Preto				1	MT	PVC 2,5 Preto			W1										
0		1		2		3		4		5		6		7								
FOLHA: 56 / 58				LEGENDA:							TÍTULO: PCE NEREDA											
											SUB-TÍTULO: Lista de peças totalizadas											
									REVISÃO:		EI				UNID. BRK:		SUMARÉ	MUNIC./EST.:	SUMARÉ-SP	BAIRRO/ÁREA:		
									DATA:		03/06/2025						RESP. TÉC.: JEAN CARLOS ESSER		APROVAÇÃO BRK AMBIENTAL:		APROVAÇÃO CLIENTE: BRK	
				EXECUÇÃO:		Luiz Corrêa				CREA:		076760-0/SC										
				VERIFICAÇÃO:		Luiz Corrêa				CONTRATANTE:		BRK AMBIENTAL	CONTRATO Nº:		230317	CÓDIGO DO PROJETO:		HID-PA-DE-ETE-ELQ-005	ESCALA:	1:1	REVISÃO:	EI
				APROVAÇÃO:		Rafael Decker																
FORMATO:																HID-PA-DE-ETE-ELQ-005.DWG						

0		1		2		3		4		5		6		7	
Lista de Materiais Totalizada															
Local de montagem	Item	Descrição				Qtde	Unidade	Código Fabricante/Fornecedor				Tag			
C1	33	Cabo PVC 6,0mm² Verde				10	MT	PVC 6,0 Verde				W3			
C1	34	Multilan CAT.5e F/UTP - Blindado				2	MT	Multilan CAT.5e F/UTP - Blindado				W5			
C1	35	CAPA PARA CONECTOR RJ45 - AZUL				4	PÇ	CAPA PARA CONECTOR RJ45 - AZUL				W5			
C1	36	RJ 45 Macho CAT5e Blindado para cabo sólido ou flexível				4	PÇ	35050206				W5			
C1	37	Multilan CAT.5e F/UTP - Blindado				2	MT	Multilan CAT.5e F/UTP - Blindado				W6;W7			
C1	38	CAPA PARA CONECTOR RJ45 - AZUL				4	PÇ	CAPA PARA CONECTOR RJ45 - AZUL				W6;W7			
C1	39	RJ 45 Macho CAT5e Blindado para cabo sólido ou flexível				4	PÇ	35050206				W6;W7			
C1	40	Borne de passagem "Push In" 2,5				70	PÇ	3209510				X0;XC;XC0;XF1			
C1	41	Tampa terminal D-ST 2,5				4	PÇ	3030417				X0;XC;XC0;XF1			
C1	42	Borne fusível, 24 VAC/DC, C/ LED				20	PÇ	3211903				X24;XC24			
C1	43	Fusível de Vidro 5X20 1A 250V				6	PÇ	Fusível de vidro 1A 250V				X24			
C1	44	Fusível de Vidro 5X20 0,5A 250V				22	PÇ	Fusível de vidro 0,5A 250V				X24;XC24			
C1	45	Fusível de Vidro 5X20 2A 250V				12	PÇ	Fusível de vidro 2A 250V				X24;XC24			
C1	46	Tampa terminal D-ST 4				3	PÇ	3030420				X24;XC24;XF			
C1	47	Borne de passagem "Push In" 4				3	PÇ	3211757				XF			
0		1		2		3		4		5		6		7	
FOLHA: 57 / 58				LEGENDA:						TÍTULO: PCE NEREDA					
										SUB-TÍTULO: Lista de peças totalizadas					
				REVISÃO:		EI				UNID. BRK:		MUNIC./EST.:		BAIRRO/ÁREA:	
				DATA:		03/06/2025				SUMARÉ		SUMARÉ-SP			
				EXECUÇÃO:		Luiz Corrêa				RESP. TÉC.:		JEAN CARLOS ESSER		APROVAÇÃO BRK AMBIENTAL:	
				VERIFICAÇÃO:		Luiz Corrêa		CONTRATANTE: BRK AMBIENTAL		CONTRATO Nº: 230317		CREA:		076760-0/SC	
APROVAÇÃO:		Rafael Decker		CÓDIGO DO PROJETO: HID-PA-DE-ETE-ELQ-005								ESCALA: 1:1		REVISÃO: EI	
FORMATO: HID-PA-DE-ETE-ELQ-005.DWG															